


Маркировочный план фрагмента 5 этажа в осях 12-18/Д-Р

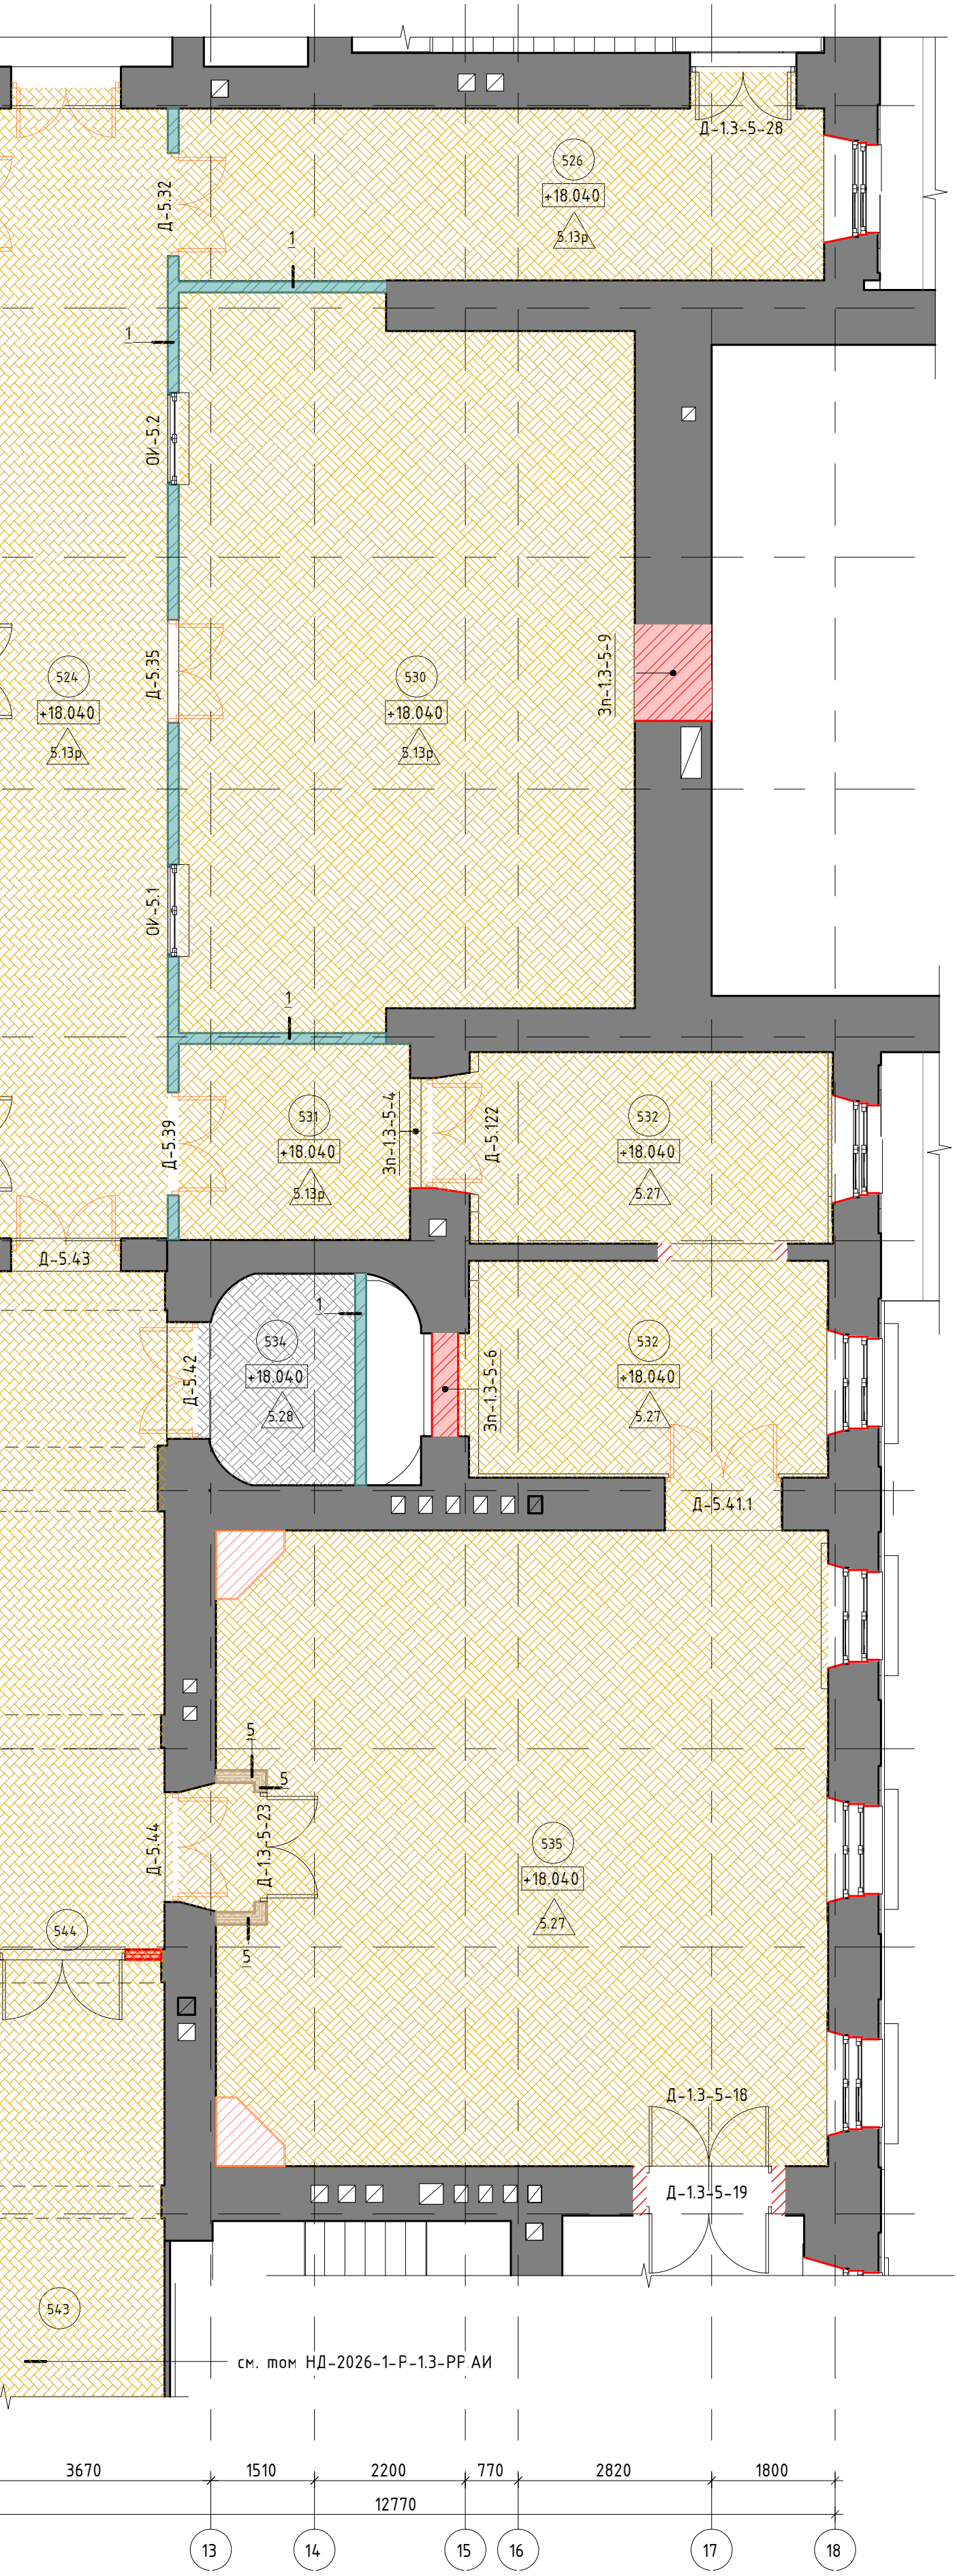

Маркировочный план фрагмента 5 этажа в осях 1-13/А-Г (1 : 75)

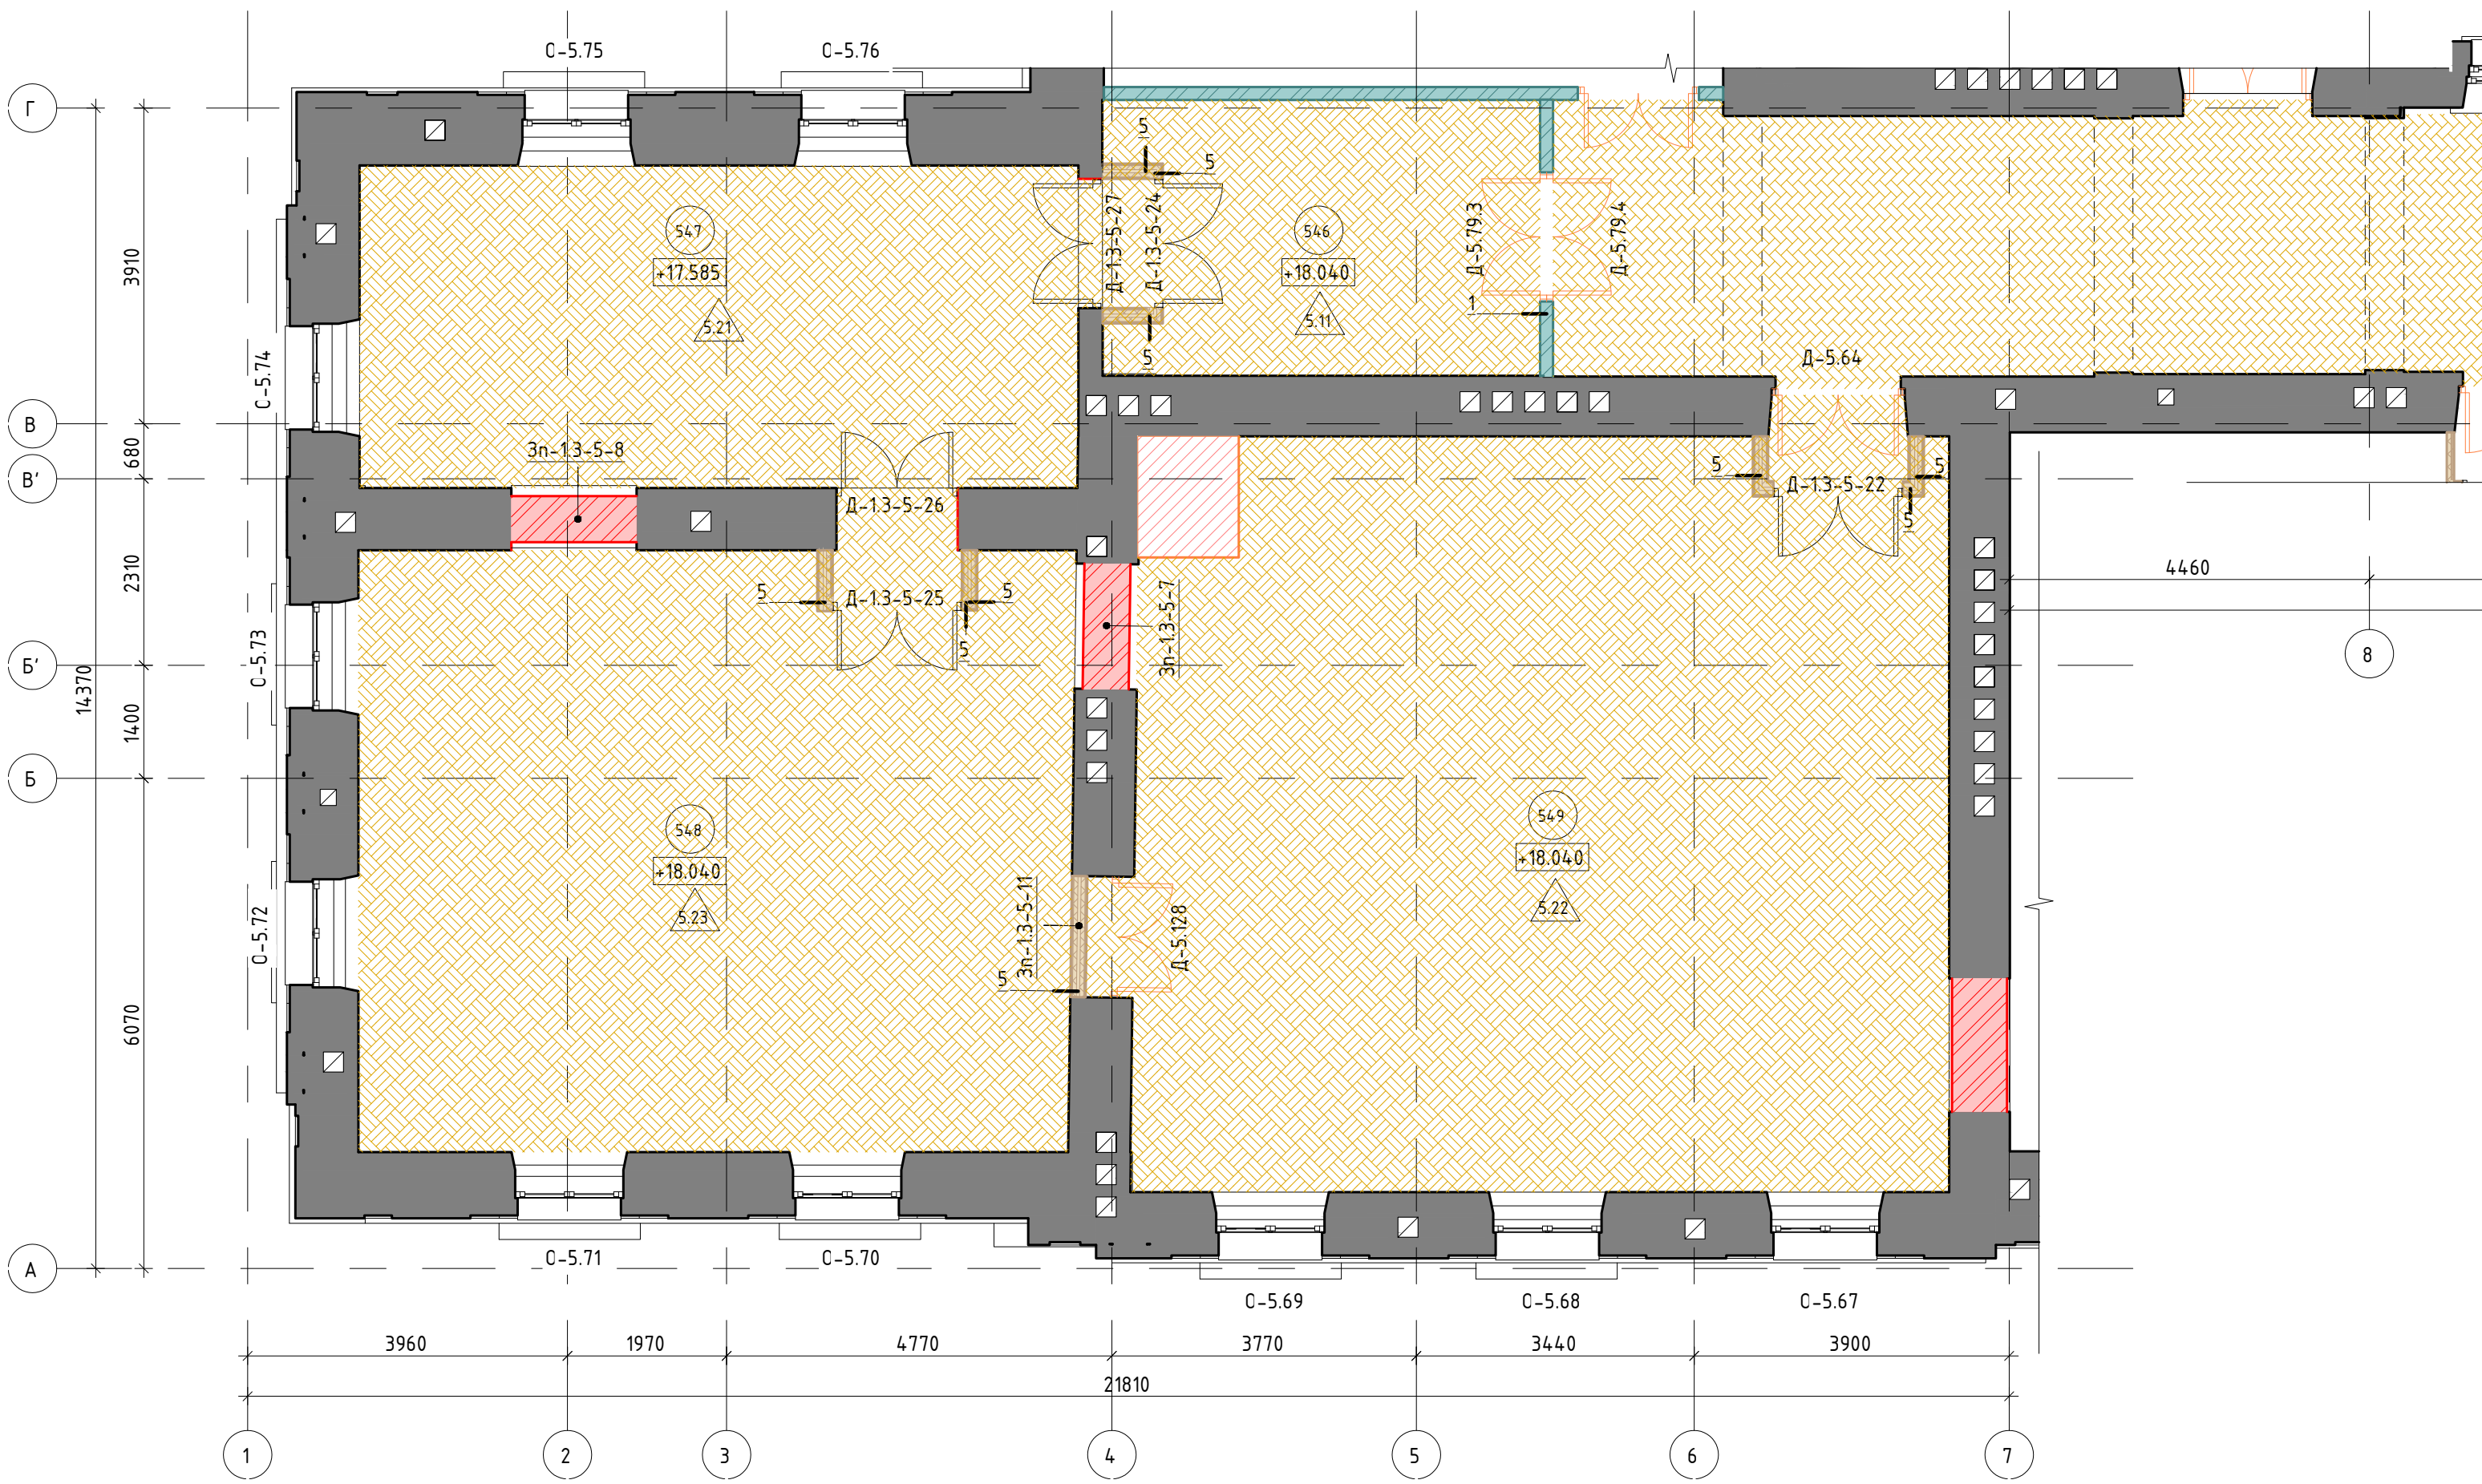


Рисунок паркета "корзинка". М 1:15


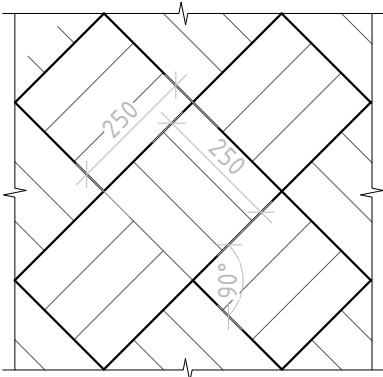


Рисунок паркета "ёлочка". М 1:15

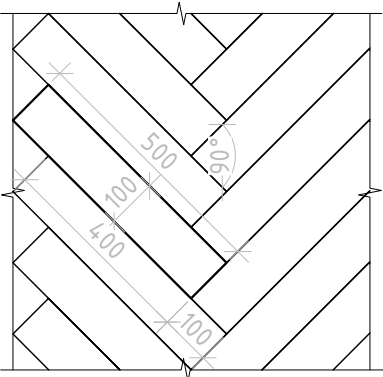

- Паркет "корзинка" в ПО
- Паркет "корзинка" не в ПО
- Паркет "ёлочка" в ПО
- Паркет "ёлочка" не в ПО

- Условные обозначения:
- 1 - Ось координации
 - +0,000 - Отметка уровня
 - Реставрируемые помещения
 - Сохраняемые конструкции
 - Продвижаемый проем
 - Закладываемый проем