


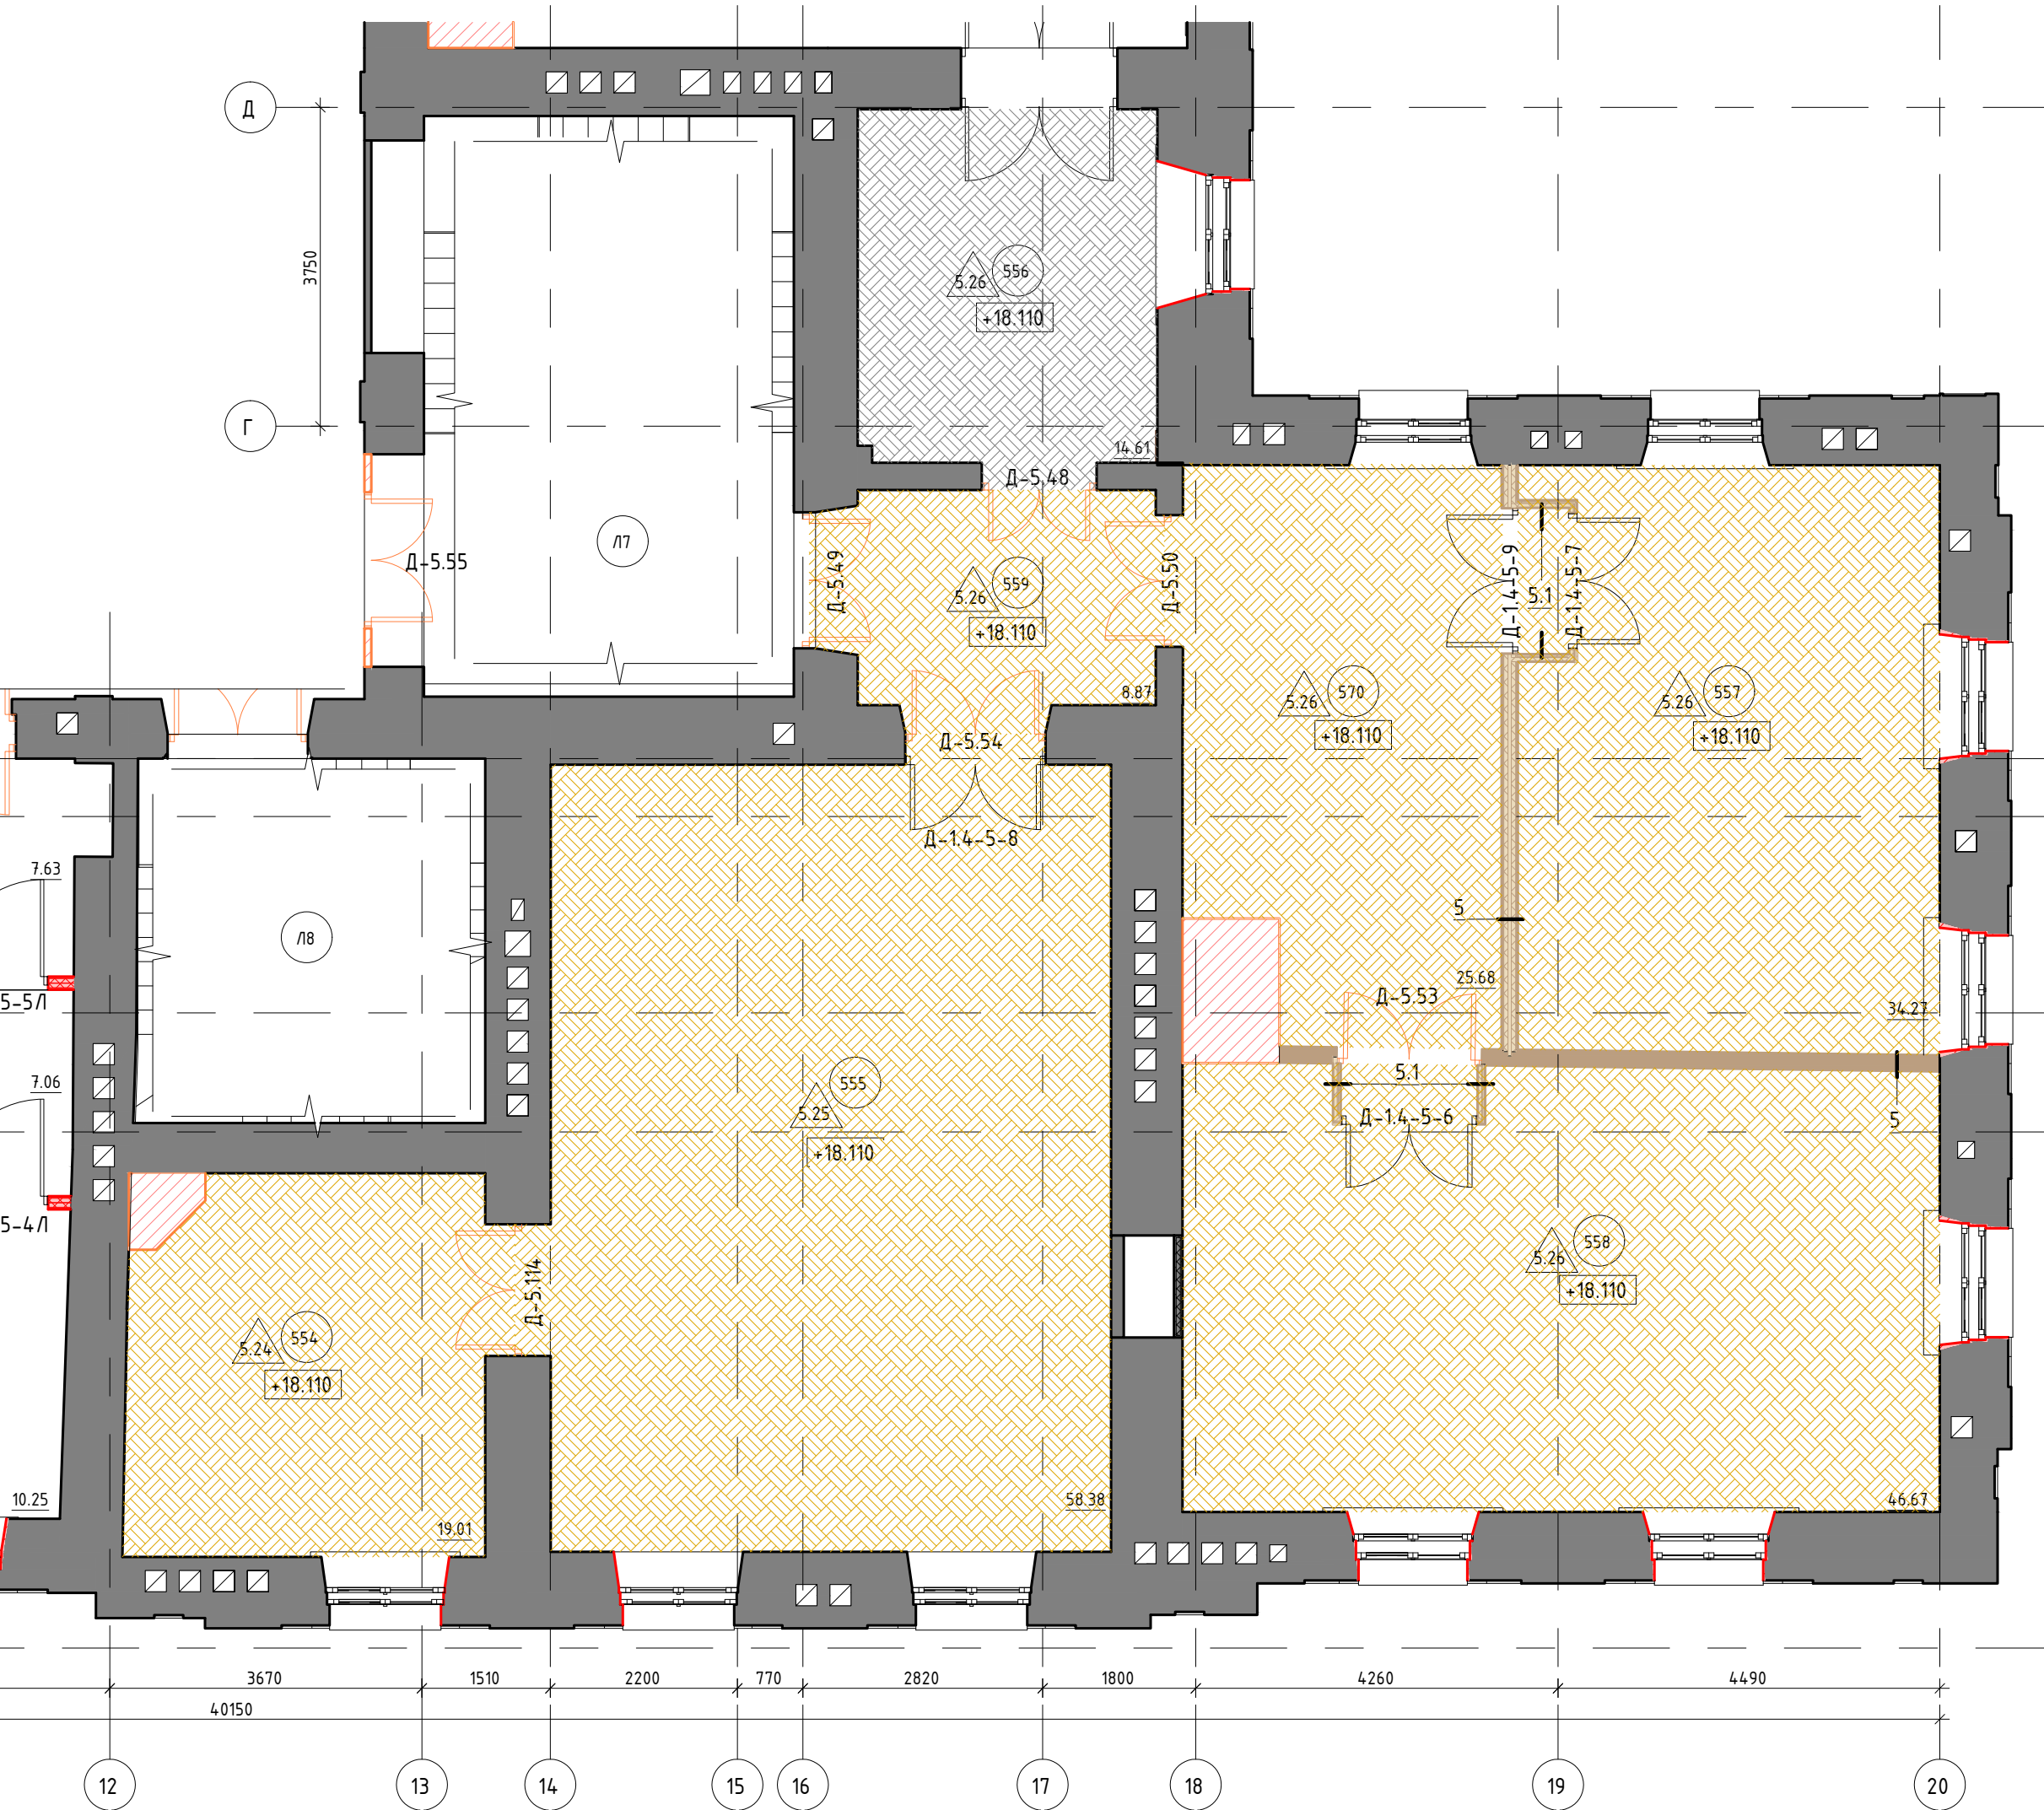

| Экспликация помещений фрагмента в осях 7-20/А-Д 5 этажа |                                            |                 |           |
|---------------------------------------------------------|--------------------------------------------|-----------------|-----------|
| Номер                                                   | Имя                                        | Площадь, кв. м. | Кат. пом. |
| 550                                                     | Репетиторий                                | 70.04           |           |
| 551                                                     | С/У М                                      | 13.95           |           |
| 552                                                     | С/У Ж                                      | 13.95           |           |
| 553                                                     | Зона безопасности МГН                      | 7.06            |           |
| 554                                                     | Кладовая музыкальных инструментов          | 19.01           | ВЗ        |
| 555                                                     | Репетиторий                                | 58.38           |           |
| 556                                                     | Комната настройки музыкальных инструментов | 14.61           |           |
| 557                                                     | Репетиторий                                | 34.27           |           |
| 558                                                     | Репетиторий                                | 46.67           |           |
| 559                                                     | Комната ожидания артистов                  | 8.87            |           |
| 561                                                     | Тамбур-шлюз                                | 5.33            |           |
| 562                                                     | Коридор                                    | 3.94            |           |
| 570                                                     | Гримерная                                  | 25.68           |           |
| 574                                                     | Коридор                                    | 7.63            |           |
| 575                                                     | Коридор                                    | 10.25           |           |
|                                                         |                                            | 339.65          |           |


| Ведомость возводимых перегородок и стен фрагмента в осях 9-20/А-Д 5 этажа |                                       |                |            |
|---------------------------------------------------------------------------|---------------------------------------|----------------|------------|
| Марка                                                                     | Наименование                          | Площадь, кв. м | Примечание |
| 2.2                                                                       | КНАУФ перегородка типа С382           | 18.25          |            |
| 3.1                                                                       | КНАУФ перегородка типа на основе С135 | 22.95          |            |
| 4.2                                                                       | КНАУФ зашивка типа С686               | 23.83          |            |
| 5                                                                         | КНАУФ перегородка типа С366           | 24.74          |            |
| 5.1                                                                       | Перегородка звукоизоляционная 90 мм   | 18.80          |            |
|                                                                           |                                       | 108.57         |            |

| Марка дверного заполнения | Обозначение         |
|---------------------------|---------------------|
| Д-1.4-5-1П                | ГОСТ 475            |
| Д-1.4-5-2П                | ГОСТ 475            |
| Д-1.4-5-3П                | ГОСТ 475            |
| Д-1.4-5-4П                | ГОСТ 2374           |
| Д-1.4-5-5П                | ГОСТ 2374           |
| Д-1.4-5-6                 | ГОСТ 475            |
| Д-1.4-5-7                 | ГОСТ 475            |
| Д-1.4-5-8                 | ГОСТ 475            |
| Д-1.4-5-9                 | ГОСТ 475            |
| Д-1.4-5-10                | ГОСТ 475            |
| Д-1.4-5-11                | ГОСТ 475            |
| Д-5.48                    | См. т. НД-2026-1-ДВ |
| Д-5.49                    | См. т. НД-2026-1-ДВ |
| Д-5.50                    | См. т. НД-2026-1-ДВ |
| Д-5.53                    | См. т. НД-2026-1-ДВ |
| Д-5.54                    | См. т. НД-2026-1-ДВ |
| Д-5.55                    | См. т. НД-2026-1-ДВ |
| Д-5.114                   | См. т. НД-2026-1-ДВ |

Общая экспликация полов фрагмента в осях 9-20/А-Д 5 этажа

| Номера помещений        | Тип пола | Схема пола | Данные элементов пола, мм   | Площадь | Примечание   |
|-------------------------|----------|------------|---|---------|---|
| 555                     | 5.25     |            | 1. Восстанавливаемый паркет на клею под лаком – см. том НД-2026-1-Р-1.4-РР.АИ – 15+3 мм<br>2. Подложка под паркет – фанерные листы ФК водостойкие нешлифованные сорт 3/4, 2 слоя по 15 мм – 30 мм<br>3. Добор – разрезанный дощатый настил 30х200 (шаг 250 мм) – 30 мм<br>Существующая конструкция – см. раздел НД-2026-1-Т01.3:<br>4. Лага 100х50 (шаг 630)<br>5. Балка – бревно 190х200 (шаг 1250) по подкладке из рубероида, с проектной засыпкой керамзитом М350 Ф10-20 – 245-520 мм<br>6. Существующее основание – кирпичный свод | 62.83   | Предусмотреть пропитку деревянных элементов конструкции пола огнебиозащитным составом (см. п VIII лист 1) (захв. 1.4: S=35м²)    |
| 556, 557, 558, 559, 570 | 5.26     |            | 1. Чистовое покрытие – паркет штучный дубовый на клею под лаком – 15+3 мм<br>2. Подложка под паркет – фанерные листы ФК водостойкие нешлифованные сорт 3/4, 2 слоя по 15 мм – 30 мм<br>3. Добор – разрезанный дощатый настил 20х200 (шаг 250 мм) – 20 мм<br>Существующая конструкция – см. раздел НД-2026-1-Т01.3:<br>4. Лага 100х50 (шаг 630)<br>5. Балка – бревно 190х280 (шаг 1380) на керамзите (укрепленном молочком), с проектной засыпкой керамзитом М350 Ф10-20 – 230-370 мм<br>6. Существующее основание – кирпичный свод     | 139.85  | Предусмотреть пропитку деревянных элементов конструкции пола огнебиозащитным составом (см. п VIII лист 1) (захв. 1.4: S=91,83м²) |
| 561                     | 5.29     |            | 1. Чистовое покрытие – паркет штучный дубовый на клею под лаком – 15+3 мм<br>2. Подложка под паркет – фанерные листы ФК водостойкие нешлифованные сорт 3/4, 2 слоя по 15 мм – 30 мм<br>3. Стяжка на цементно-песчаном растворе М200 – 50 мм<br>4. Плита монолитная железобетонная (см. раздел НД-2026-1-Р-1.1-КР) – 200 мм   | 5.81    |   |
|                         |          |            |   | 363.59  |   |
|                         |          |            |   | 363.59  |   |

Рисунок паркета “корзинка”. М 1:15

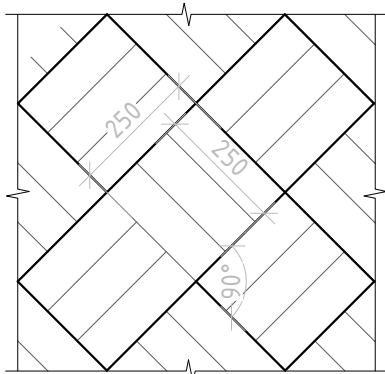

- Паркет “корзинка” в ПО
- Паркет “корзинка” не в ПО
- Паркет “елочка” в ПО
- Паркет “елочка” не в ПО

- Условные обозначения
- 1 - Ось координат
  - +0,000 - Отметка ч...
  - Реставрир...
  - Сохраняем...
  - Пробиваем...
  - Закладываем...