



Рисунок паркета "корзинка". М 1:15

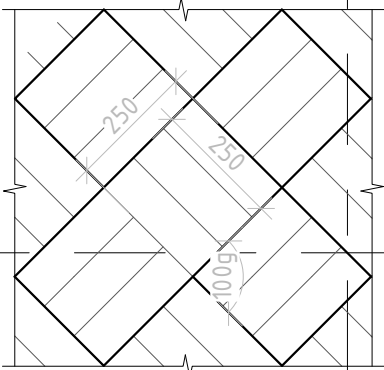

- Паркет "корзинка" в ПО
- Паркет "корзинка" не в ПО

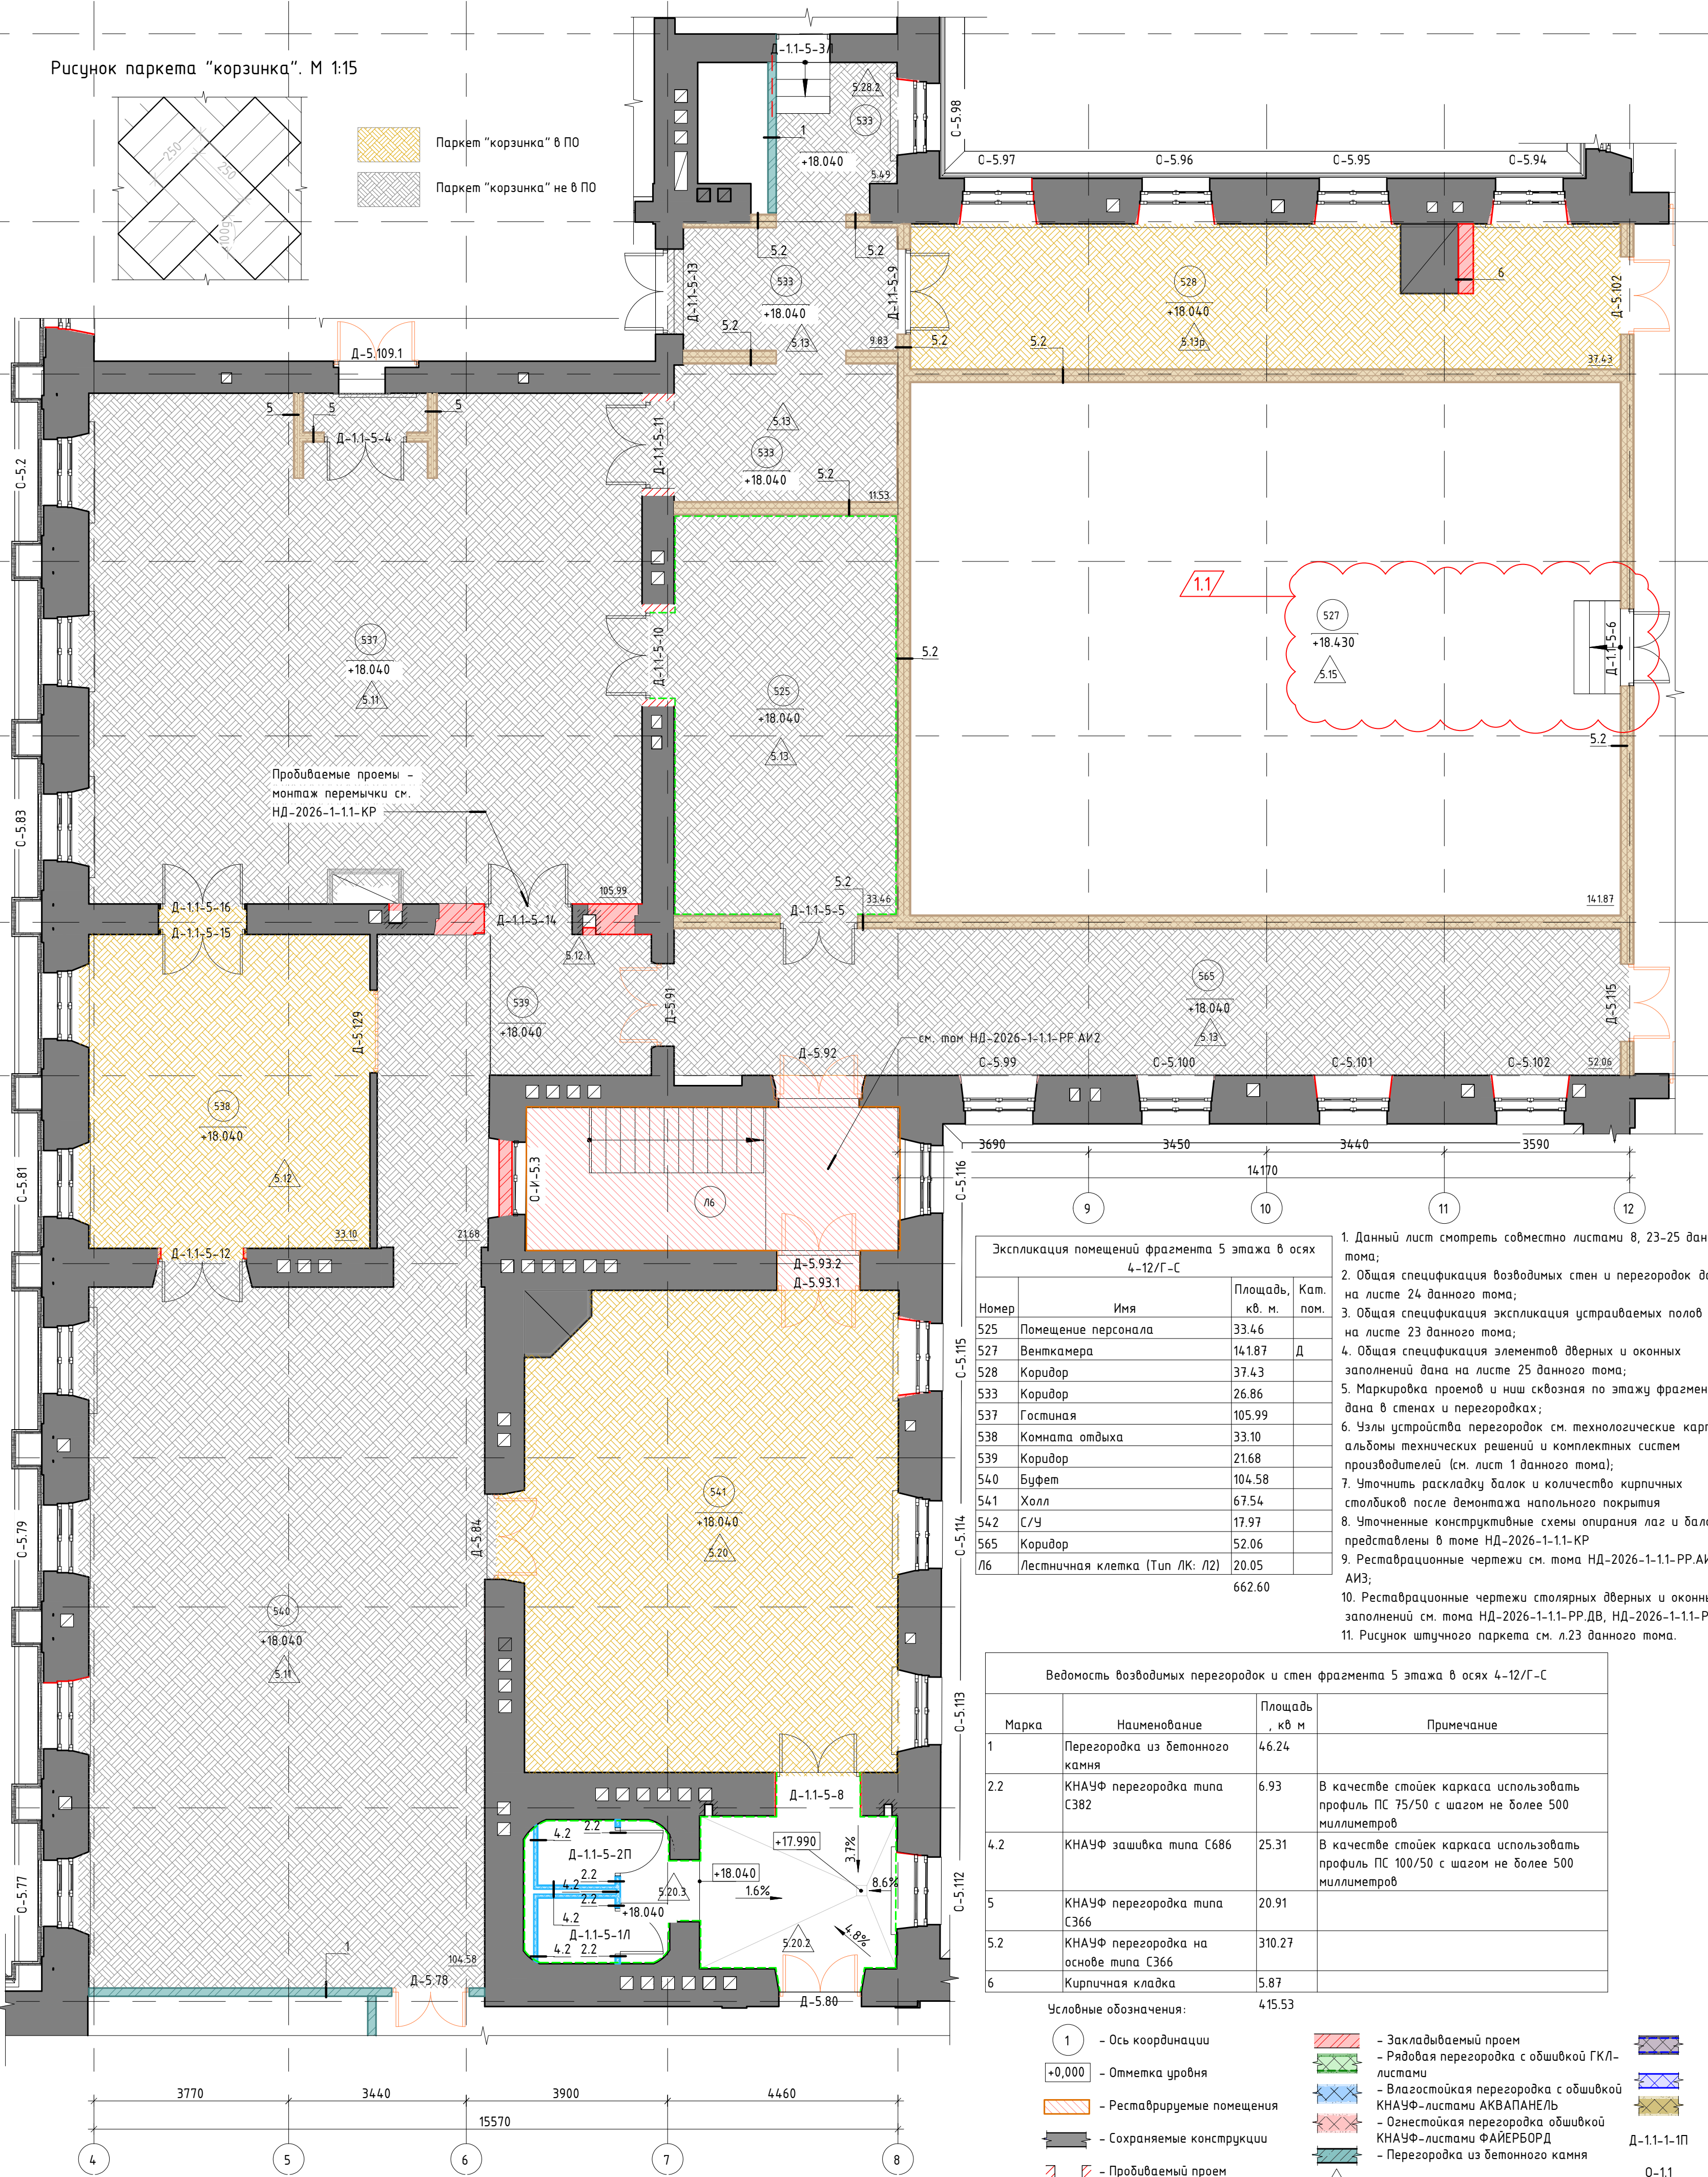

Пробиваемые проемы -
монтаж перемычки см.
НД-2026-1-1.1-КР

Экспликация помещений фрагмента 5 этажа в осях
4-12/Г-С

Номер	Имя	Площадь, кв. м.	Кат. пом.
525	Помещение персонала	33.46	
527	Венткамера	14.187	Д
528	Коридор	37.43	
533	Коридор	26.86	
537	Гостиная	105.99	
538	Комната отдыха	33.10	
539	Коридор	21.68	
540	Буфет	104.58	
541	Холл	67.54	
542	С/У	17.97	
565	Коридор	52.06	
16	Лестничная клетка (Тип ЛК: 1/2)	20.05	
		662.60	

- Данный лист смотреть совместно листами 8, 23-25 данного тома;
- Общая спецификация возводимых стен и перегородок дана на листе 24 данного тома;
- Общая спецификация экспликация устраиваемых полов дана на листе 23 данного тома;
- Общая спецификация элементов дверных и оконных заполнений дана на листе 25 данного тома;
- Маркировка проемов и ниш сквозная по этажу фрагмента, дана в стенах и перегородках;
- Узлы устройства перегородок см. технологические карты, альбомы технических решений и комплектных систем производителей (см. лист 1 данного тома);
- Уточнить раскладку балок и количество кирпичных столбиков после демонтажа напольного покрытия
- Уточненные конструктивные схемы опирания лаг и балок представлены в томе НД-2026-1-1.1-КР
- Реставрационные чертежи см. тома НД-2026-1-1.1-РР.АИ1-АИ3;
- Реставрационные чертежи столярных дверных и оконных заполнений см. тома НД-2026-1-1.1-РР.ДВ, НД-2026-1-1.1-РР.ОК;
- Рисунок штучного паркета см. л.23 данного тома.

Ведомость возводимых перегородок и стен фрагмента 5 этажа в осях 4-12/Г-С

Марка	Наименование	Площадь, кв. м	Примечание
1	Перегорodka из бетонного камня	46.24	
2.2	КНАУФ перегородка типа С382	6.93	В качестве стоек каркаса использовать профиль ПС 75/50 с шагом не более 500 миллиметров
4.2	КНАУФ зашивка типа С686	25.31	В качестве стоек каркаса использовать профиль ПС 100/50 с шагом не более 500 миллиметров
5	КНАУФ перегородка типа С366	20.91	
5.2	КНАУФ перегородка на основе типа С366	310.27	
6	Кирпичная кладка	5.87	

Условные обозначения:

- 1 - Ось координации
- +0,000 - Отметка уровня
- Реставрируемые помещения
- Сохраняемые конструкции
- Пробиваемый проем

- Закладываемый проем
- Рядовая перегородка с обшивкой ГКЛ-листами
- Влазостойкая перегородка с обшивкой КНАУФ-листами АКВАПАНЕЛЬ
- Огнестойкая перегородка обшивкой КНАУФ-листами ФАЙЕРБОРД
- Перегорodka из бетонного камня
- 1.1 - Марка пола

- Д-1.1-1-1П
- О-1.1