


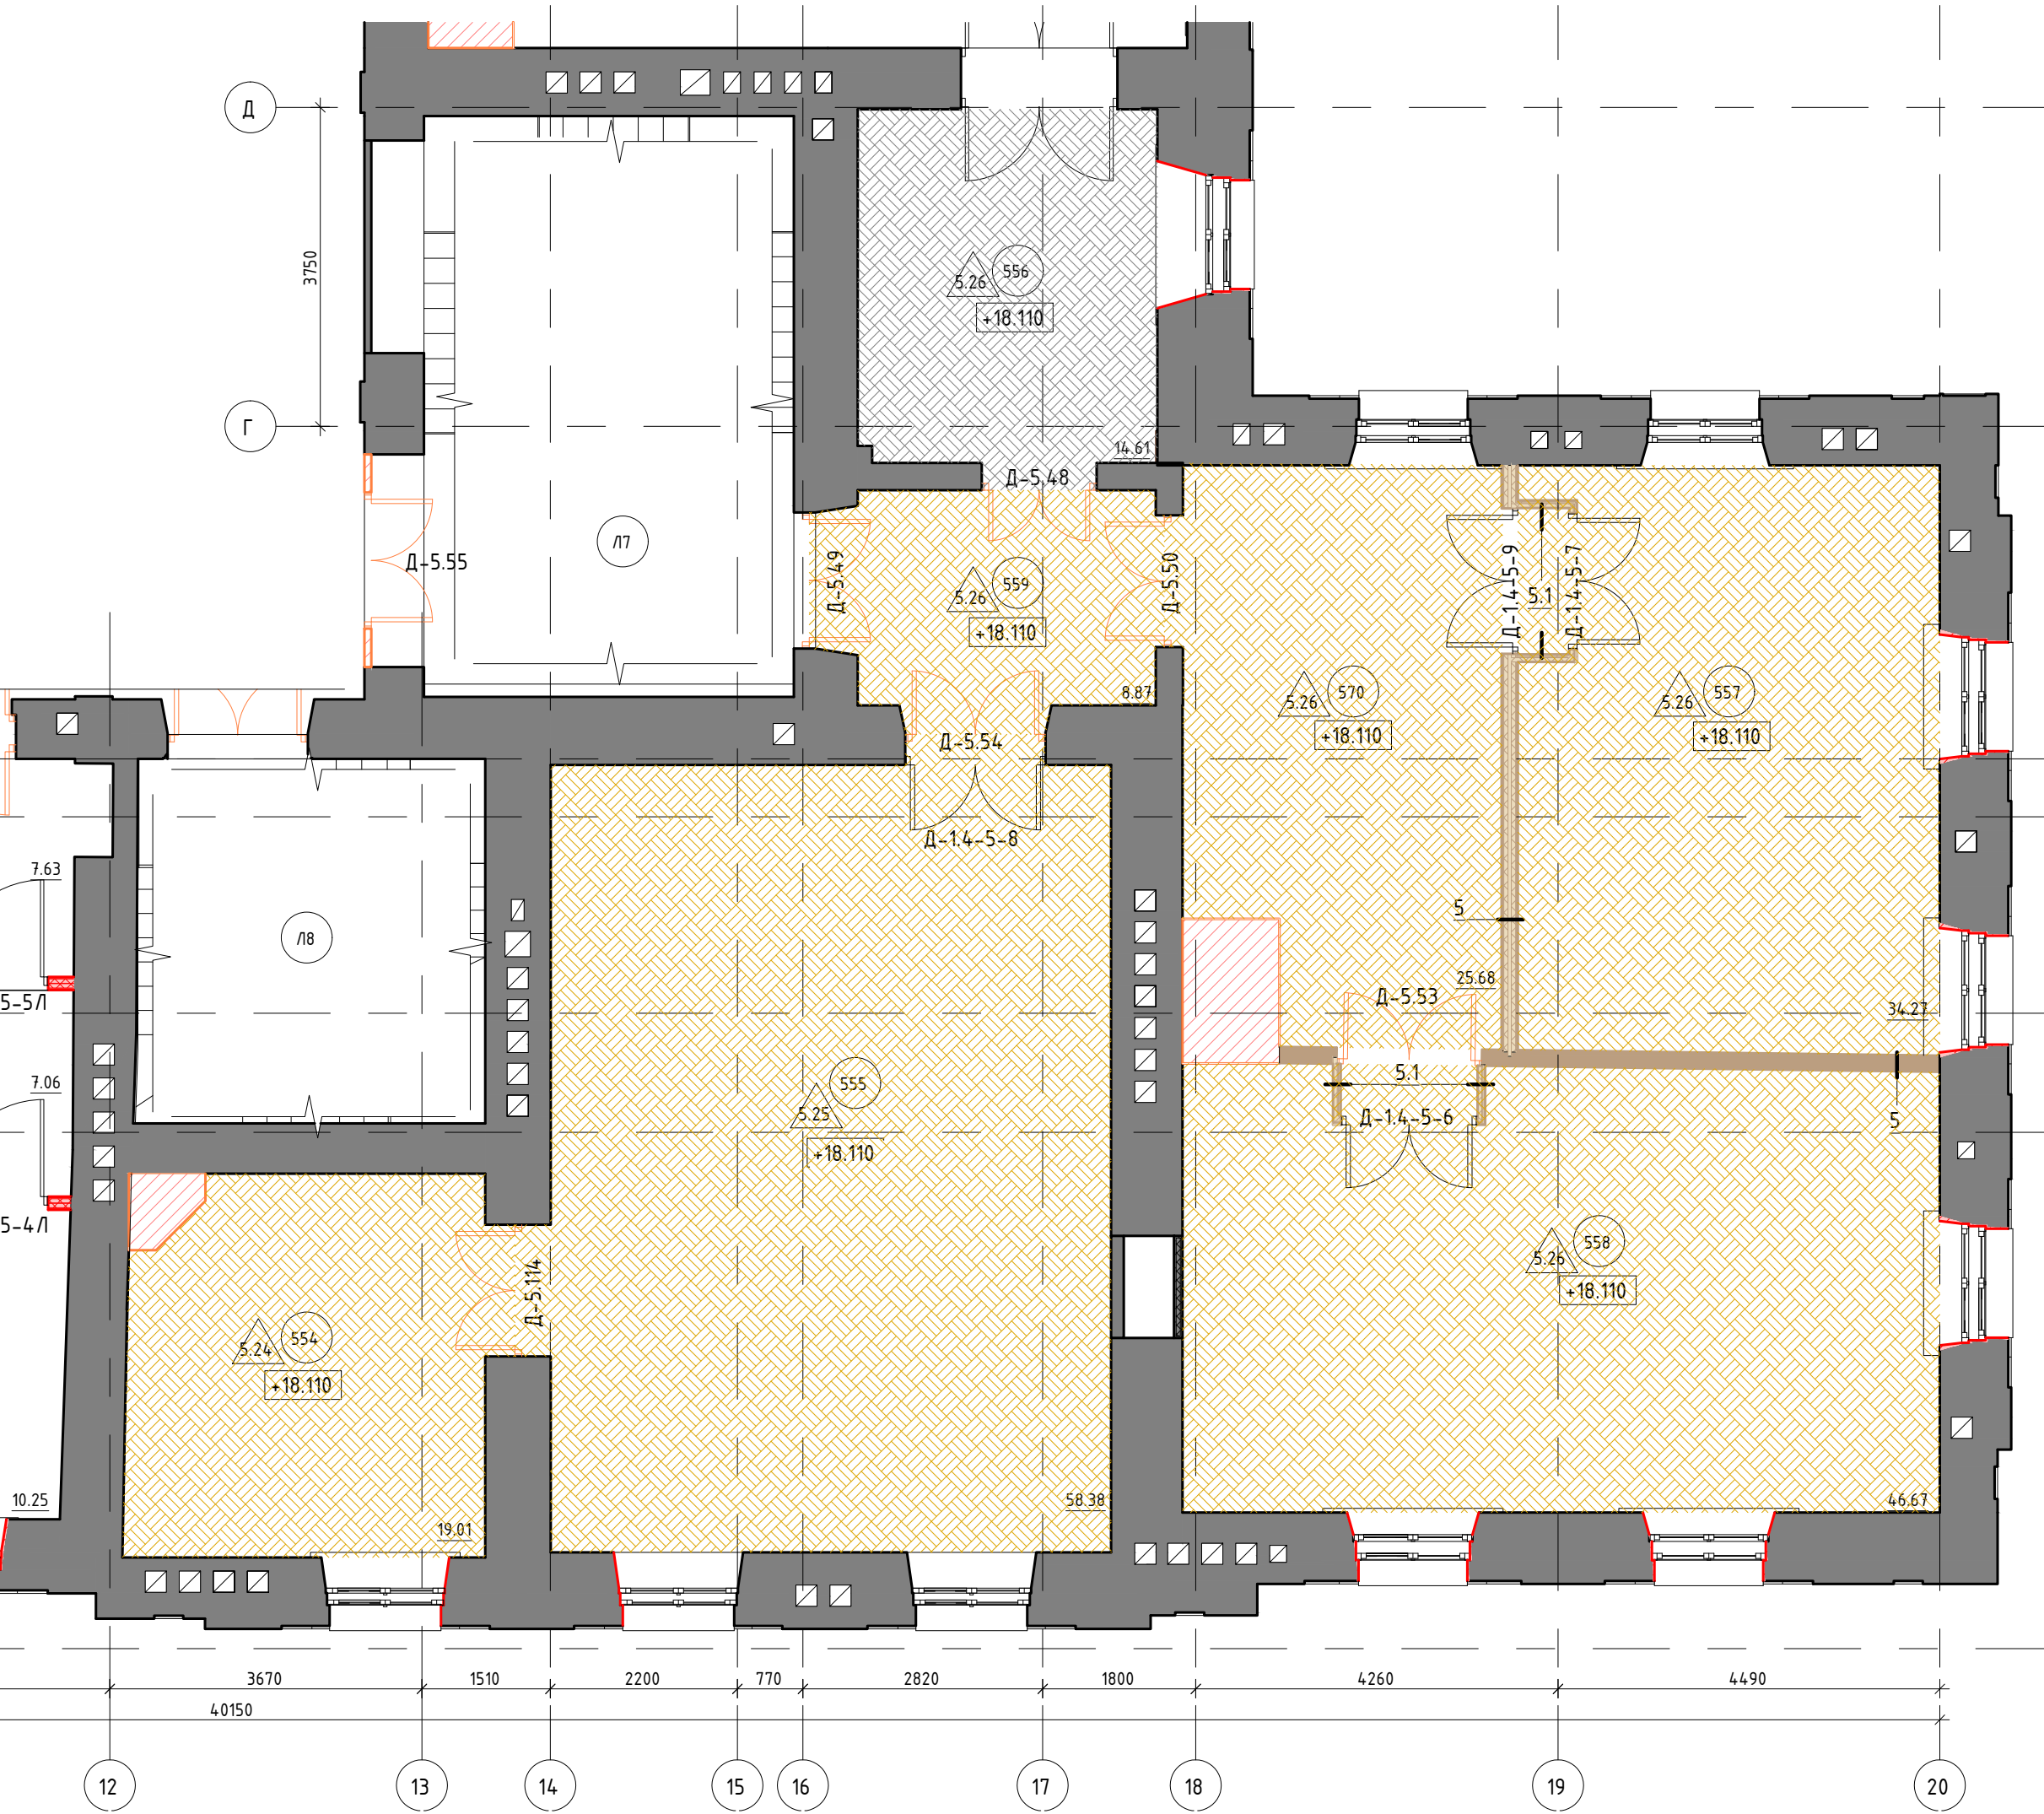

Экспликация помещений фрагмента в осях 7-20/А-Д 5 этажа			
Номер	Имя	Площадь, кв. м.	Кат. пом.
550	Репетиторий	70.04	
551	С/У М	13.95	
552	С/У Ж	13.95	
553	Зона безопасности МГН	7.06	
554	Кладовая музыкальных инструментов	19.01	ВЗ
555	Репетиторий	58.38	
556	Комната настройки музыкальных инструментов	14.61	
557	Репетиторий	34.27	
558	Репетиторий	46.67	
559	Комната ожидания артистов	8.87	
561	Тамбур-шлюз	5.33	
562	Коридор	3.94	
570	Гримерная	25.68	
574	Коридор	7.63	
575	Коридор	10.25	
		339.65	


Ведомость возводимых перегородок и стен фрагмента в осях 9-20/А-Д 5 этажа			
Марка	Наименование	Площадь, кв. м	Примечание
2.2	КНАУФ перегородка типа С382	18.25	
3.1	КНАУФ перегородка типа на основе С135	22.95	
4.2	КНАУФ зашивка типа С686	23.83	
5	КНАУФ перегородка типа С366	24.74	
5.1	Перегородка звукоизоляционная 90 мм	18.80	
		108.57	

Марка дверного заполнения	Обозначение
Д-1.4-5-1П	ГОСТ 475
Д-1.4-5-2П	ГОСТ 475
Д-1.4-5-3П	ГОСТ 475
Д-1.4-5-4П	ГОСТ 2374
Д-1.4-5-5П	ГОСТ 2374
Д-1.4-5-6	ГОСТ 475
Д-1.4-5-7	ГОСТ 475
Д-1.4-5-8	ГОСТ 475
Д-1.4-5-9	ГОСТ 475
Д-1.4-5-10	ГОСТ 475
Д-1.4-5-11	ГОСТ 475
Д-5.48	См. т. НД-2026-1-ДВ
Д-5.49	См. т. НД-2026-1-ДВ
Д-5.50	См. т. НД-2026-1-ДВ
Д-5.53	См. т. НД-2026-1-ДВ
Д-5.54	См. т. НД-2026-1-ДВ
Д-5.55	См. т. НД-2026-1-ДВ
Д-5.114	См. т. НД-2026-1-ДВ

Общая экспликация полов фрагмента в осях 9-20/А-Д 5 этажа

Номера помещений	Тип пола	Схема пола	Данные элементов пола, мм	Площадь	Примечание
555	5.25		1. Восстанавливаемый паркет на клею под лаком – см. том НД-2026-1-Р-1.4-РР.АИ – 15+3 мм 2. Подложка под паркет – фанерные листы ФК водостойкие нешлифованные сорт 3/4, 2 слоя по 15 мм – 30 мм 3. Добор – разрезанный дощатый настил 30х200 (шаг 250 мм) – 30 мм Существующая конструкция – см. раздел НД-2026-1-Т01.3: 4. Лага 100х50 (шаг 630) 5. Балка – бревно 190х200 (шаг 1250) по подкладке из рубероида, с проектной засыпкой керамзитом М350 Ф10-20 – 245-520 мм 6. Существующее основание – кирпичный свод	62.83	Предусмотреть пропитку деревянных элементов конструкции пола огнебиозащитным составом (см. п VIII лист 1) (захв. 1.4: S=35м²)
556, 557, 558, 559, 570	5.26		1. Чистовое покрытие – паркет штучный дубовый на клею под лаком – 15+3 мм 2. Подложка под паркет – фанерные листы ФК водостойкие нешлифованные сорт 3/4, 2 слоя по 15 мм – 30 мм 3. Добор – разрезанный дощатый настил 20х200 (шаг 250 мм) – 20 мм Существующая конструкция – см. раздел НД-2026-1-Т01.3: 4. Лага 100х50 (шаг 630) 5. Балка – бревно 190х280 (шаг 1380) на керамзите (укрепленном молочком), с проектной засыпкой керамзитом М350 Ф10-20 – 230-370 мм 6. Существующее основание – кирпичный свод	139.85	Предусмотреть пропитку деревянных элементов конструкции пола огнебиозащитным составом (см. п VIII лист 1) (захв. 1.4: S=91,83м²)
561	5.29		1. Чистовое покрытие – паркет штучный дубовый на клею под лаком – 15+3 мм 2. Подложка под паркет – фанерные листы ФК водостойкие нешлифованные сорт 3/4, 2 слоя по 15 мм – 30 мм 3. Стяжка на цементно-песчаном растворе М200 – 50 мм 4. Плита монолитная железобетонная (см. раздел НД-2026-1-Р-1.1-КР) – 200 мм	5.81	
				363.59	
				363.59	

Рисунок паркета “корзинка”. М 1:15

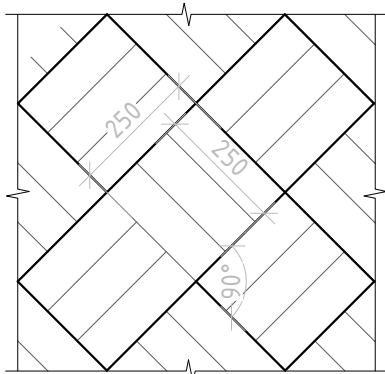

- Паркет “корзинка” в ПО
- Паркет “корзинка” не в ПО
- Паркет “елочка” в ПО
- Паркет “елочка” не в ПО

- Условные обозначения
- 1 – Ось координат
 - +0,000 – Отметка ч...
 - Реставрир...
 - Сохраняем...
 - Пробиваем...
 - Закладываем...