




Маркировочный план фрагмента 5 этажа в осях 4–7/П–З

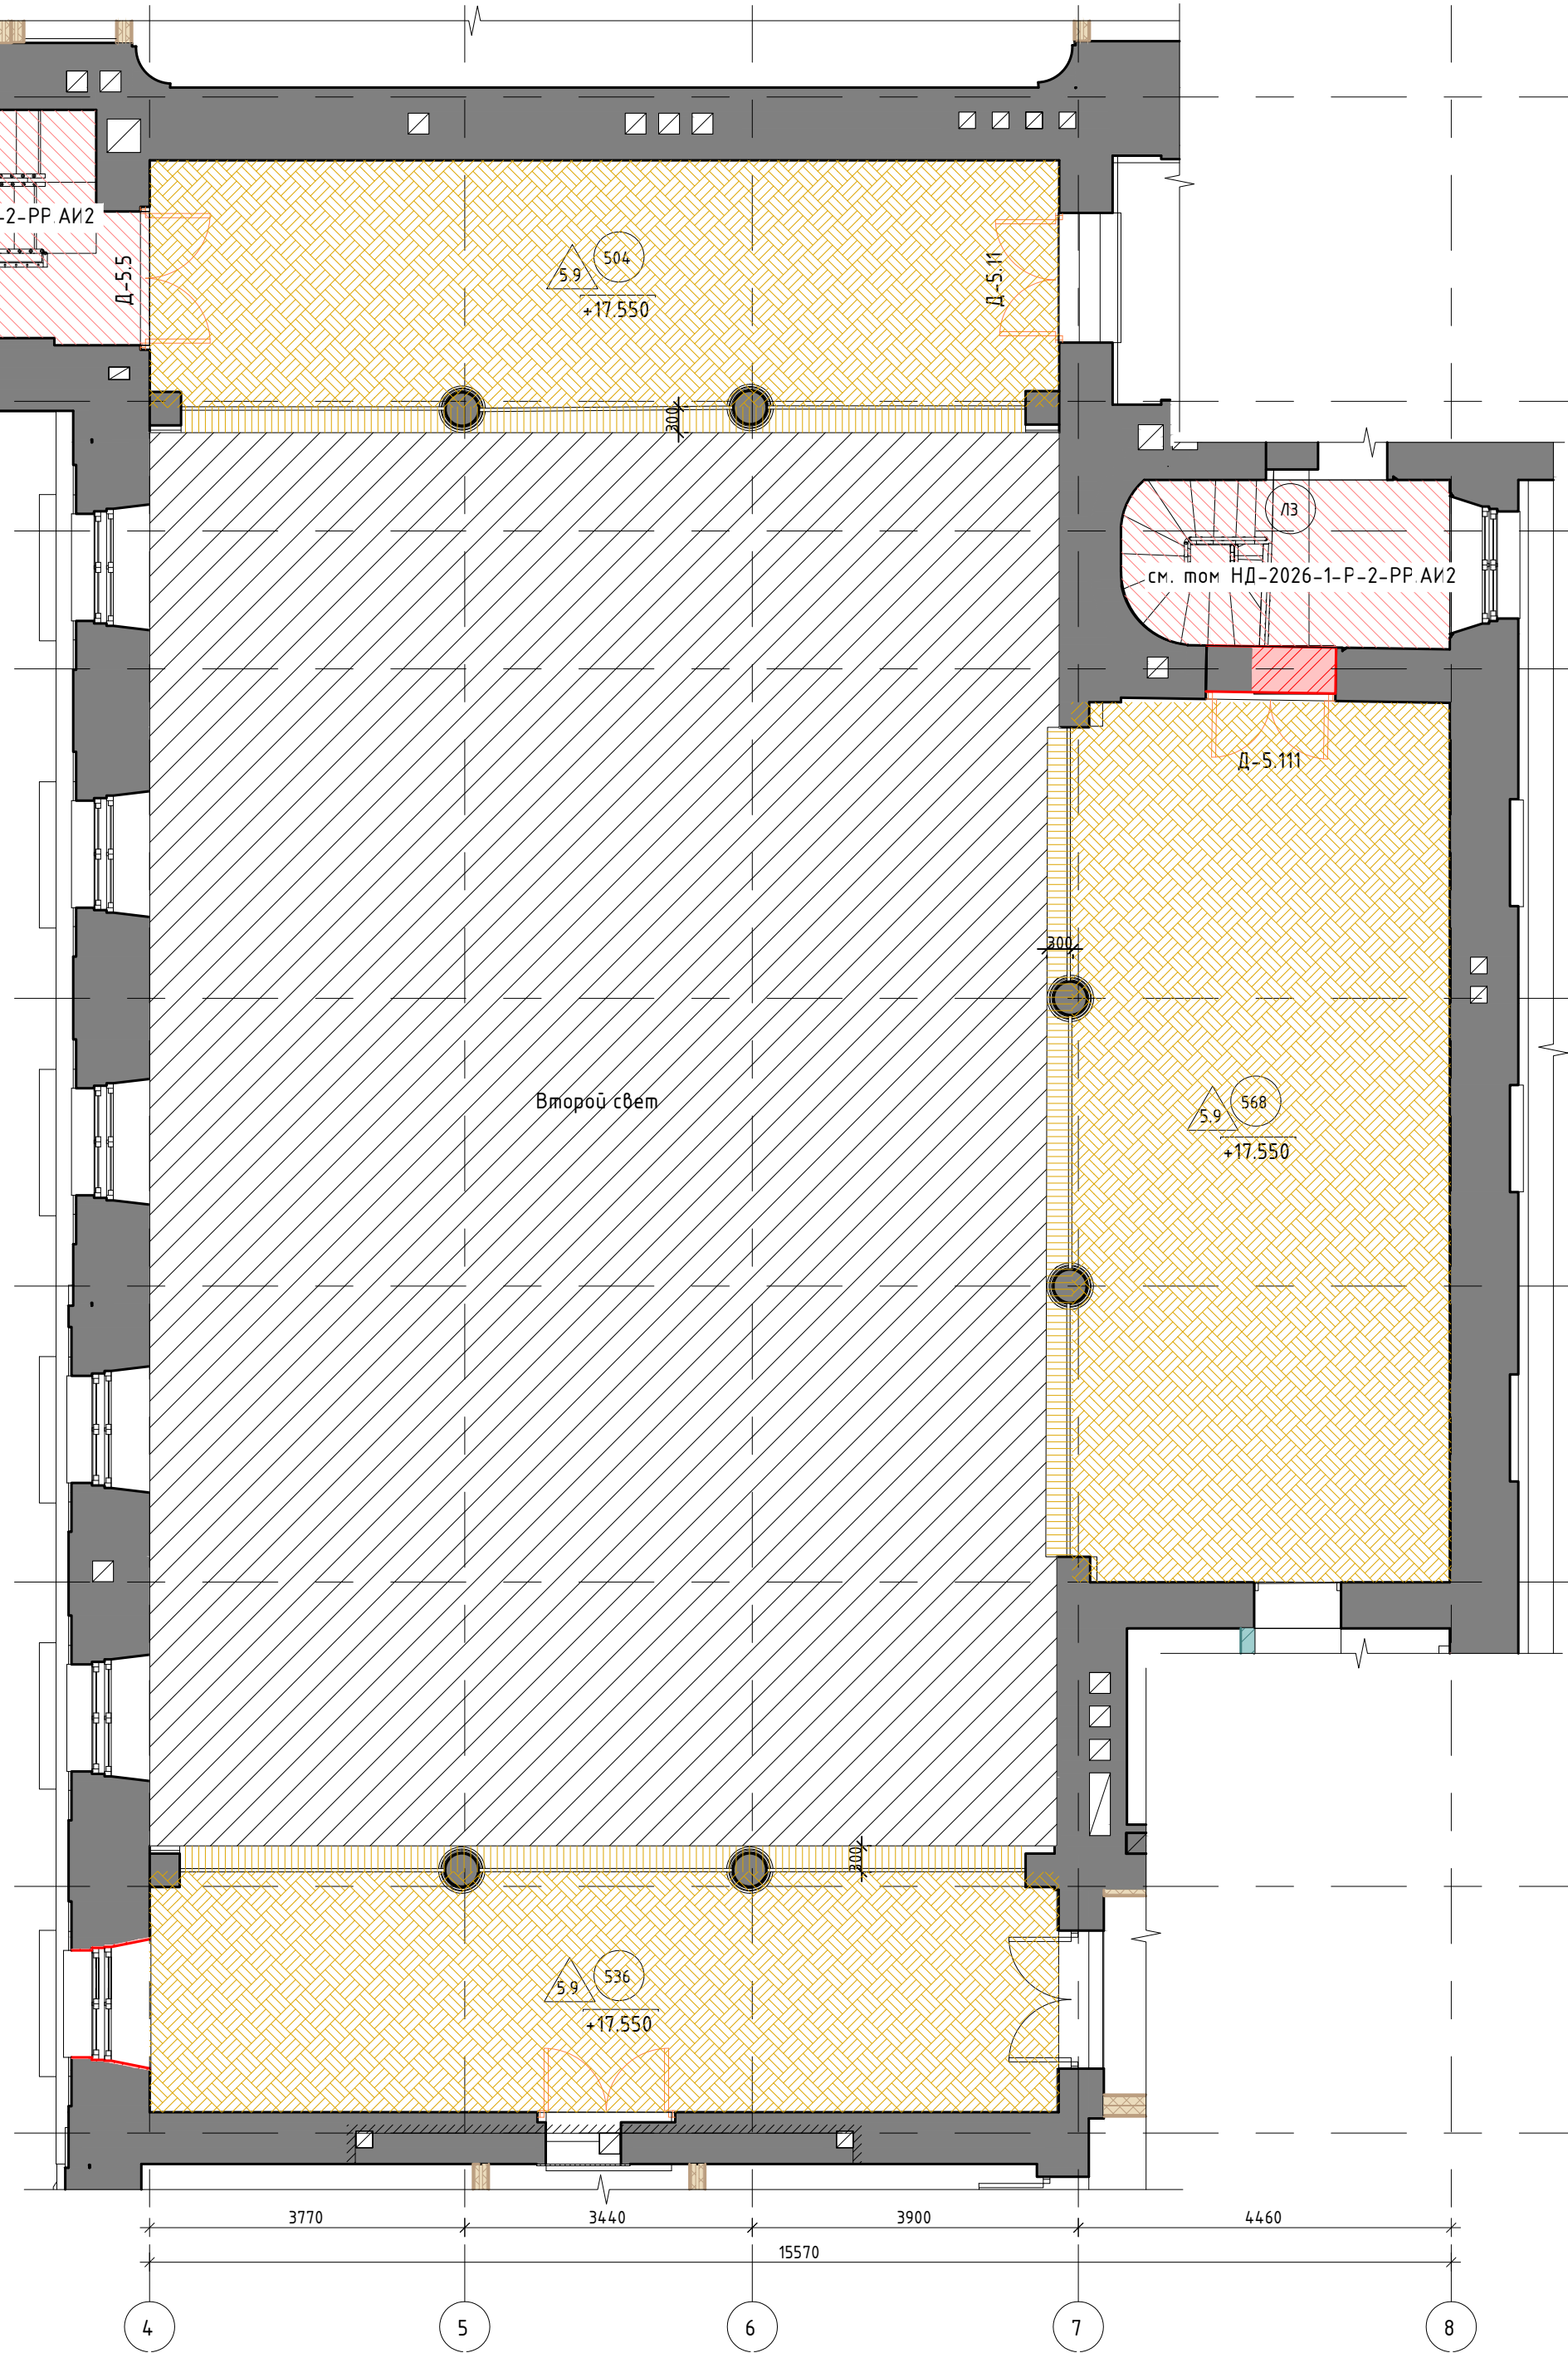


Маркировочный план фрагмента 5 этажа в осях 13-20/У–Ю

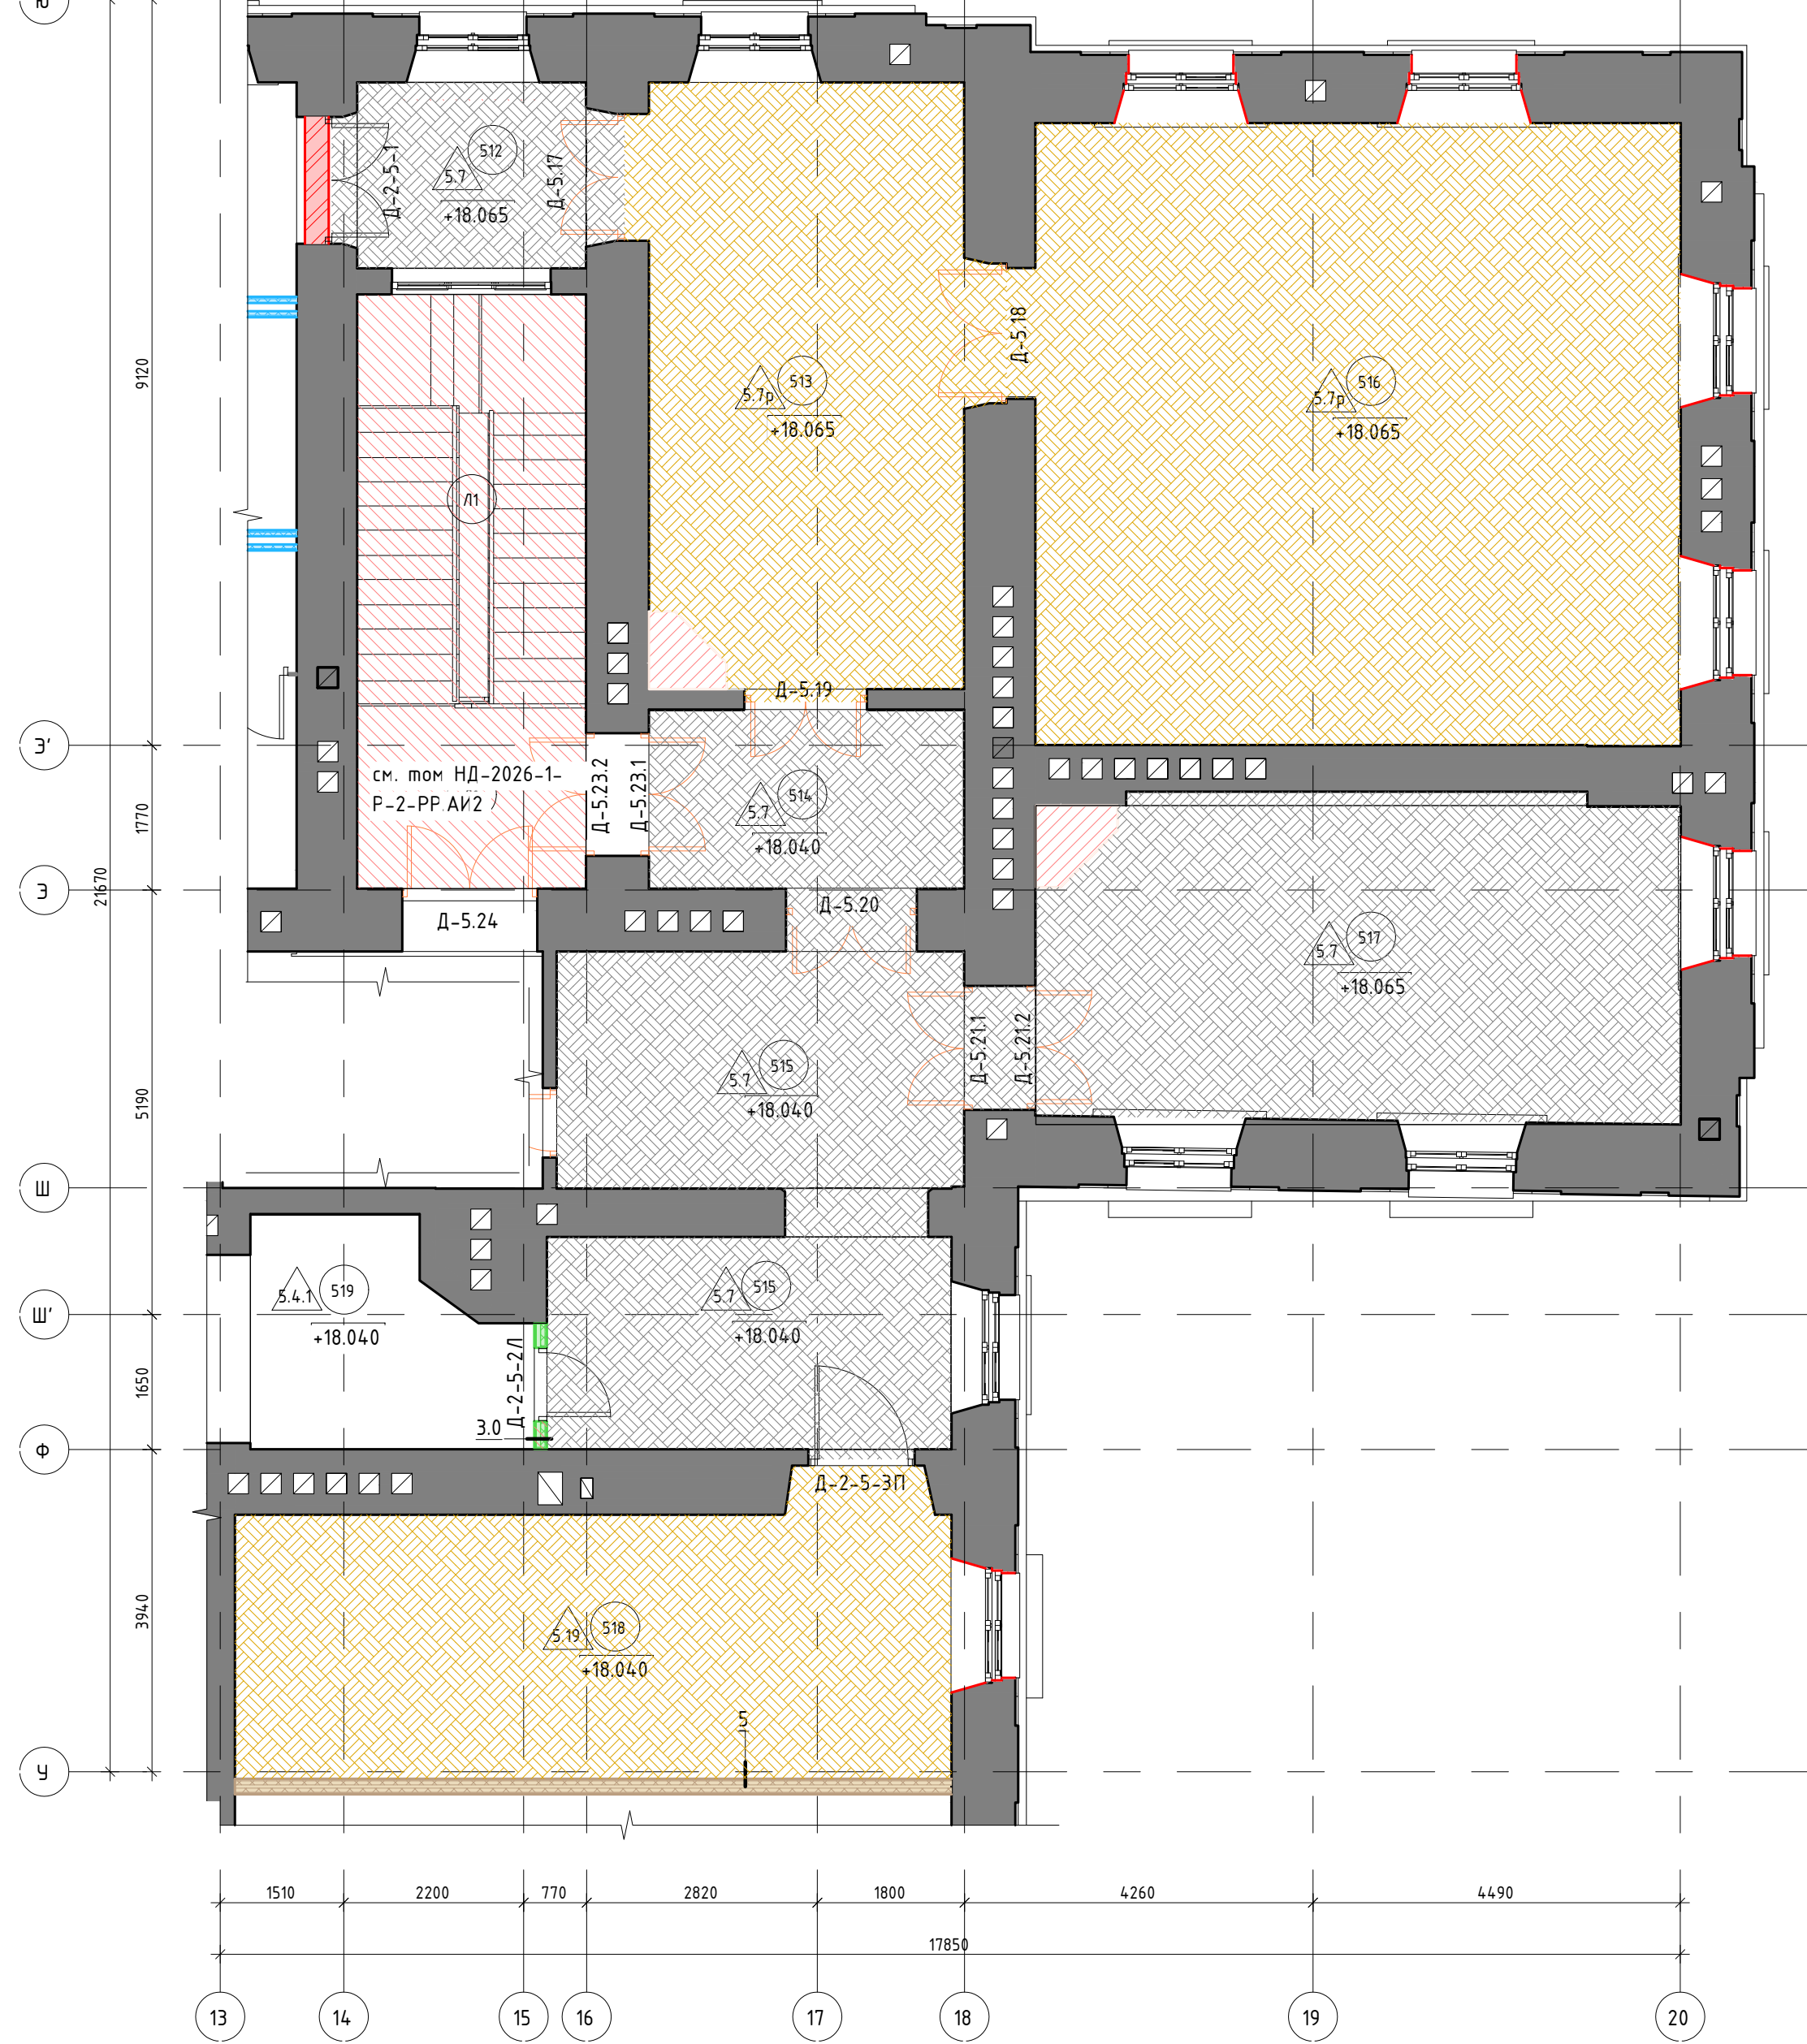

Маркировочный план фрагмента 5 этажа в осях 12-16/Б–Д

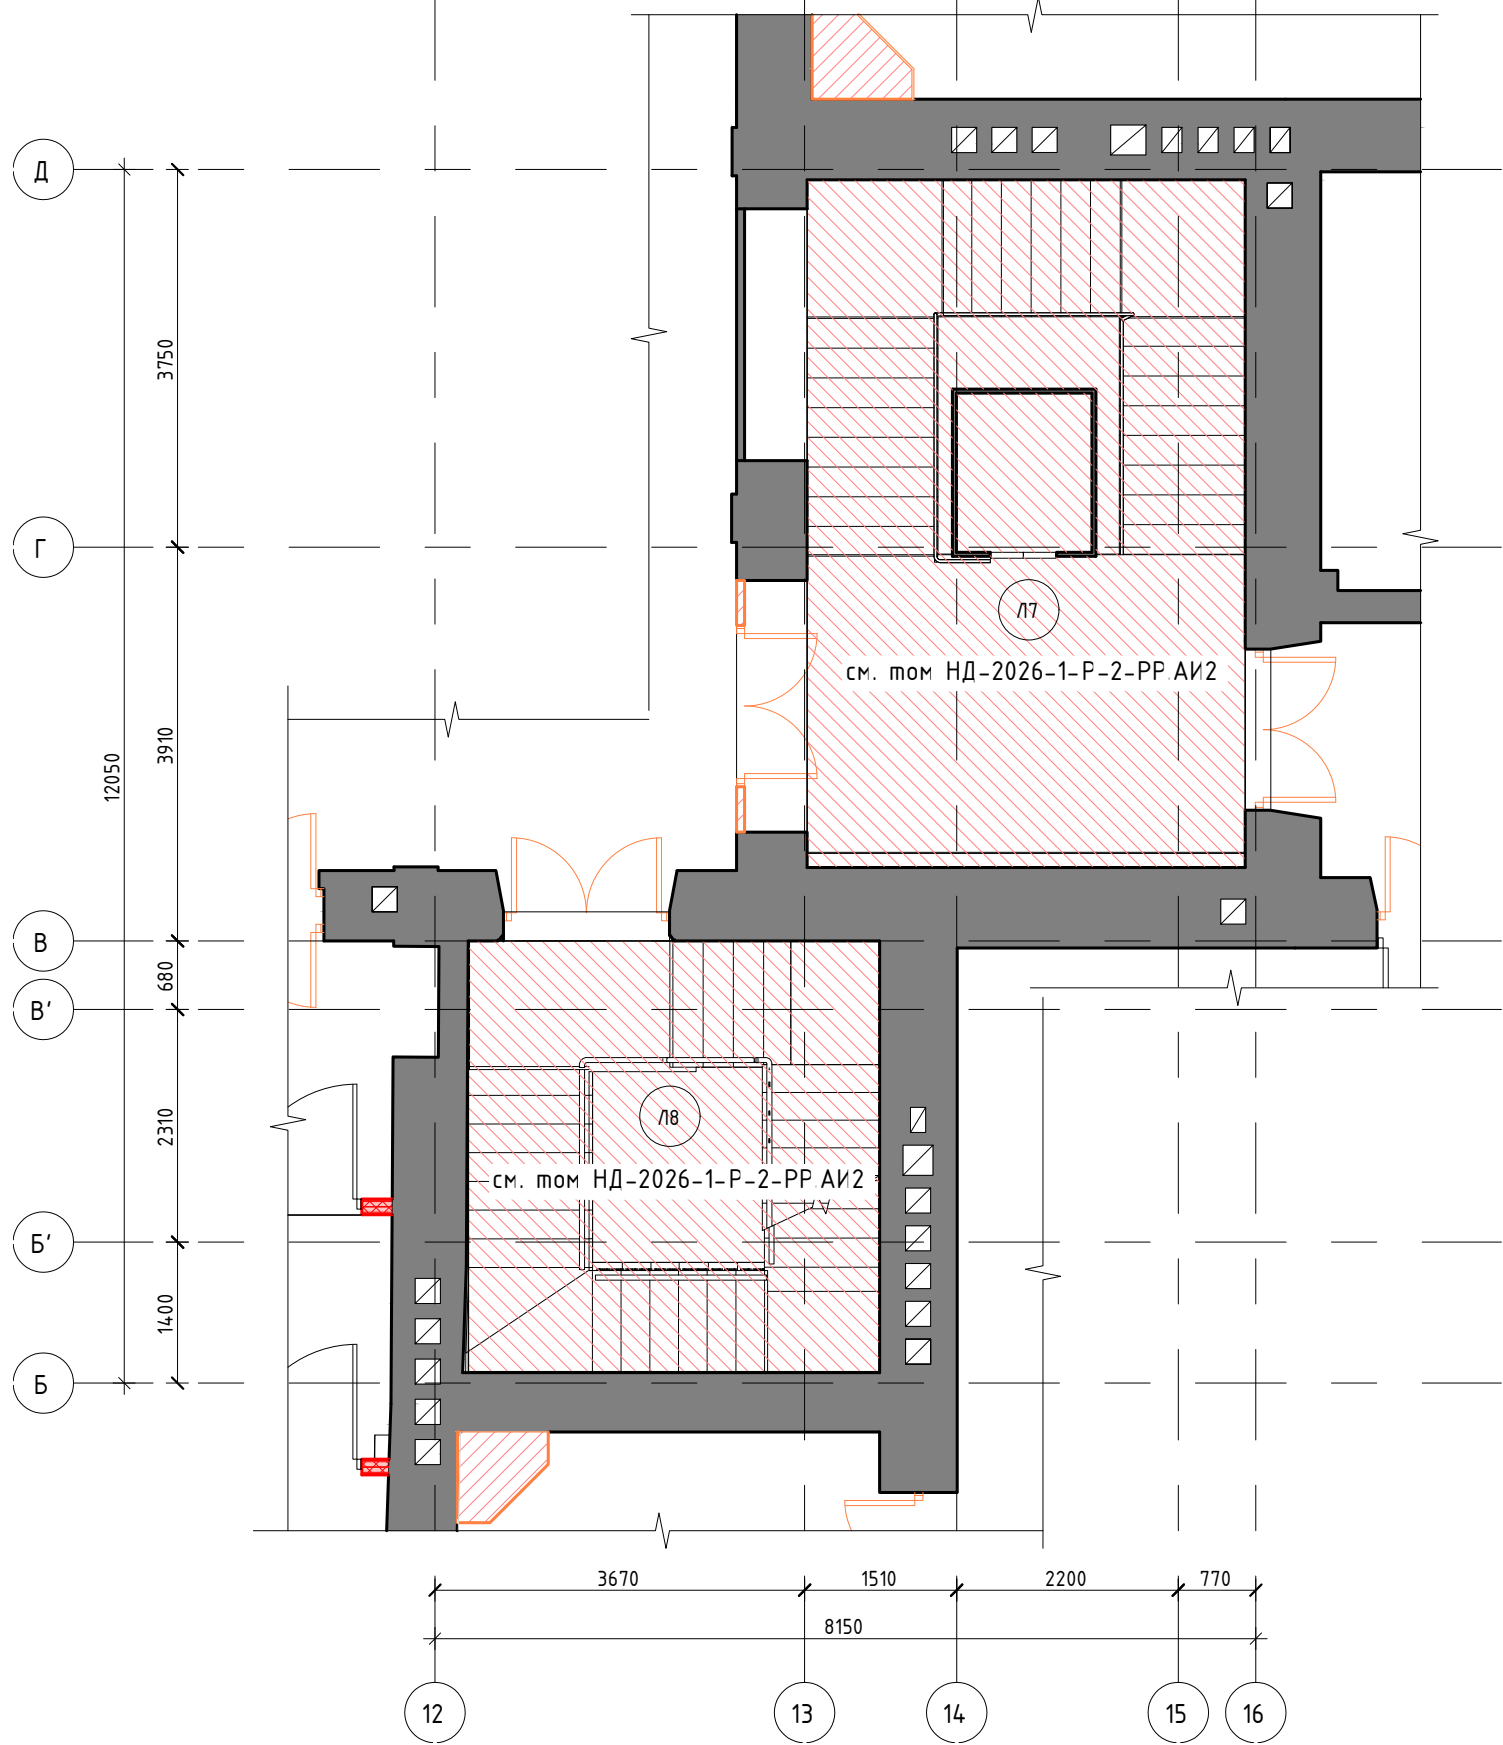

Маркировочный план фрагмента 5 этажа в осях 14–18/Р–С

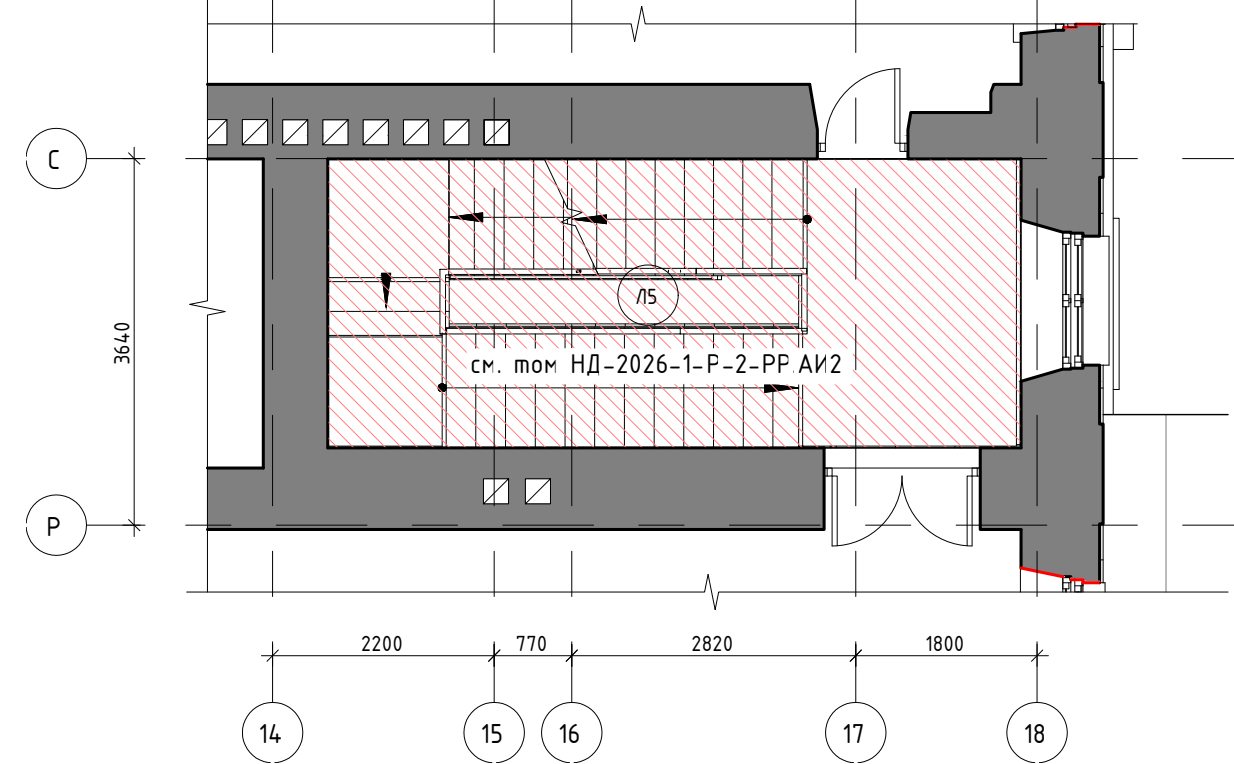


514	Коридор	8.43
515	Коридор	27.15
516	Репетиторий	60.03
517	Комната отдыха	31.30
518	Комната отдыха	28.29
519	С/У	8.30
536	Ложа VIP	34.31
568	Ложа VIP	49.19
Л1	Лестничная клетка (Тип ЛК: Л2)	20.32
Л2	Коридор	10.27
Л3	Технологическая лестница	7.71
Л5	Лестничная клетка (Тип ЛК: Л2)	19.75
Л7	Технологическая лестница	27.33
Л8	Лестничная клетка (Тип ЛК: Н2)	17.57
		419.94

Ведомость возводимых перегородок и стен фрагментов 5 этажа в осях 4-8/П-З, 13-20/У-Ю, 12-16/Б-Д,...			
Марка	Наименование	Площадь, кв. м.	Примечание
3.0	КНАУФ перегородка типа С115	5.27	
		5.27	

Спецификация элементов заполнения дверных проемов фрагментов 5 этажа в осях 4-8/П-З, 13-20/У-Ю, 12-16/Б-Д, 14-18/Р-С											
Наименование	Габариты проем по полотну		Кол-во	Примечание			Основание установки	Марка проема	Габариты монтажного проема		Примечание
	Высота, мм	Ширина, мм		Озн.-ст	Р. 05	Характеристика			Ширина, мм	Высота, мм	
ДМ 2Р 29х13 Г Пр	2970	1390	1	-		Тип открывания, количество створок: распашное, 2 створки; Тип дверного блока: открытый деревянный с наличниками; Типы доводчика, петель, порога, ограничителя: без доводчика, со встроенным порогом, ограничитель напольный; Тип ручки: нажимная с планкой без замка;	Существующая стена	П-2-5-11	1490	3020	-
ДС 1РЛ 21х9 Пр0 МЗ3	1990	780	1	-		Тип открывания, количество створок: распашное левое, 1 створка; Тип дверного блока: скрытый деревянный; Типы доводчика, петель, порога, ограничителя: без доводчика, скрытые петли, выпадающий порог, без ограничителя; Тип ручки: нажимная с заверткой; Тип уплотнителя: отсутствует; СКУД: отсутствует	ГКЛ	П-2-5-1	880	2040	-
ДМ 1Рл 21х11 Г Пр	2120	1140	1	-		Тип открывания, количество створок: распашное правое, 1 створка; Тип дверного блока: открытый деревянный с наличниками; Типы доводчика, петель, порога, ограничителя: без доводчика, скрытые петли, со встроенным порогом, без ограничителя; Тип ручки: нажимная с планкой без замка; Тип уплотнителя: отсутствует; СКУД: отсутствует	Существующая стена	П-2-5-2	1240	2170	-
См. том НД-2026-1-2-Р-ДВ	2940	1550	1	Е130		Тип дверного блока: Учтено в томе НД-2026-1-2-РР-ДВ;	Существующая стена	П-2-5-9	1650	2990	Дверь в ПО
См. том НД-2026-1-2-Р-ДВ	3320	1390	1	Е130		Тип дверного блока: Учтено в томе НД-2026-1-2-РР-ДВ;	Существующая стена	П-2-5-13	1490	3370	Дверь в ПО

Спецификация элементов заполнения дверных проемов фрагментов 5 этажа в осях 4–8/П–З, 13–20/У–Ю, 12–16/Б–Д, 14–18/Р–С													
Марка дверного заполнения	Обозначение	Наименование	Габариты проем по полотну		Кол-во	Примечание			Основание установки	Марка проема	Габариты монтажного проема		
			Высота, мм	Ширина, мм		Озн.-ст	R. 05	Характеристика			Ширина, мм	Высота, мм	Примечание
Д-5.17	См. том НД-2026-1-2-РР-Д В	См. том НД-2026-1-2-Р Р.ДВ	2970	1390	1	-		Тип дверного блока: Учтено в томе НД-2026-1-2-РР-ДВ;	Существующая стена	П-2-5-10	1490	3020	Дверь в ПО
Д-5.18	См. том НД-2026-1-2-РР-Д В	См. том НД-2026-1-2-Р Р.ДВ	2940	1550	1	-		Тип дверного блока: Учтено в томе НД-2026-1-2-РР-ДВ;	Существующая стена	П-2-5-8	1650	2990	Дверь в ПО
Д-5.19	См. том НД-2026-1-2-РР-Д В	См. том НД-2026-1-2-Р Р.ДВ	2920	1340	1	-		Тип дверного блока: Учтено в томе НД-2026-1-2-РР-ДВ;	Существующая стена	П-2-5-4	1440	2970	Дверь в ПО
Д-5.20	См. том НД-2026-1-2-РР-Д В	См. том НД-2026-1-2-Р Р.ДВ	2920	1440	1	-		Тип дверного блока: Учтено в томе НД-2026-1-2-РР-ДВ;	Существующая стена	П-2-5-7	1540	2970	Дверь в ПО
Д-5.21.1	См. том НД-2026-1-2-РР-Д В	См. том НД-2026-1-2-Р Р.ДВ	2890	1380	1	-		Тип дверного блока: Учтено в томе НД-2026-1-2-РР-ДВ;	Существующая стена	П-2-5-5	1480	2940	Дверь в ПО
Д-5.21.2	См. том НД-2026-1-2-РР-Д В	См. том НД-2026-1-2-Р Р.ДВ	2890	1380	1	-		Тип дверного блока: Учтено в томе НД-2026-1-2-РР-ДВ;	Существующая стена	П-2-5-5	1480	2940	Дверь в ПО
Д-5.23.1	См. том НД-2026-1-2-РР-Д В	См. том НД-2026-1-2-Р Р.ДВ	2890	1380	1	-		Тип дверного блока: Учтено в томе НД-2026-1-2-РР-ДВ;	Существующая стена	П-2-5-6	1480	2940	Дверь в ПО

Рисунок паркета “корзинка”. М 1:15

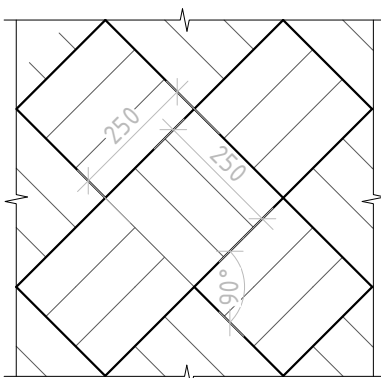

- Условные обозначения:
- 1 - Ось координации
 - +0,000 - Отметка уровня
 - Реставрируемые помещения
 - Сохраняемые конструкции
 - Пробиваемый проем
 - Закладываемый проем
 - Рядовая перегородка
 - ГКЛ-листаны
 - Влагостойкая перегородка КНАУФ-листа АКВАПАНЕЛЬ
 - Озвучка перегородки КНАУФ-листами ФАЙЕР
 - Перегородка из бетона
 - Смешанная перегородка
 - Сборная конструкция