




Маркировочный план фрагмента 5 этажа в осях 4–7/П–З

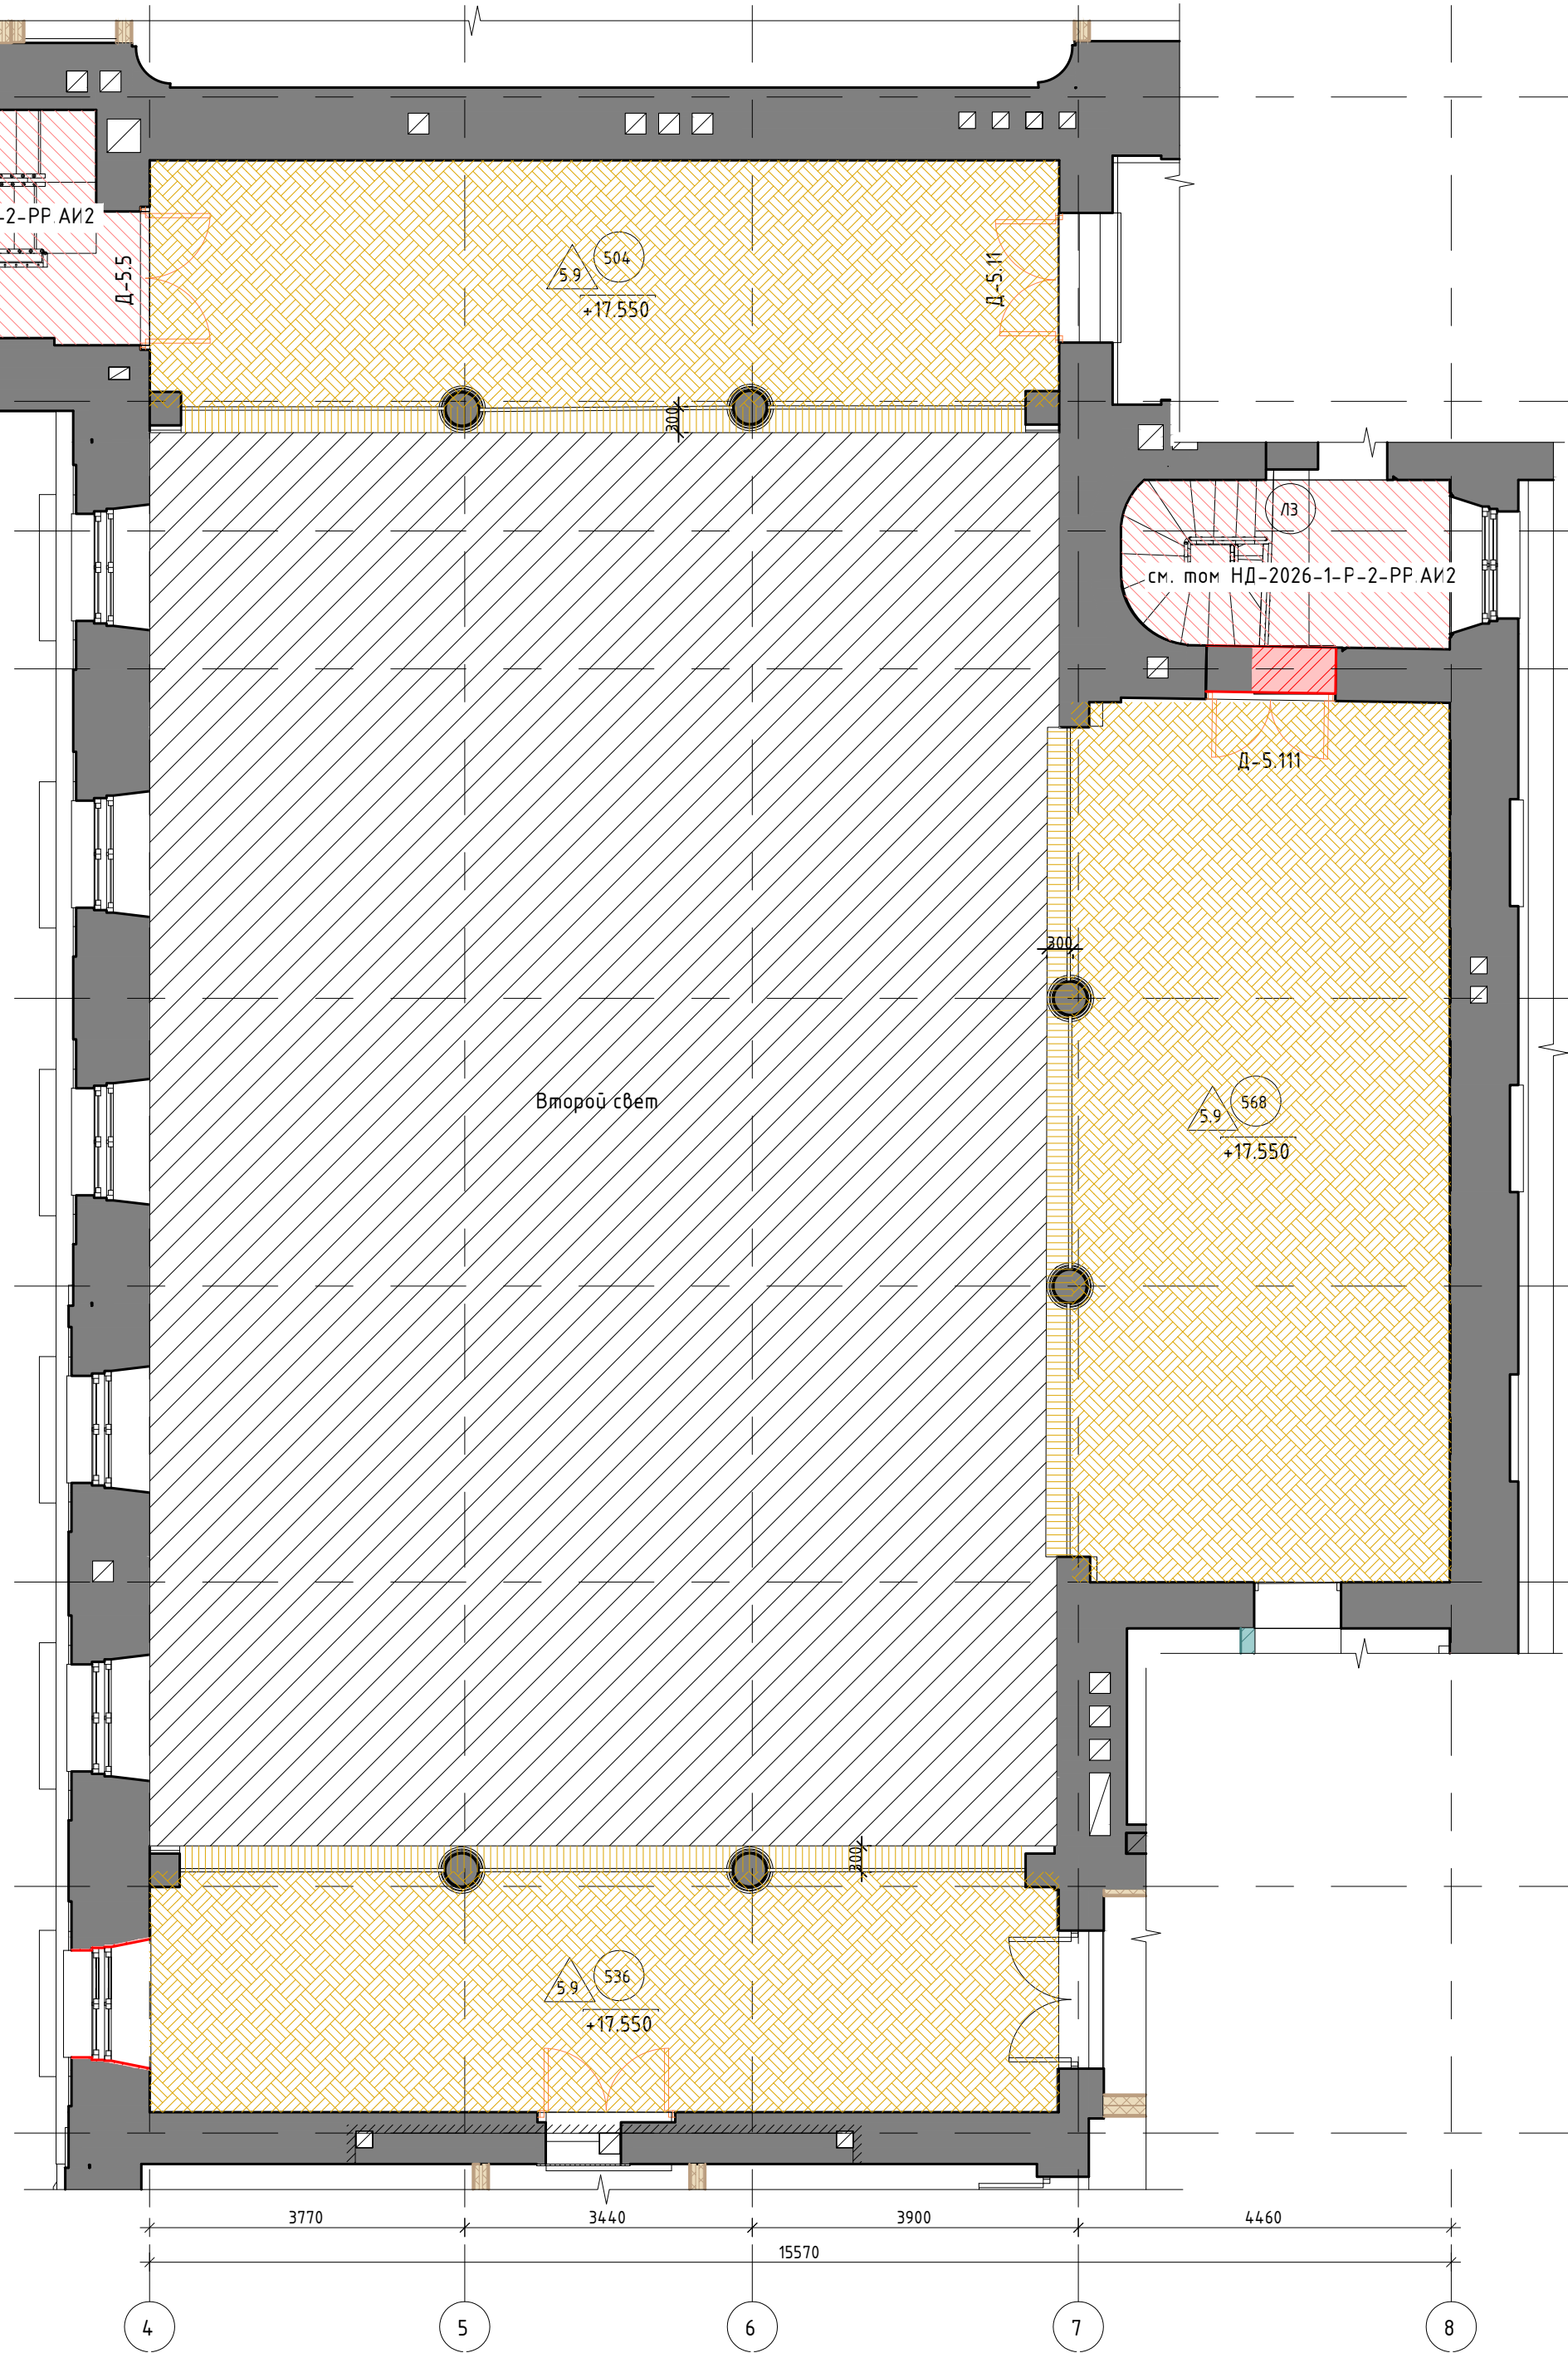


Маркировочный план фрагмента 5 этажа в осях 13–20/У–Ю

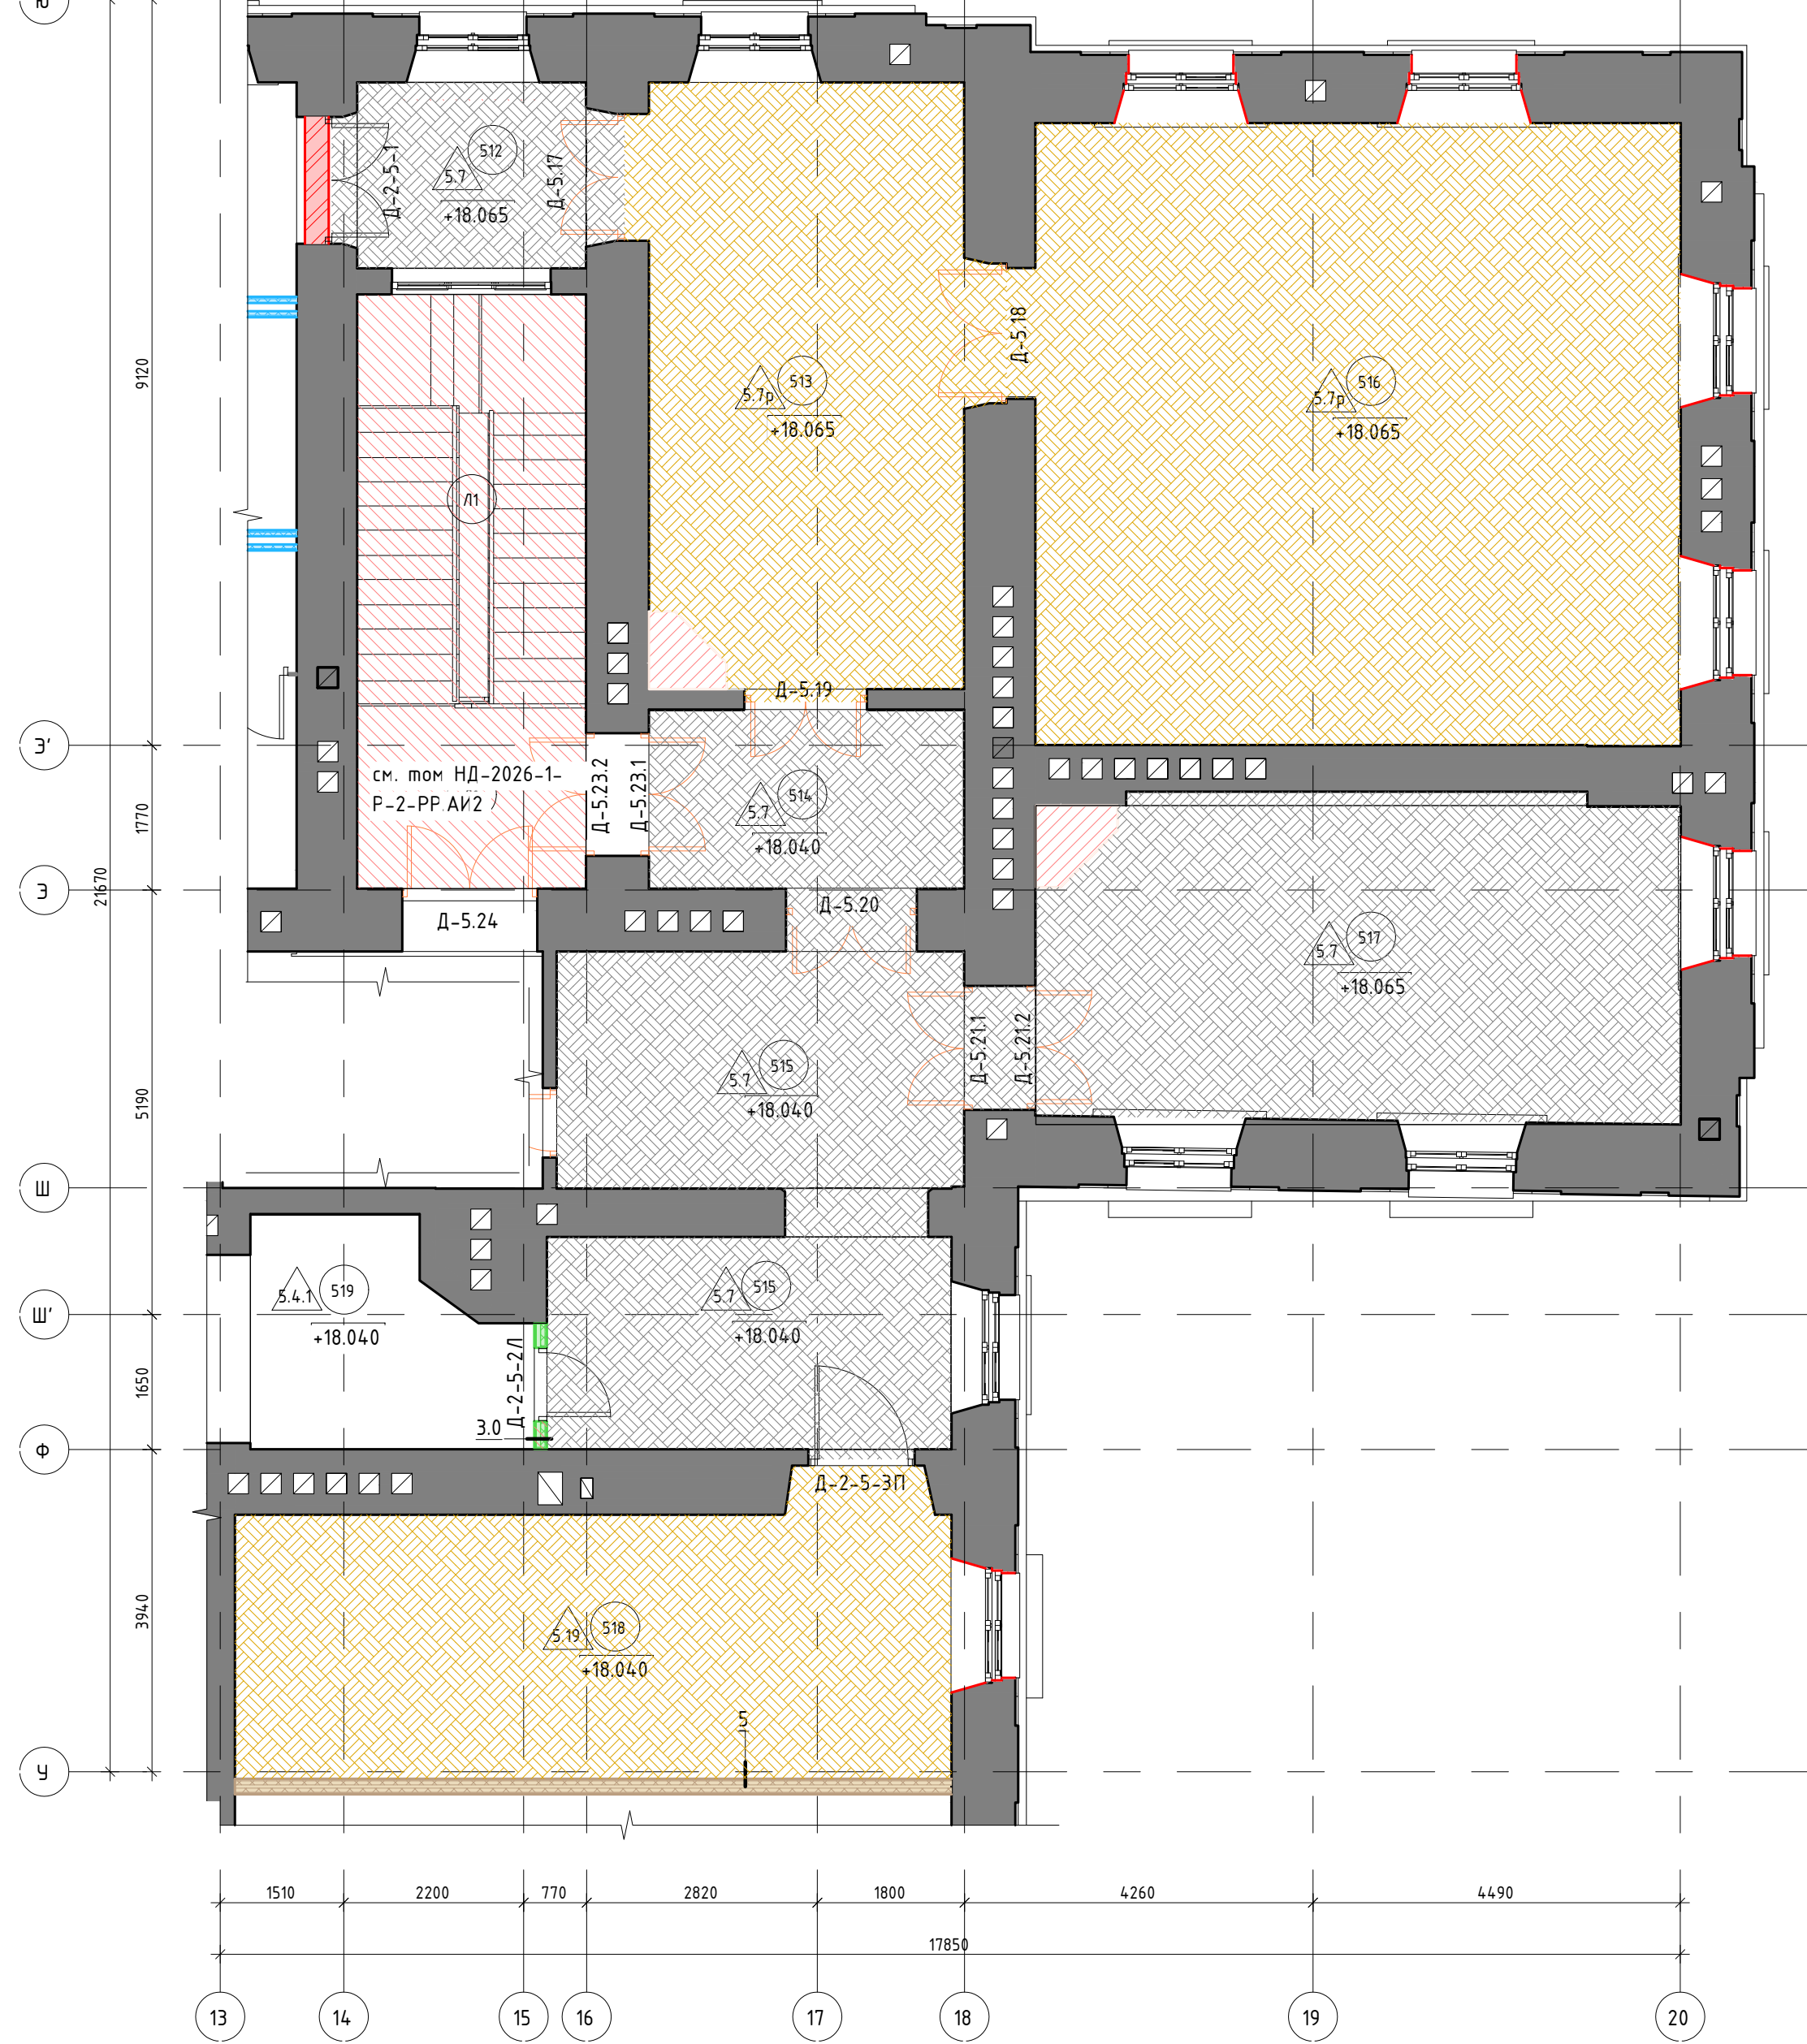

Маркировочный план фрагмента 5 этажа в осях 12–16/Б–Д

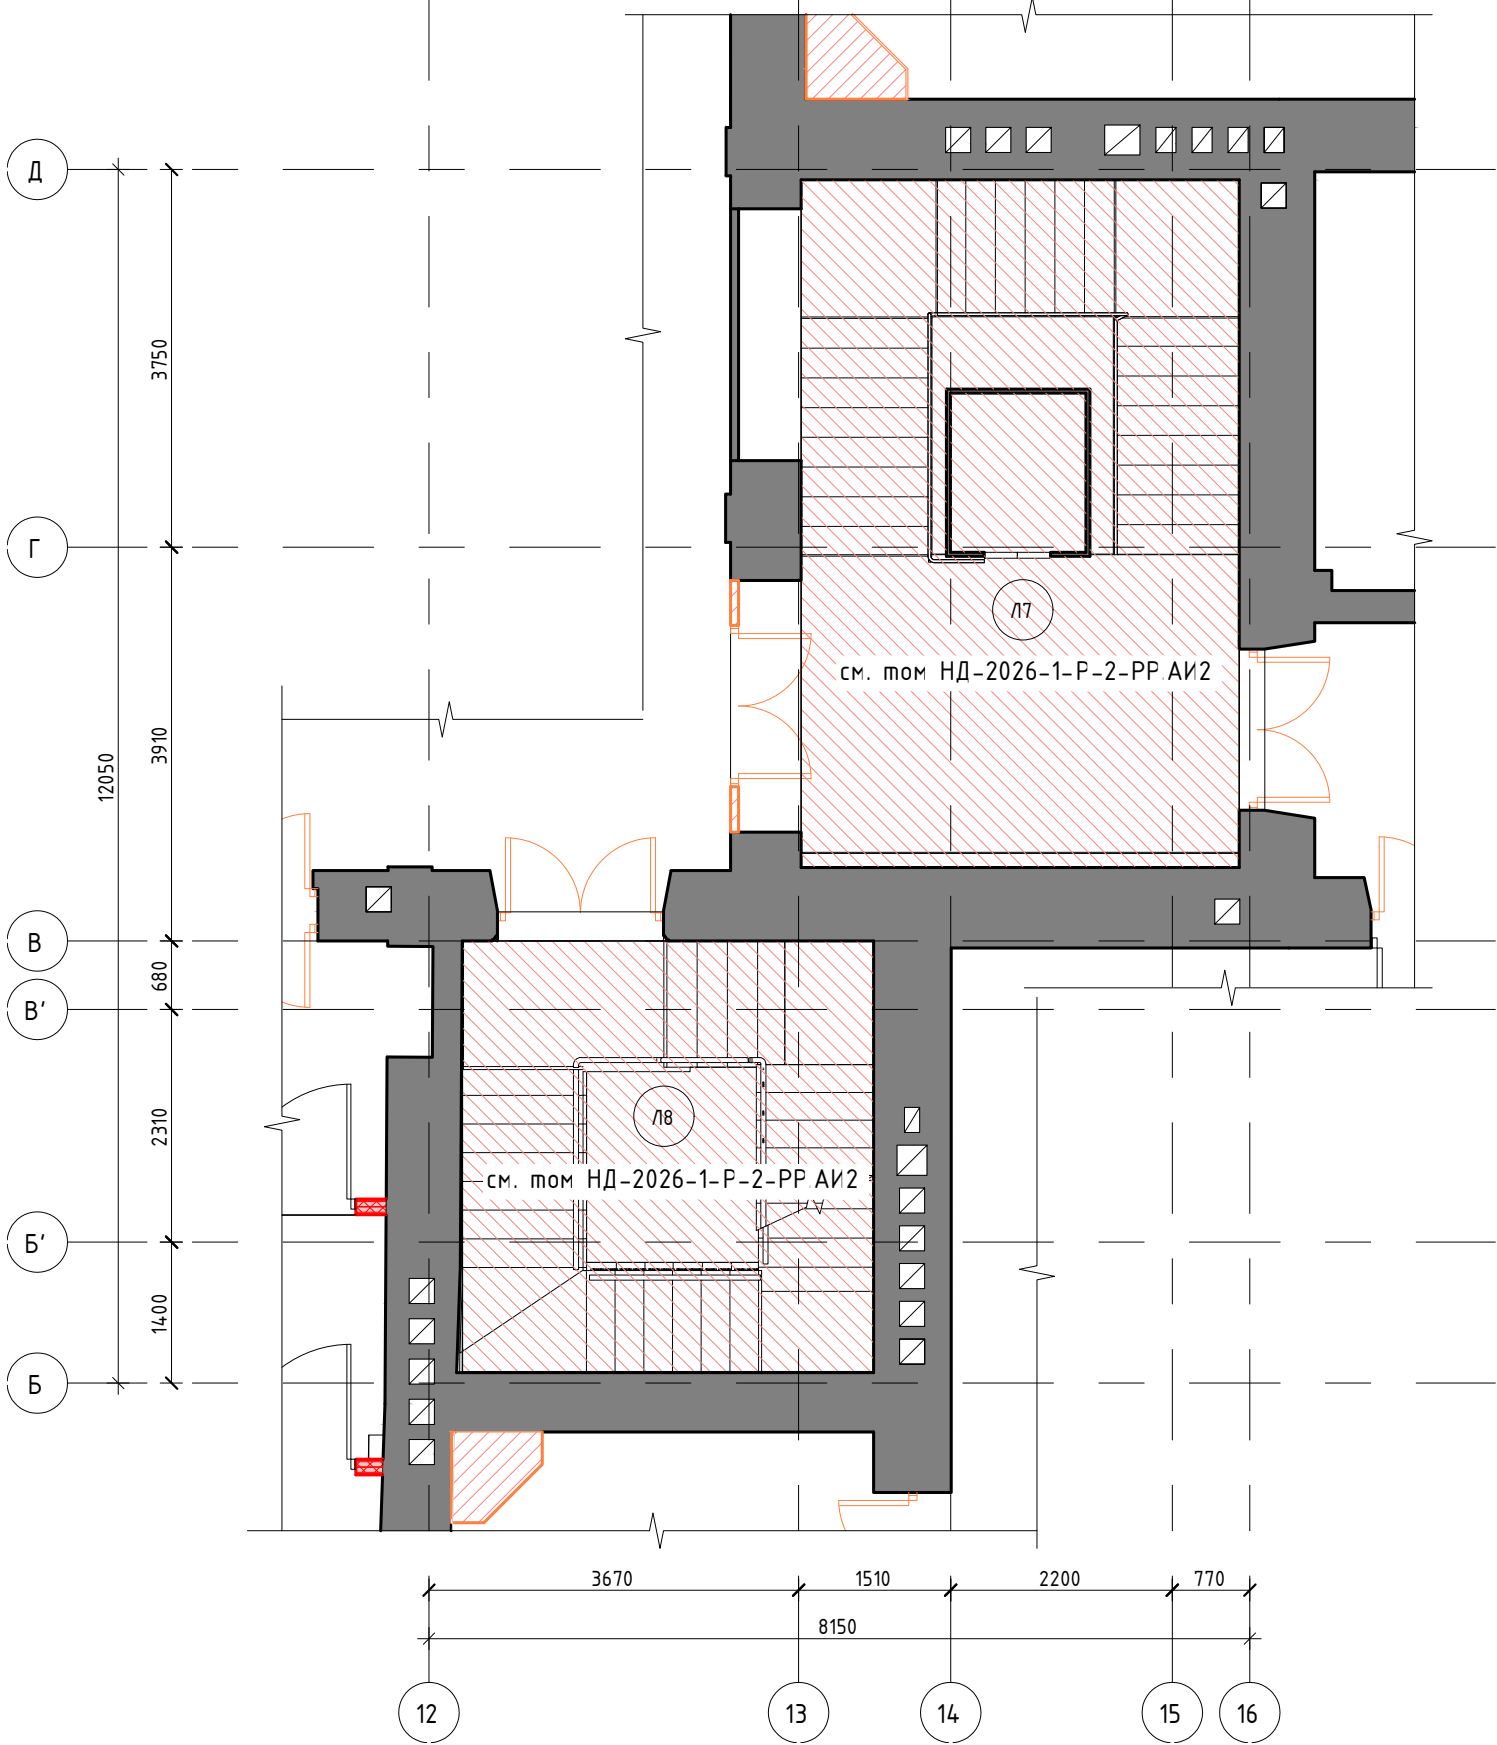

Маркировочный план фрагмента 5 этажа в осях 14–18/Р–С

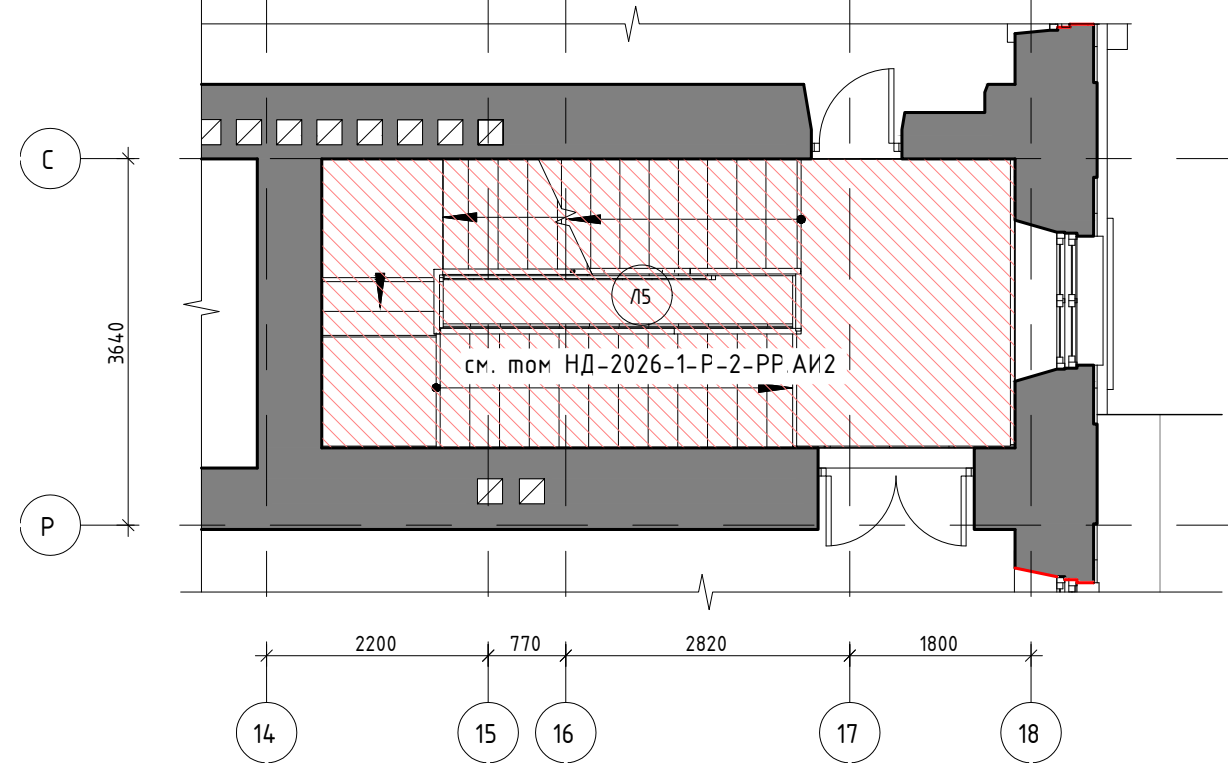

|     |                                |        |
|-----|--------------------------------|--------|
| 514 | Коридор                        | 8.43   |
| 515 | Коридор                        | 27.15  |
| 516 | Репетиторий                    | 60.03  |
| 517 | Комната отдыха                 | 31.30  |
| 518 | Комната отдыха                 | 28.29  |
| 519 | С/У                            | 8.30   |
| 536 | Ложа VIP                       | 34.31  |
| 568 | Ложа VIP                       | 49.19  |
| Л1  | Лестничная клетка (Тип ЛК: Л2) | 20.32  |
| Л2  | Коридор                        | 10.27  |
| Л3  | Технологическая лестница       | 7.71   |
| Л5  | Лестничная клетка (Тип ЛК: Л2) | 19.75  |
| Л7  | Технологическая лестница       | 27.33  |
| Л8  | Лестничная клетка (Тип ЛК: Н2) | 17.57  |
|     |                                | 419.94 |


| Ведомость возводимых перегородок и стен фрагментов 5 этажа в осях 4–8/П–З, 13–20/У–Ю, 12–16/Б–Д,... |                             |                 |            |
|---|-----------------------------|-----------------|------------|
| Марка                                                                                               | Наименование                | Площадь, кв. м. | Примечание |
| 3.0                                                                                                 | КНАУФ перегородка типа С115 | 5.27            |            |
|   |                             | 5.27            |            |

| Спецификация элементов заполнения дверных проемов фрагментов 5 этажа в осях 4–8/П–З, 13–20/У–Ю, 12–16/Б–Д, 14–18/Р–С |                           |            |        |            |       |   |                     |              |                            |            |            |
|---|---------------------------|------------|--------|------------|-------|---|---------------------|--------------|----------------------------|------------|------------|
| Наименование   | Габариты проем по полотну |            | Кол-во | Примечание |       |   | Основание установки | Марка проема | Габариты монтажного проема |            |            |
|   | Высота, мм                | Ширина, мм |        | Озн.-ст    | R, мм | Характеристика   |                     |              | Ширина, мм                 | Высота, мм |            |
| ДМ 2Р 29х13 Г Пр   | 2970                      | 1390       | 1      | -          |       | Тип открывания, количество створок: распашное, 2 створки; Тип дверного блока: открытый деревянный с наличниками; Типы доводчика, петель, порога, ограничителя: без доводчика, со встроенным порогом, ограничитель напольный; Тип ручки: нажимная с планкой без замка;                                                                 | Существующая стена  | П-2-5-11     | 1490                       | 3020       | -          |
| ДС 1Рл 21х9 Пр0 Мз3                                                                                                  | 1990                      | 780        | 1      | -          |       | Тип открывания, количество створок: распашное левое, 1 створка; Тип дверного блока: скрытый деревянный; Типы доводчика, петель, порога, ограничителя: без доводчика, скрытые петли, выпадающий порог, без ограничителя; Тип ручки: нажимная с заверткой; Тип уплотнителя: отсутствует; СКЗД: отсутствует                              | ГКЛ                 | П-2-5-1      | 880                        | 2040       | -          |
| ДМ 1Рл 21х11 Г Пр   | 2120                      | 1140       | 1      | -          |       | Тип открывания, количество створок: распашное правое, 1 створка; Тип дверного блока: открытый деревянный с наличниками; Типы доводчика, петель, порога, ограничителя: без доводчика, скрытые петли, со встроенным порогом, без ограничителя; Тип ручки: нажимная с планкой без замка; Тип уплотнителя: отсутствует; СКЗД: отсутствует | Существующая стена  | П-2-5-2      | 1240                       | 2170       | -          |
| См. том НД-2026-1-2-Р-ДВ                                                                                             | 2940                      | 1550       | 1      | EI30       |       | Тип дверного блока: Учтено в том НД-2026-1-2-Р-ДВ;   | Существующая стена  | П-2-5-9      | 1650                       | 2990       | Дверь в ПО |
| См. том НД-2026-1-2-Р-ДВ                                                                                             | 3320                      | 1390       | 1      | EI30       |       | Тип дверного блока: Учтено в том НД-2026-1-2-Р-ДВ;   | Существующая стена  | П-2-5-13     | 1490                       | 3370       | Дверь в ПО |

| Спецификация элементов заполнения дверных проемов фрагментов 5 этажа в осях 4–8/П–З, 13–20/У–Ю, 12–16/Б–Д, 14–18/Р–С |                             |                             |                           |            |        |            |       |                                                      |                     |              |                            |            |            |
|---|-----------------------------|-----------------------------|---------------------------|------------|--------|------------|-------|------------------------------------------------------|---------------------|--------------|----------------------------|------------|------------|
| Марка дверного заполнения                                                                                            | Обозначение                 | Наименование                | Габариты проем по полотну |            | Кол-во | Примечание |       |                                                      | Основание установки | Марка проема | Габариты монтажного проема |            | Примечание |
|   |                             |                             | Высота, мм                | Ширина, мм |        | Озн.-ст    | R, мм | Характеристика                                       |                     |              | Ширина, мм                 | Высота, мм |            |
| Д-5.17   | См. том НД-2026-1-2-Р-Р-Д В | См. том НД-2026-1-2-Р-Р-Д В | 2970                      | 1390       | 1      | -          |       | Тип дверного блока: Учтено в том НД-2026-1-2-Р-Р-ДВ; | Существующая стена  | П-2-5-10     | 1490                       | 3020       | Дверь в ПО |
| Д-5.18   | См. том НД-2026-1-2-Р-Р-Д В | См. том НД-2026-1-2-Р-Р-Д В | 2940                      | 1550       | 1      | -          |       | Тип дверного блока: Учтено в том НД-2026-1-2-Р-Р-ДВ; | Существующая стена  | П-2-5-8      | 1650                       | 2990       | Дверь в ПО |
| Д-5.19   | См. том НД-2026-1-2-Р-Р-Д В | См. том НД-2026-1-2-Р-Р-Д В | 2920                      | 1340       | 1      | -          |       | Тип дверного блока: Учтено в том НД-2026-1-2-Р-Р-ДВ; | Существующая стена  | П-2-5-4      | 1440                       | 2970       | Дверь в ПО |
| Д-5.20   | См. том НД-2026-1-2-Р-Р-Д В | См. том НД-2026-1-2-Р-Р-Д В | 2920                      | 1440       | 1      | -          |       | Тип дверного блока: Учтено в том НД-2026-1-2-Р-Р-ДВ; | Существующая стена  | П-2-5-7      | 1540                       | 2970       | Дверь в ПО |
| Д-5.21.1   | См. том НД-2026-1-2-Р-Р-Д В | См. том НД-2026-1-2-Р-Р-Д В | 2890                      | 1380       | 1      | -          |       | Тип дверного блока: Учтено в том НД-2026-1-2-Р-Р-ДВ; | Существующая стена  | П-2-5-5      | 1480                       | 2940       | Дверь в ПО |
| Д-5.21.2   | См. том НД-2026-1-2-Р-Р-Д В | См. том НД-2026-1-2-Р-Р-Д В | 2890                      | 1380       | 1      | -          |       | Тип дверного блока: Учтено в том НД-2026-1-2-Р-Р-ДВ; | Существующая стена  | П-2-5-5      | 1480                       | 2940       | Дверь в ПО |
| Д-5.23.1   | См. том НД-2026-1-2-Р-Р-Д В | См. том НД-2026-1-2-Р-Р-Д В | 2890                      | 1380       | 1      | -          |       | Тип дверного блока: Учтено в том НД-2026-1-2-Р-Р-ДВ; | Существующая стена  | П-2-5-6      | 1480                       | 2940       | Дверь в ПО |

| Спецификация элементов    |                             |                             |                 |            |
|---------------------------|-----------------------------|-----------------------------|-----------------|------------|
| Марка дверного заполнения | Обозначение                 | Наименование                | Габариты проема |            |
|                           |                             |                             | Высота, мм      | Ширина, мм |
| Д-5.23.2                  | См. том НД-2026-1-2-Р-Р-Д В | См. том НД-2026-1-2-Р-Р-Д В | 2890            | 1380       |
| Д-5.24                    | См. том НД-2026-1-2-Р-Р-Д В | См. том НД-2026-1-2-Р-Р-Д В | 2840            | 1530       |
| Д-5.111                   | См. том НД-2026-1-2-Р-Р-Д В | См. том НД-2026-1-2-Р-Р-Д В | 2920            | 1390       |

Рисунок паркета “корзинка”. М 1:15

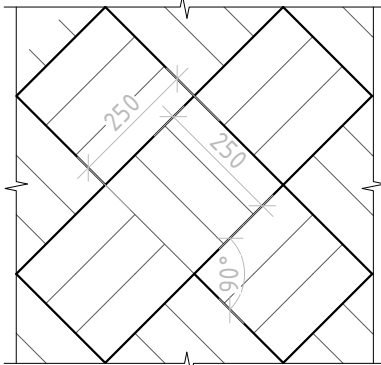

- Условные обозначения:
- 1 - Ось координации
  - +0,000 - Отметка уровня
  - Реставрируемые помещения
  - Сохраняемые конструкции
  - Пробиваемый проем
  - Закладываемый проем
  - Рядовая перегородка
  - ГКЛ-листаны
  - Влагостойкая перегородка КНАУФ-листаны АКВАПАНЕЛЬ
  - Озвучивающая перегородка КНАУФ-листаны ФАЙЕР
  - Перегородка из бетона
  - Смешанная перегородка
  - Сборная конструкция