


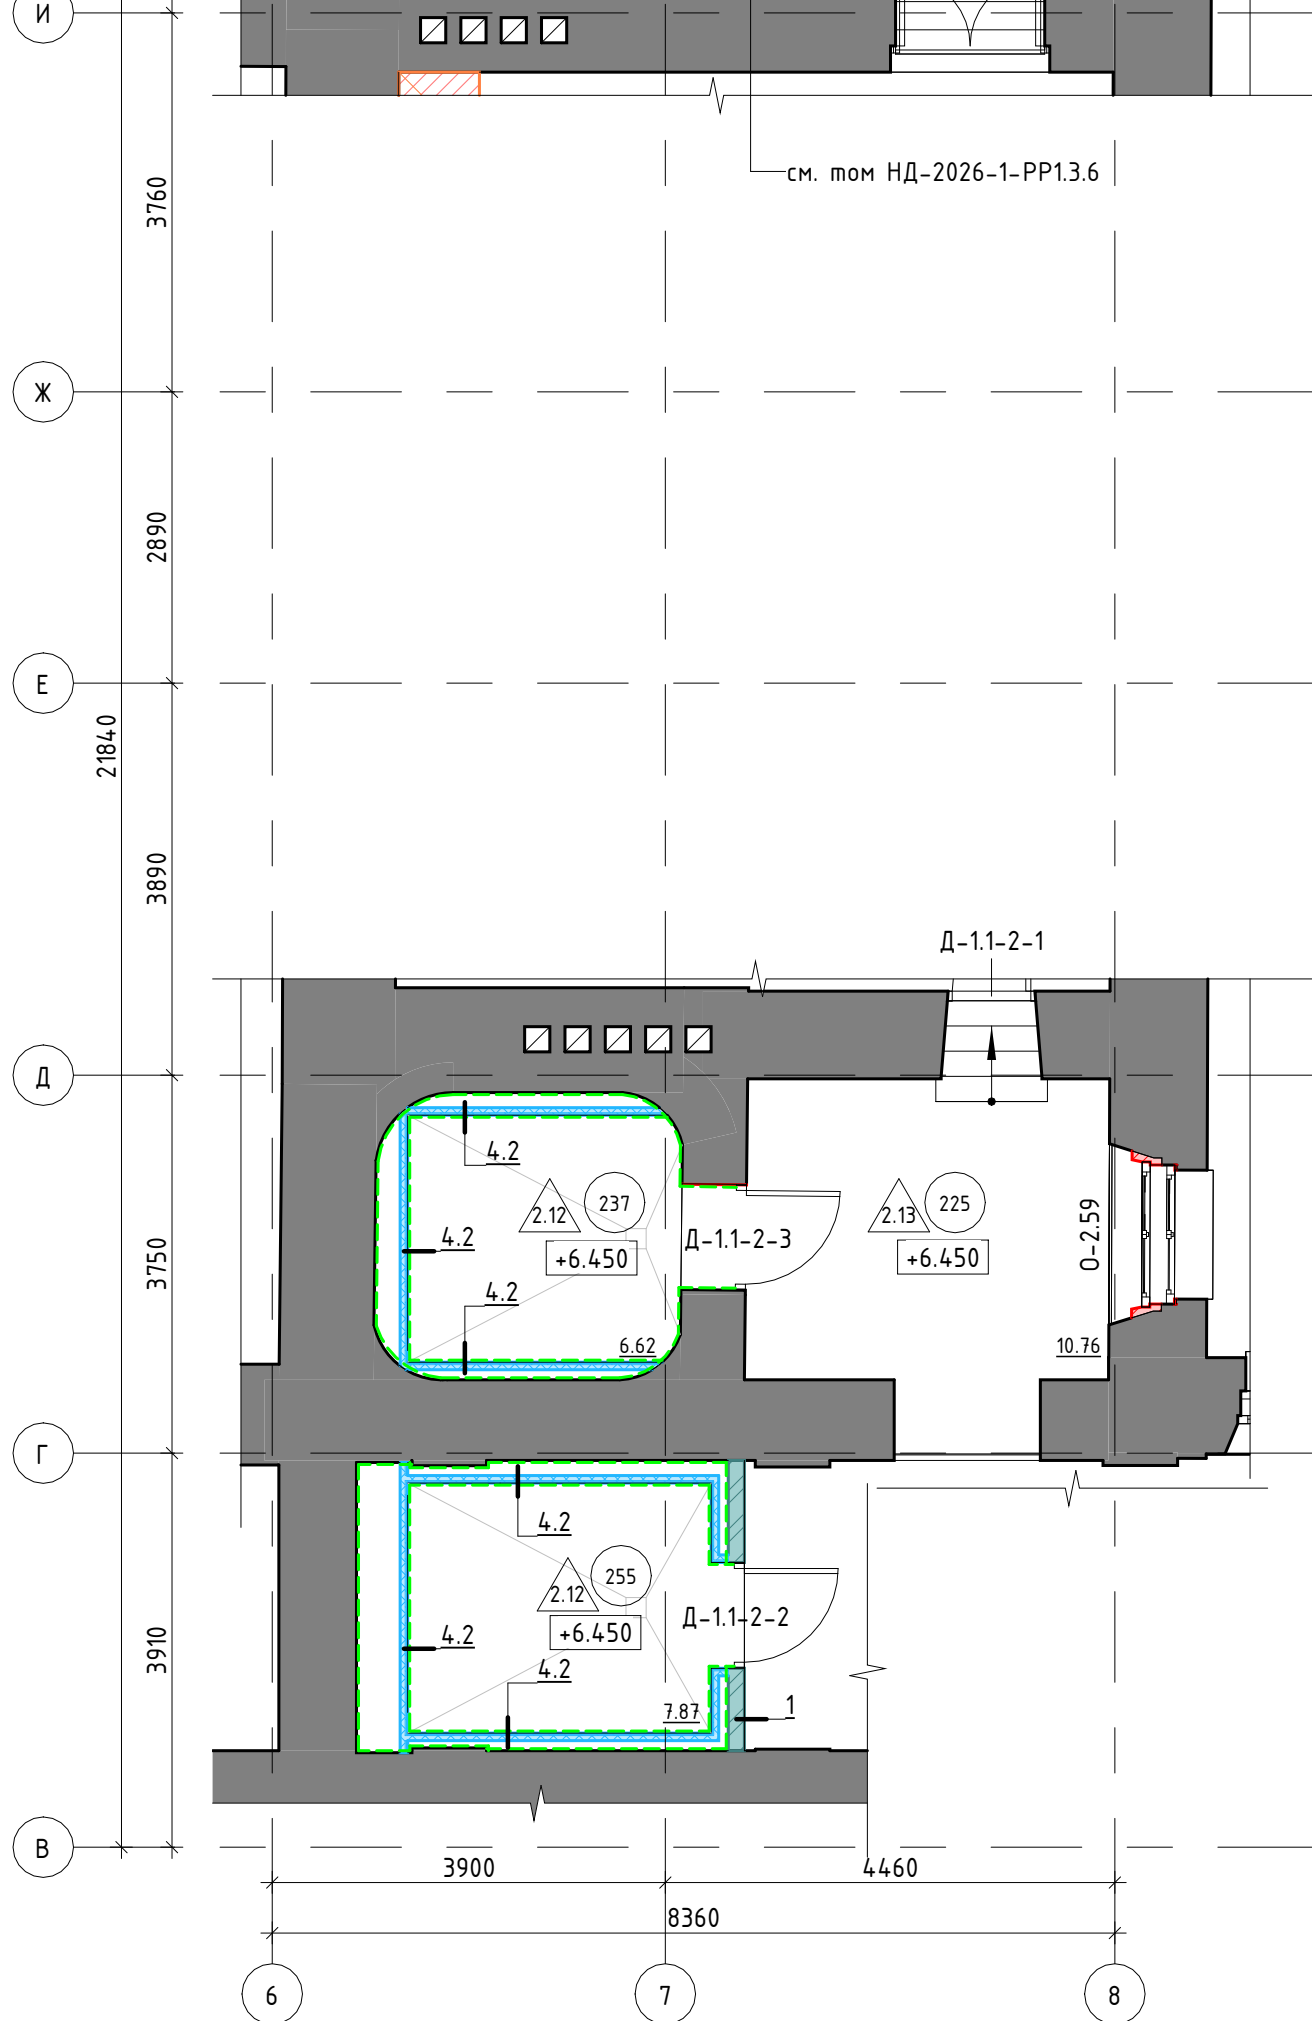

Условные обозначения:

- | | | |
|----------------------------|--|---------------------------------|
| 1 - Ось координации | - Закладываемый проем | - Смешанная перегородка |
| +0,000 - Отметка уровня | - Рядовая перегородка с обшивкой ГКЛ-листами | - Сборная конструкция из фанеры |
| - Реставрируемые помещения | - Влагостойкая перегородка с обшивкой КНАУФ-листами АКВАПАНЕЛЬ | - Акустическая перегородка |
| - Сохраняемые конструкции | - Огнестойкая перегородка обшивкой КНАУФ-листами ФАЙЕРБОРД | - Марка дверного заполнения |
| - Прорываемый проем | - Перегородка из бетонного камня | - Марка оконного заполнения |
| - Марка пола | | |

Номер пом.	Тип пола	Схема пола	Данные элементов пола, мм	Площадь	Примечание
2					
237, 255	2.12		1. Плитка керамогранитная (Ктр=0,40; класс износостойкости 3) на клею см. раздел НД-2026-1-Р-1.1/1.3/1.4/2-АИ - 15+5 мм 2. Гидроизоляция обмазочная на цементной основе (завести на стену, обработать узлы прохода и крепления трубопроводов) - 2 слоя 3. Грунтовка 4. Стяжка уклонообразующая на цементно-песчаном растворе М200, армированная сеткой d5, Вр1 100x100 - 50-100 мм 5. Армированная полиэтиленовая пленка - 300 мкм 6. Засыпка керамзитом М350 Ф10-20 - 280-480 мм 7. Существующее основание - кирпичный свод (см. раздел НД-2026-1-Т01.3)	12.70	Пол санитарного/санитарно-технического помещения; Завести гидроизоляцию на стену на высоту 200 миллиметров от уровня покрытия, на узлы прохода и крепления трубопроводов (S= 26,51 м²); Обеспечить жесткую фиксацию гранул керамзита - после укладки пролить цементным молочком
237	2.12.1		1. Плитка керамогранитная (Ктр=0,40; класс износостойкости 3) на клею см. раздел НД-2026-1-Р-1.1/1.3/1.4/2-АИ - 15+5 мм 2. Гидроизоляция обмазочная на цементной основе (завести на стену, обработать узлы прохода и крепления трубопроводов) - 2 слоя 3. Грунтовка 4. Стяжка уклонообразующая на цементно-песчаном растворе М200, армированная сеткой d5, Вр1 100x100 - 50-100 мм 5. Армированная полиэтиленовая пленка - 300 мкм 6. Засыпка керамзитом М350 Ф10-20 - 300 мм 7. Плита монолитная железобетонная (см. раздел НД-2026-1-Р-1.1-КР) - 150 мм	6.62	Пол санитарного/санитарно-технического помещения; Завести гидроизоляцию на стену на высоту 200 миллиметров от уровня покрытия, на узлы прохода и крепления трубопроводов (S= 26,51 м²); Обеспечить жесткую фиксацию гранул керамзита - после укладки пролить цементным молочком
223, 225	2.13		1. Чистовое покрытие - паркет дубовый на клею под лаком - 15+3 мм 2. Подложка под паркет - фанерные листы ФК водостойкие нешлифованные сорт 3/4, 2 слоя по 15 мм - 30 мм 3. Добор - разреженный деревянный настил 200x25 (шаг 250 мм) - 25 мм Существующая конструкция - см. раздел НД-2026-1-Т01.3: 4. Лага 160x80 (шаг 700 мм) 5. Балка - бревно 120x170 (шаг 1500) с проектной засыпкой керамзитом М350 Ф10-20 - 130-390 мм 6. Существующее основание - кирпичный свод	12.59	Предусмотреть пропитку деревянных исторических элементов конструкции пола огнебиозащитным составом (см. п VIII лист 1) деревянных конструкций полов (захв. 1.1 - S= 22 м²); После обработки деревянных элементов пола произвести дозасыпку керамзитом до верха лаг
				31.91	
				31.91	