


Маркировочный план фрагмента 3 этажа в осях 6-8/Г-К (1: 75)

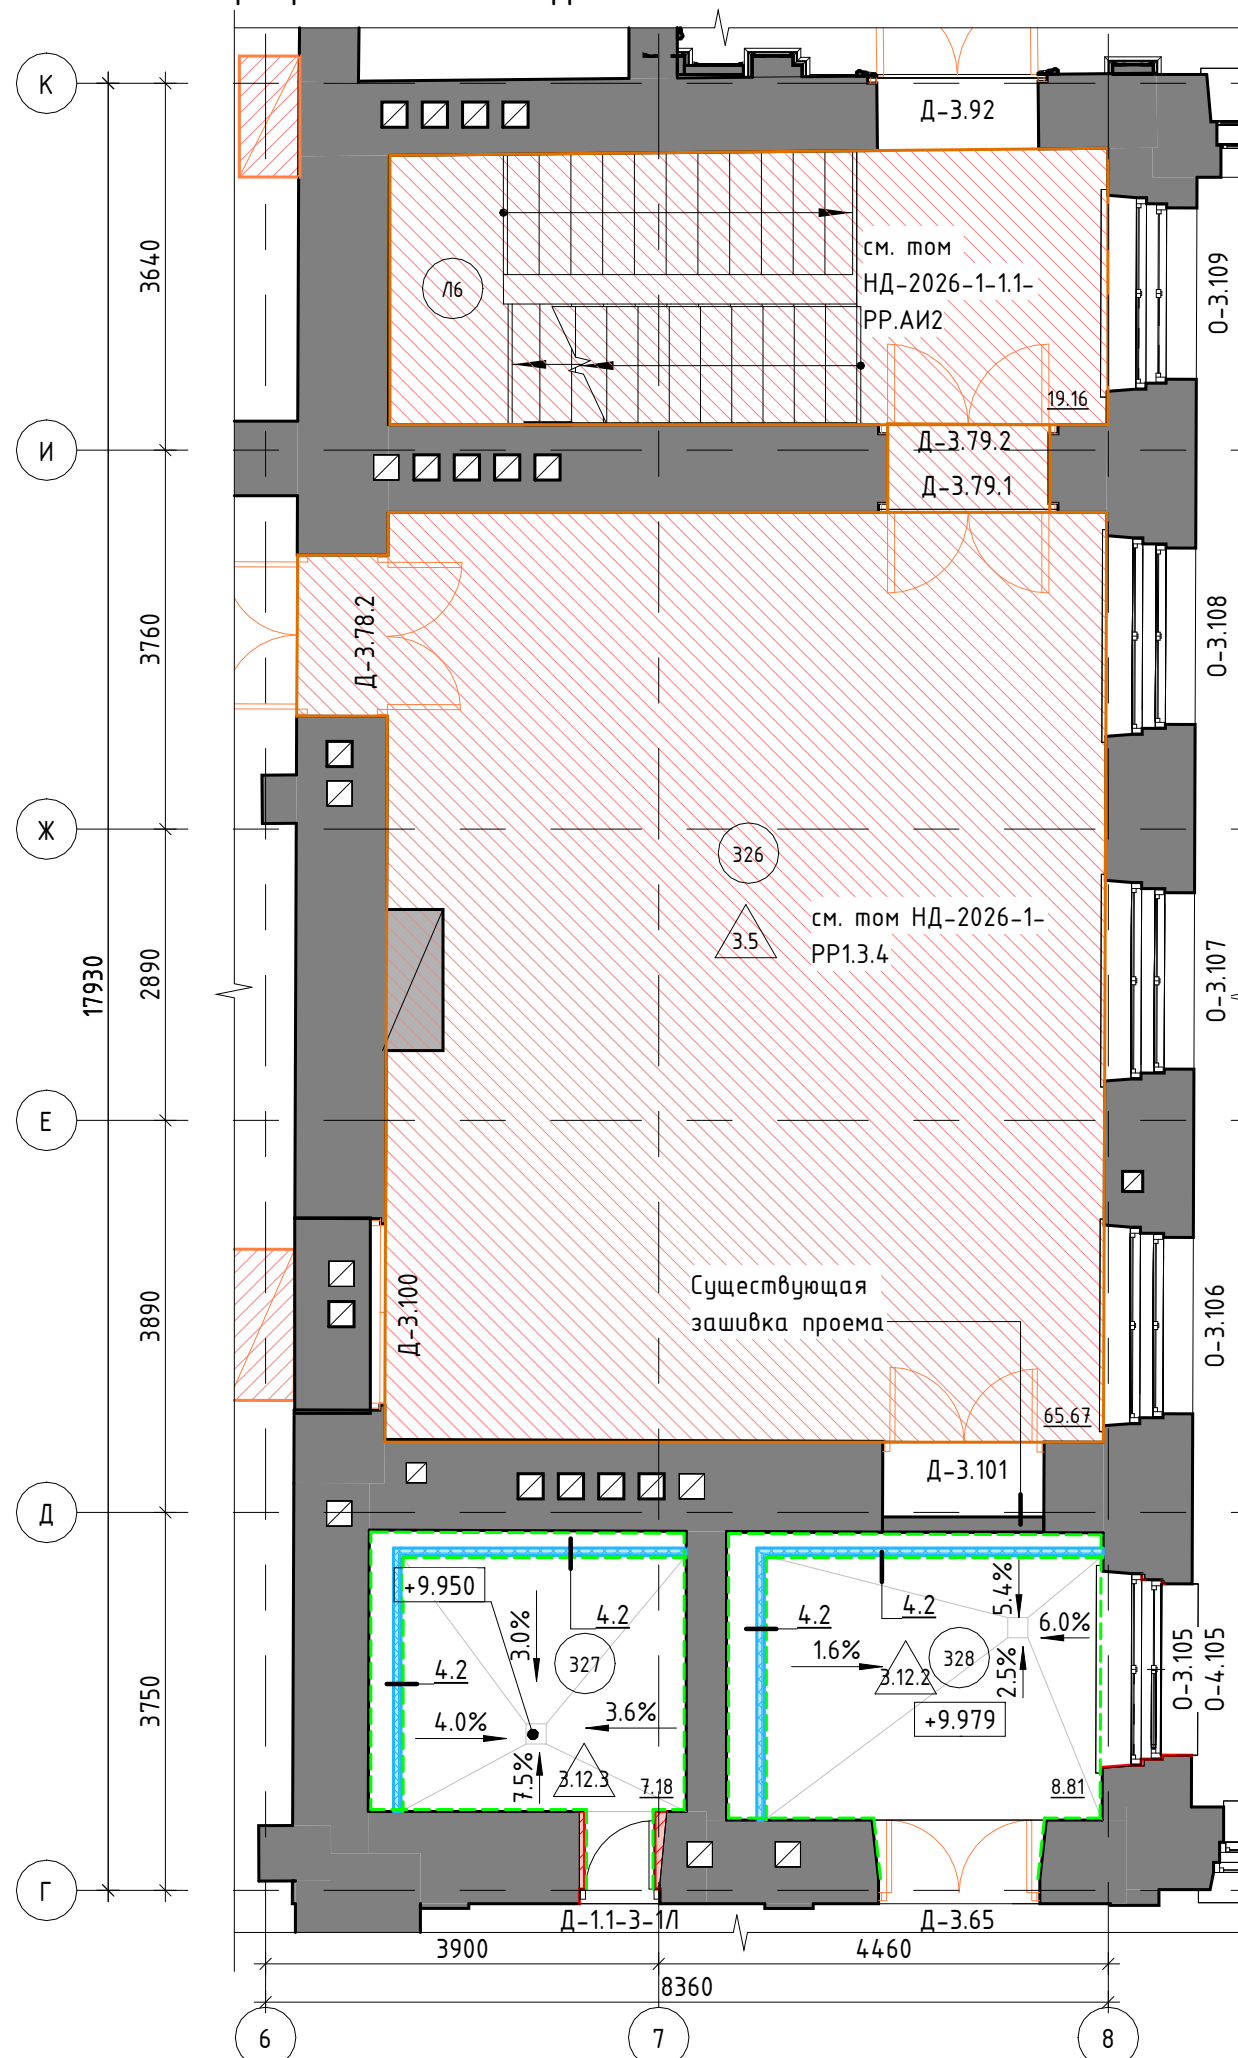

Экспликация помещений фрагмента 3 этажа в осях 6-8/Г-К			
Номер	Имя	Площадь, кв. м.	Кат. пом.
326	Холл	65.67	
327	С/У	7.18	
328	С/У МГН	8.81	
Л6	Лестничная клетка (Тип ЛК: Л2)	19.16	
		100.82	

Ведомость возводимых перегородок и стен фрагмента 3 этажа в осях 6-8/Г-К

Марка	Наименование	Площадь, кв. м	Примечание
4.2	КНАУФ зашивка типа С686	39.87	
		39.87	

Общая экспликация полов фрагмента в осях 6-8/Г-К

Номер пом.	Тип пола	Схема пола	Данные элементов пола, мм
3			
326	3.5		1. Восстанавливаемый паркет на клею под лаком - см. п. 1. НД-2026-1-Р-1.1/1.3/1.4/2-РР.АИ - 15+3 мм 2. Подложка под паркет - фанерные листы ФК водостойкие сорт 3/4, 2 слоя по 15 мм - 30 мм 3. Плита монолитная железобетонная (см. том НД-2026-1-Т) Существующая конструкция - см. раздел НД-2026-1-Т 4. Металлическая балка усиленная трубой и уголками с заполнением пустот минеральной ватой (ρ=35-45 кг/м³) 5. Дощатый накат - 70 мм 6. Существующая штукатурка - 50 мм
327	3.12.2		1. Плитка керамогранитная (Ктр=0,40; класс износостойкости II - см. раздел НД-2026-1-Р-1.1/1.3/1.4/2-АИ - 15+5 мм 2. Гидроизоляция обмазочная на цементной основе (защитный слой обработать узлы прохода и крепления трубопроводов) 3. Грунтовка 4. Стяжка уклонообразующая на цементно-песчаном растворе армированная сеткой d5, Вр1 100х100 - 50-100 мм 5. Армированная полиэтиленовая пленка - 300 мкм 6. Засыпка керамзитом Ф10-20 М350 - 300-470 мм 7. Существующее основание - кирпичный свод (см. раздел НД-2026-1-Т)
327	3.12.3		1. Плитка керамогранитная (Ктр=0,40; класс износостойкости II - см. раздел НД-2026-1-Р-1.1/1.3/1.4/2-АИ - 15+5 мм 2. Гидроизоляция обмазочная на цементной основе (защитный слой обработать узлы прохода и крепления трубопроводов) 3. Грунтовка 4. Стяжка уклонообразующая на цементно-песчаном растворе армированная сеткой d5, Вр1 100х100 - 50-100 мм 5. Армированная полиэтиленовая пленка - 300 мкм 6. Засыпка керамзитом М350 Ф10-20 - 300 мм 7. Плита монолитная железобетонная (см. раздел НД-2026-1-Т)

Спецификация элементов заполнения дверных проемов фрагмента 3 этажа в осях 6-8/Г-К

Марка дверного заполнения	Обозначение	Наименование	Габариты проем по полотну		Кол-во	Примечание			Основание установки	Материал
			Высота, мм	Ширина, мм		Озн.-см	Р. дБ	Характеристика		
Д-1.1-3-1/	ГОСТ 475-2016	ДС 1Рл 21х8 Пр МЗ	1990	680	1	-	-	Тип открывания, количество створок: распашное правое, 1 створка; Тип дверного блока: открытый деревянный с наличниками; Типы доводчика, петель, порога, ограничителя: встроенный доводчик, прямые петли, выпадающий порог, встроенный в доводчик ограничитель; Тип ручки: нажимная с заверткой; СКУД: отсутствует	Существующая стена	П-1.
Д-3.65	См. том НД-2026-1-1.1-РР. ДВ	См. том НД-2026-1-1.1-РР. ДВ	2720	1440	1	-	-	Тип дверного блока: Дверной блок двупольный филенчатый Учтено в томе НД-2026-1-1.1-РР. ДВ;	Существующая стена	П-1.
Д-3.79.1	См. том НД-2026-1-1.1-РР. ДВ	См. том НД-2026-1-1.1-РР. ДВ	2780	1600	1	-	-	Тип дверного блока: Дверной блок двупольный филенчатый Учтено в томе НД-2026-1-1.1-РР. ДВ;	Существующая стена	П-1.
Д-3.79.2	См. том НД-2026-1-1.1-РР. ДВ	См. том НД-2026-1-1.1-РР. ДВ	2780	1600	1	-	-	Тип дверного блока: Дверной блок двупольный филенчатый Учтено в томе НД-2026-1-1.1-РР. ДВ;	Существующая стена	П-1.
Д-3.92	См. том НД-2026-1-1.1-РР. ДВ	См. том НД-2026-1-1.1-РР. ДВ	3540	1600	1	-	-	Тип дверного блока: Дверной блок двупольный филенчатый Учтено в томе НД-2026-1-1.1-РР. ДВ;	Существующая стена	П-1.
Д-3.100	См. том	См. том	3430	1760	1	-	-	Тип дверного блока: Фальш-дверь, дверной блок двупольный	Существующая	П-1.