


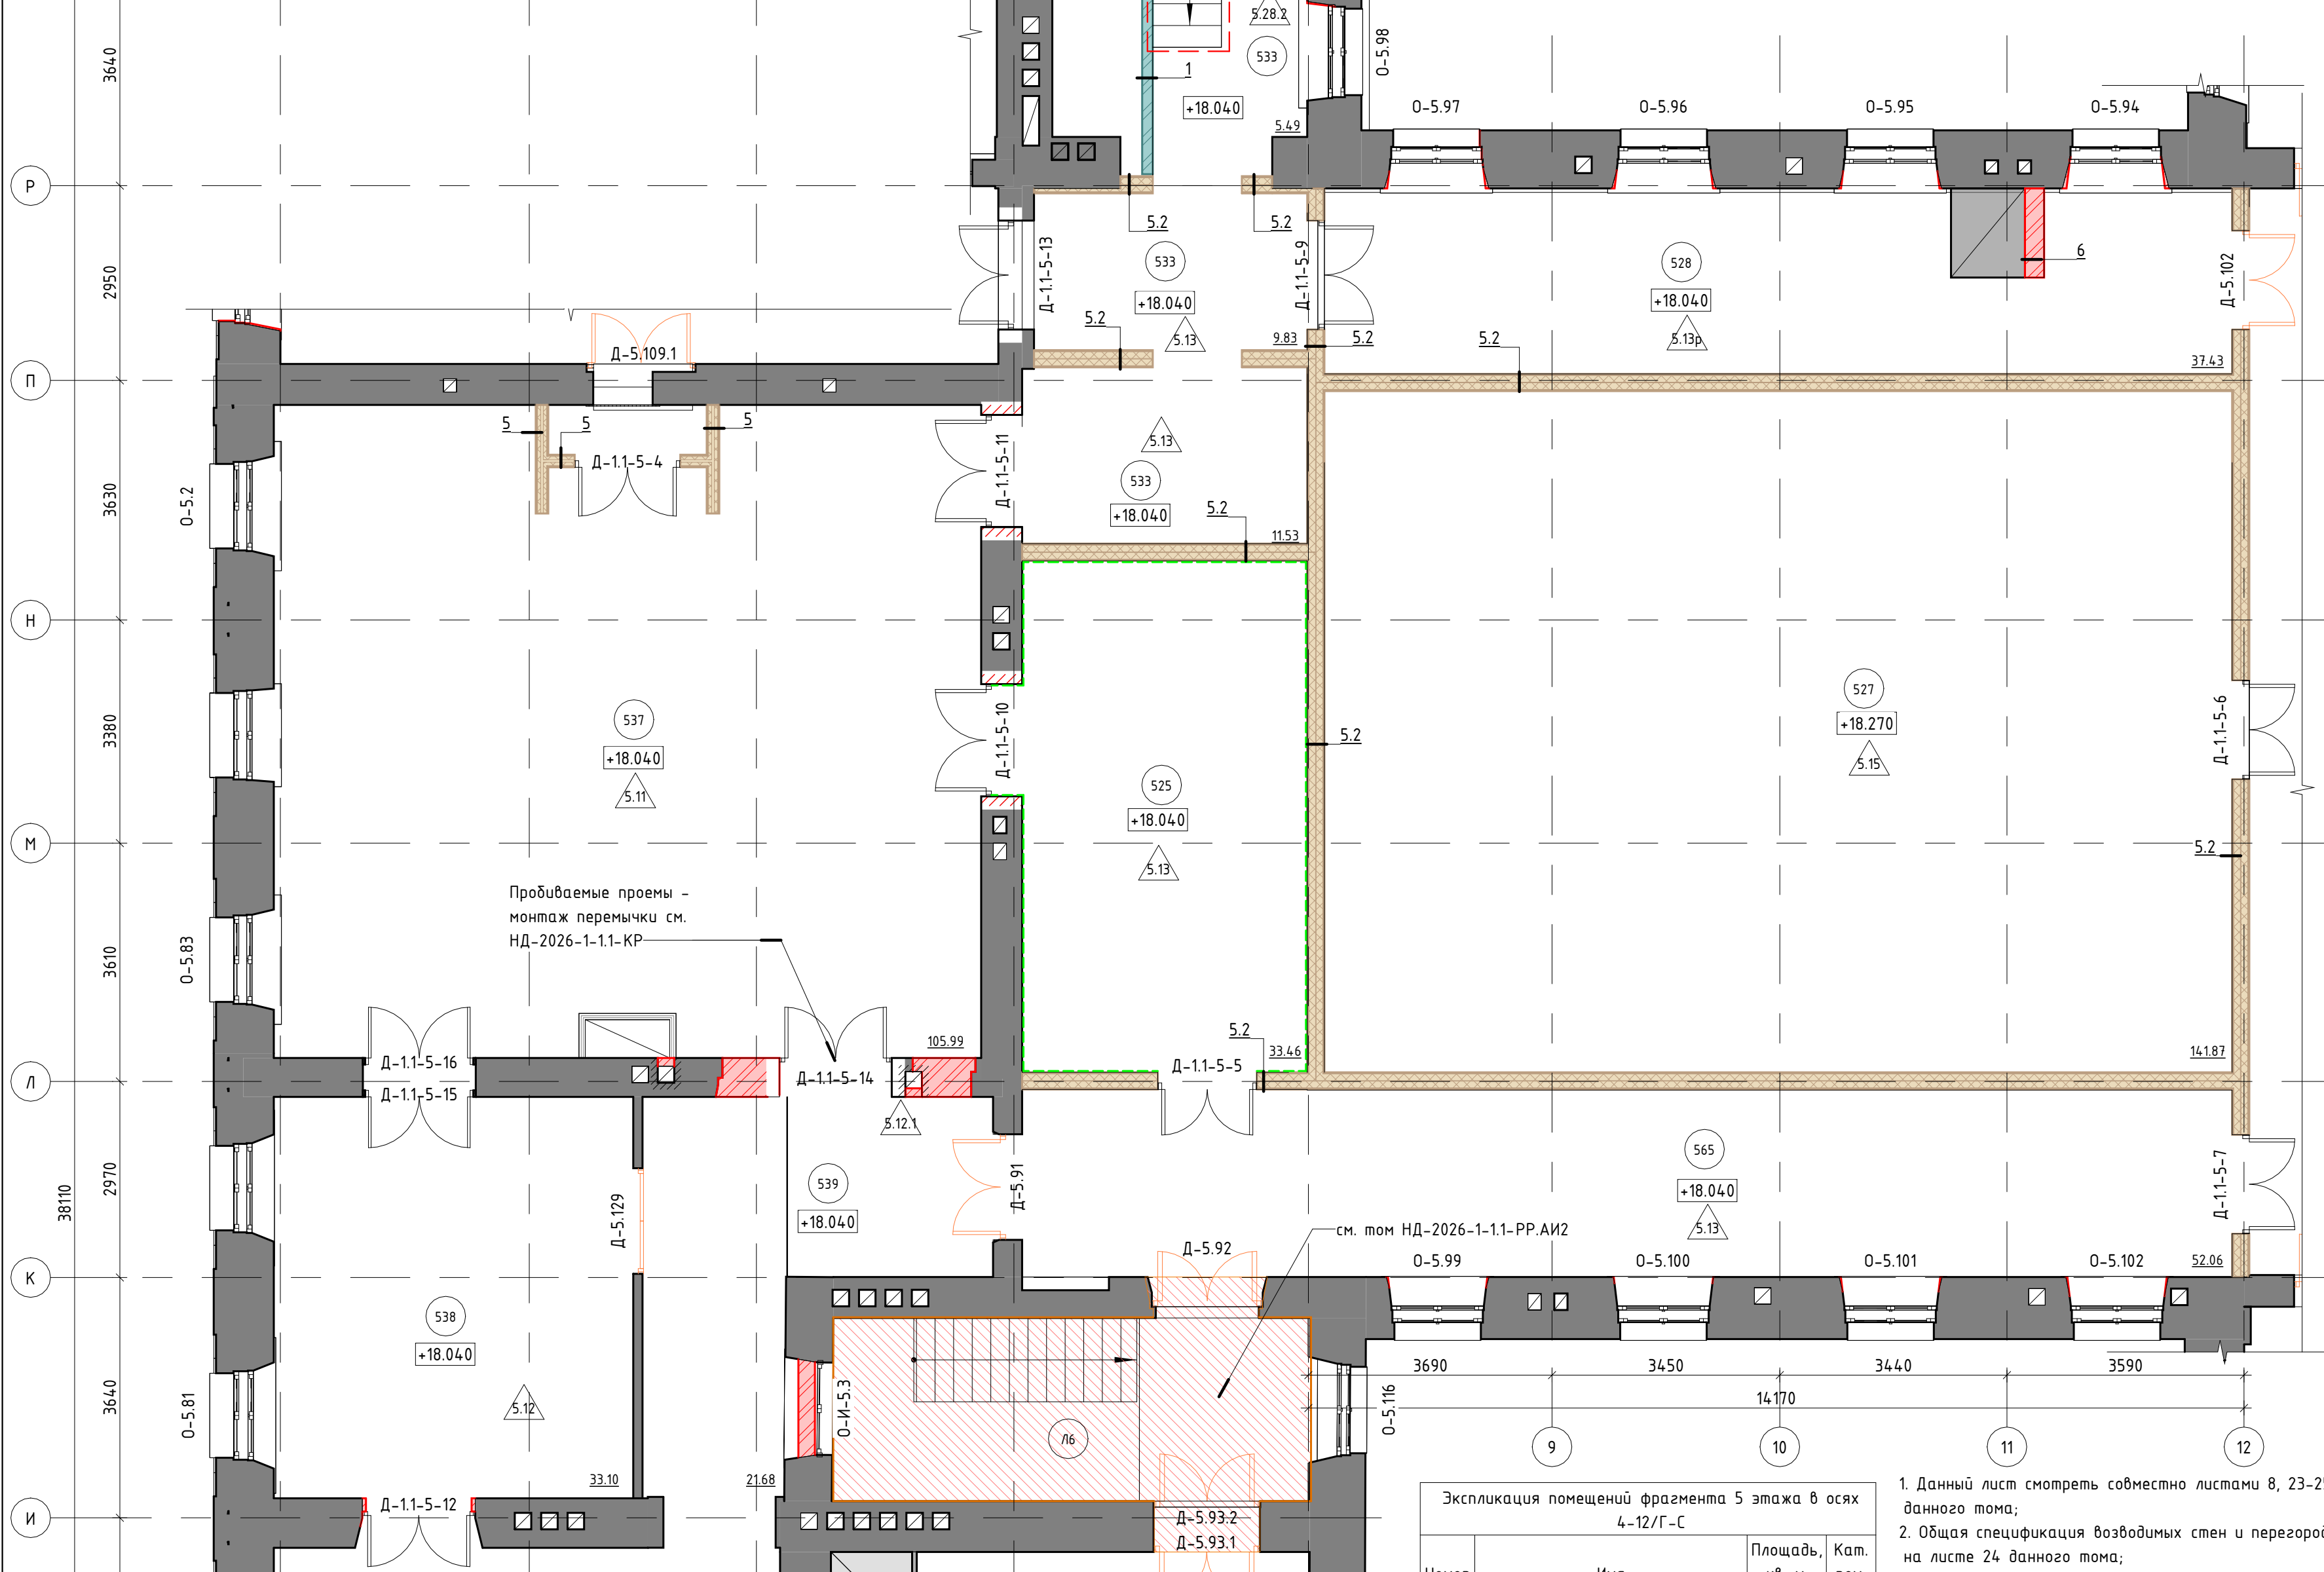

Экспликация помещений фрагмента 5 этажа в осях 4-12/Г-С

Наим.	Изм.	Площадь, кв. м	Кат. помещений

1. Данный лист смотреть совместно листами 8, 23-25 данного тома;
2. Общая спецификация возводимых стен и перегородок на листе 24 данного тома;