


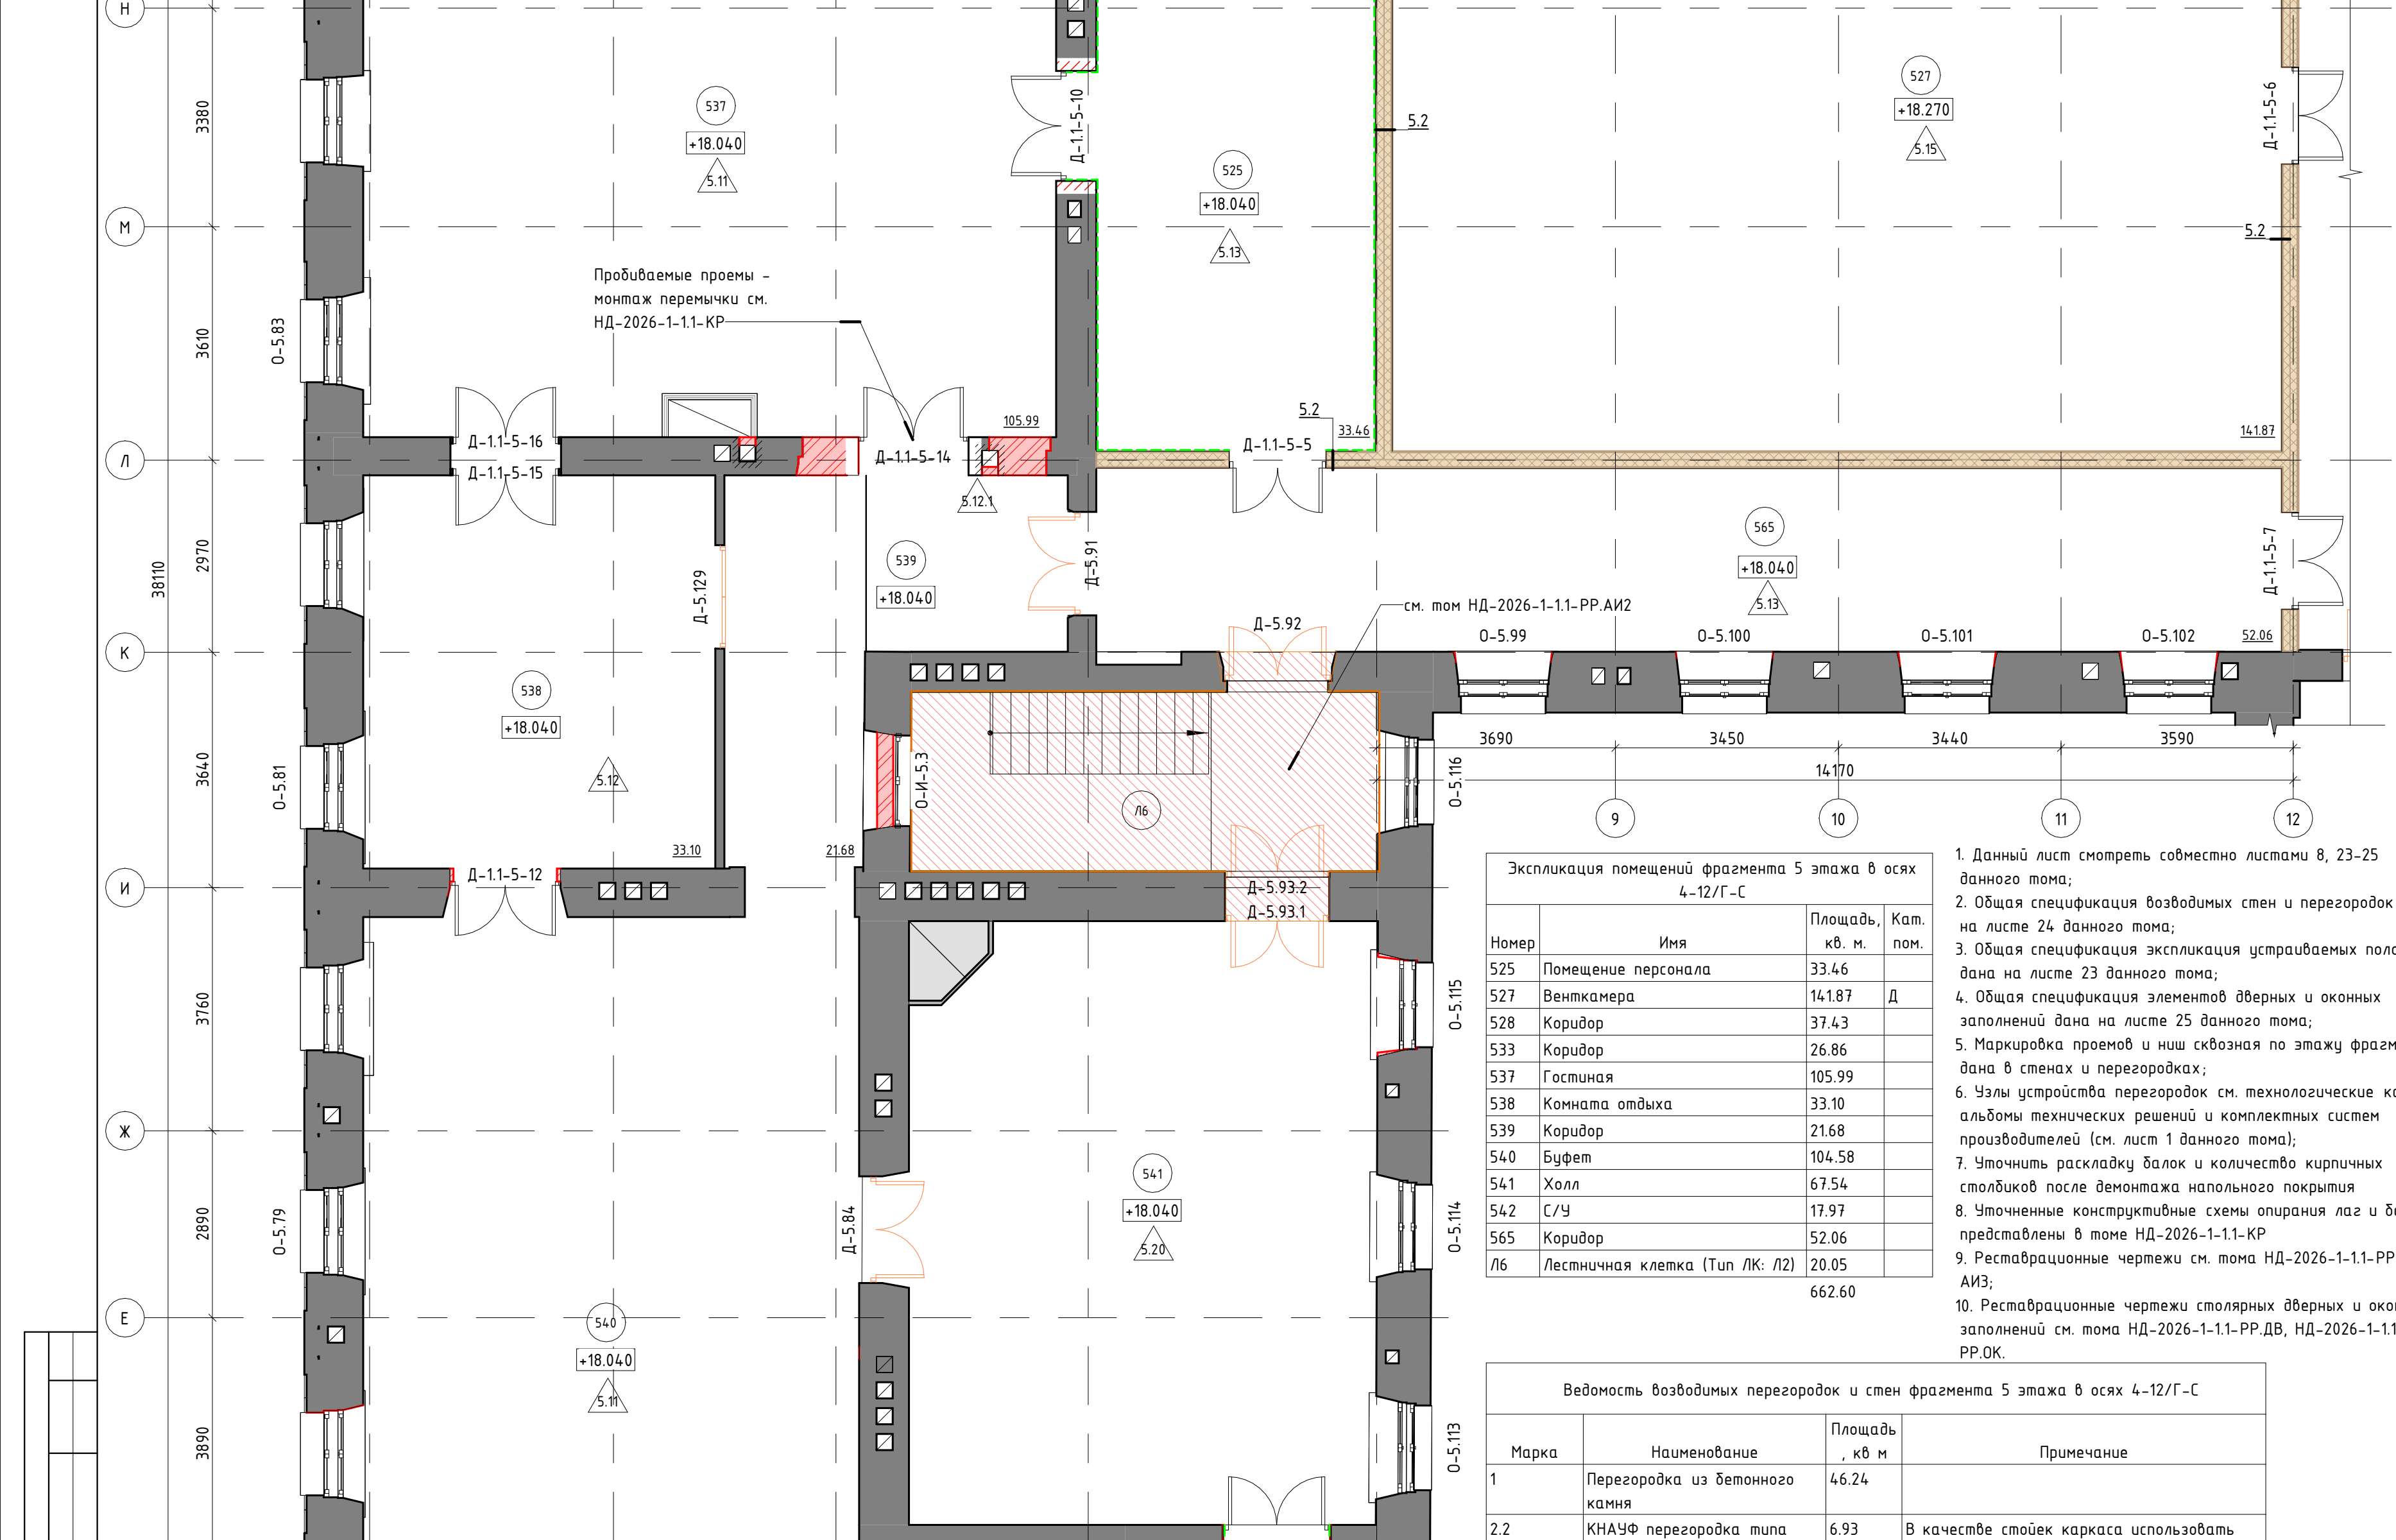

Экспликация помещений фрагмента 5 этажа в осях 4-12/Г-С			
Номер	Имя	Площадь, кв. м.	Кат. пом.
525	Помещение персонала	33.46	
527	Венткамера	141.87	Д
528	Коридор	37.43	
533	Коридор	26.86	
537	Гостиная	105.99	
538	Комната отдыха	33.10	
539	Коридор	21.68	
540	Буфет	104.58	
541	Холл	67.54	
542	С/У	17.97	
565	Коридор	52.06	
Л6	Лестничная клетка (Тип ЛК: Л2)	20.05	
		662.60	

- Данный лист смотреть совместно листами 8, 23-25 данного тома;
- Общая спецификация возводимых стен и перегородок на листе 24 данного тома;
- Общая спецификация экспликация устраиваемых полов дана на листе 23 данного тома;
- Общая спецификация элементов дверных и оконных заполнений дана на листе 25 данного тома;
- Маркировка проемов и ниш сквозная по этажу фрагмента дана в стенах и перегородках;
- Узлы устройства перегородок см. технологические карты альбомы технических решений и комплектных систем производителей (см. лист 1 данного тома);
- Уточнить раскладку балок и количество кирпичных столбиков после демонтажа напольного покрытия
- Уточненные конструктивные схемы опирания лаг и балок представлены в томе НД-2026-1-1.1-КР
- Реставрационные чертежи см. тома НД-2026-1-1.1-РР.АИЗ;
- Реставрационные чертежи столярных дверных и оконных заполнений см. тома НД-2026-1-1.1-РР.ДВ, НД-2026-1-1.1-РР.ОК.

Ведомость возводимых перегородок и стен фрагмента 5 этажа в осях 4-12/Г-С			
Марка	Наименование	Площадь, кв. м	Примечание
1	Перегородка из бетонного камня	46.24	
2.2	КНАУФ перегородка типа	6.93	В качестве стоек каркаса использовать