


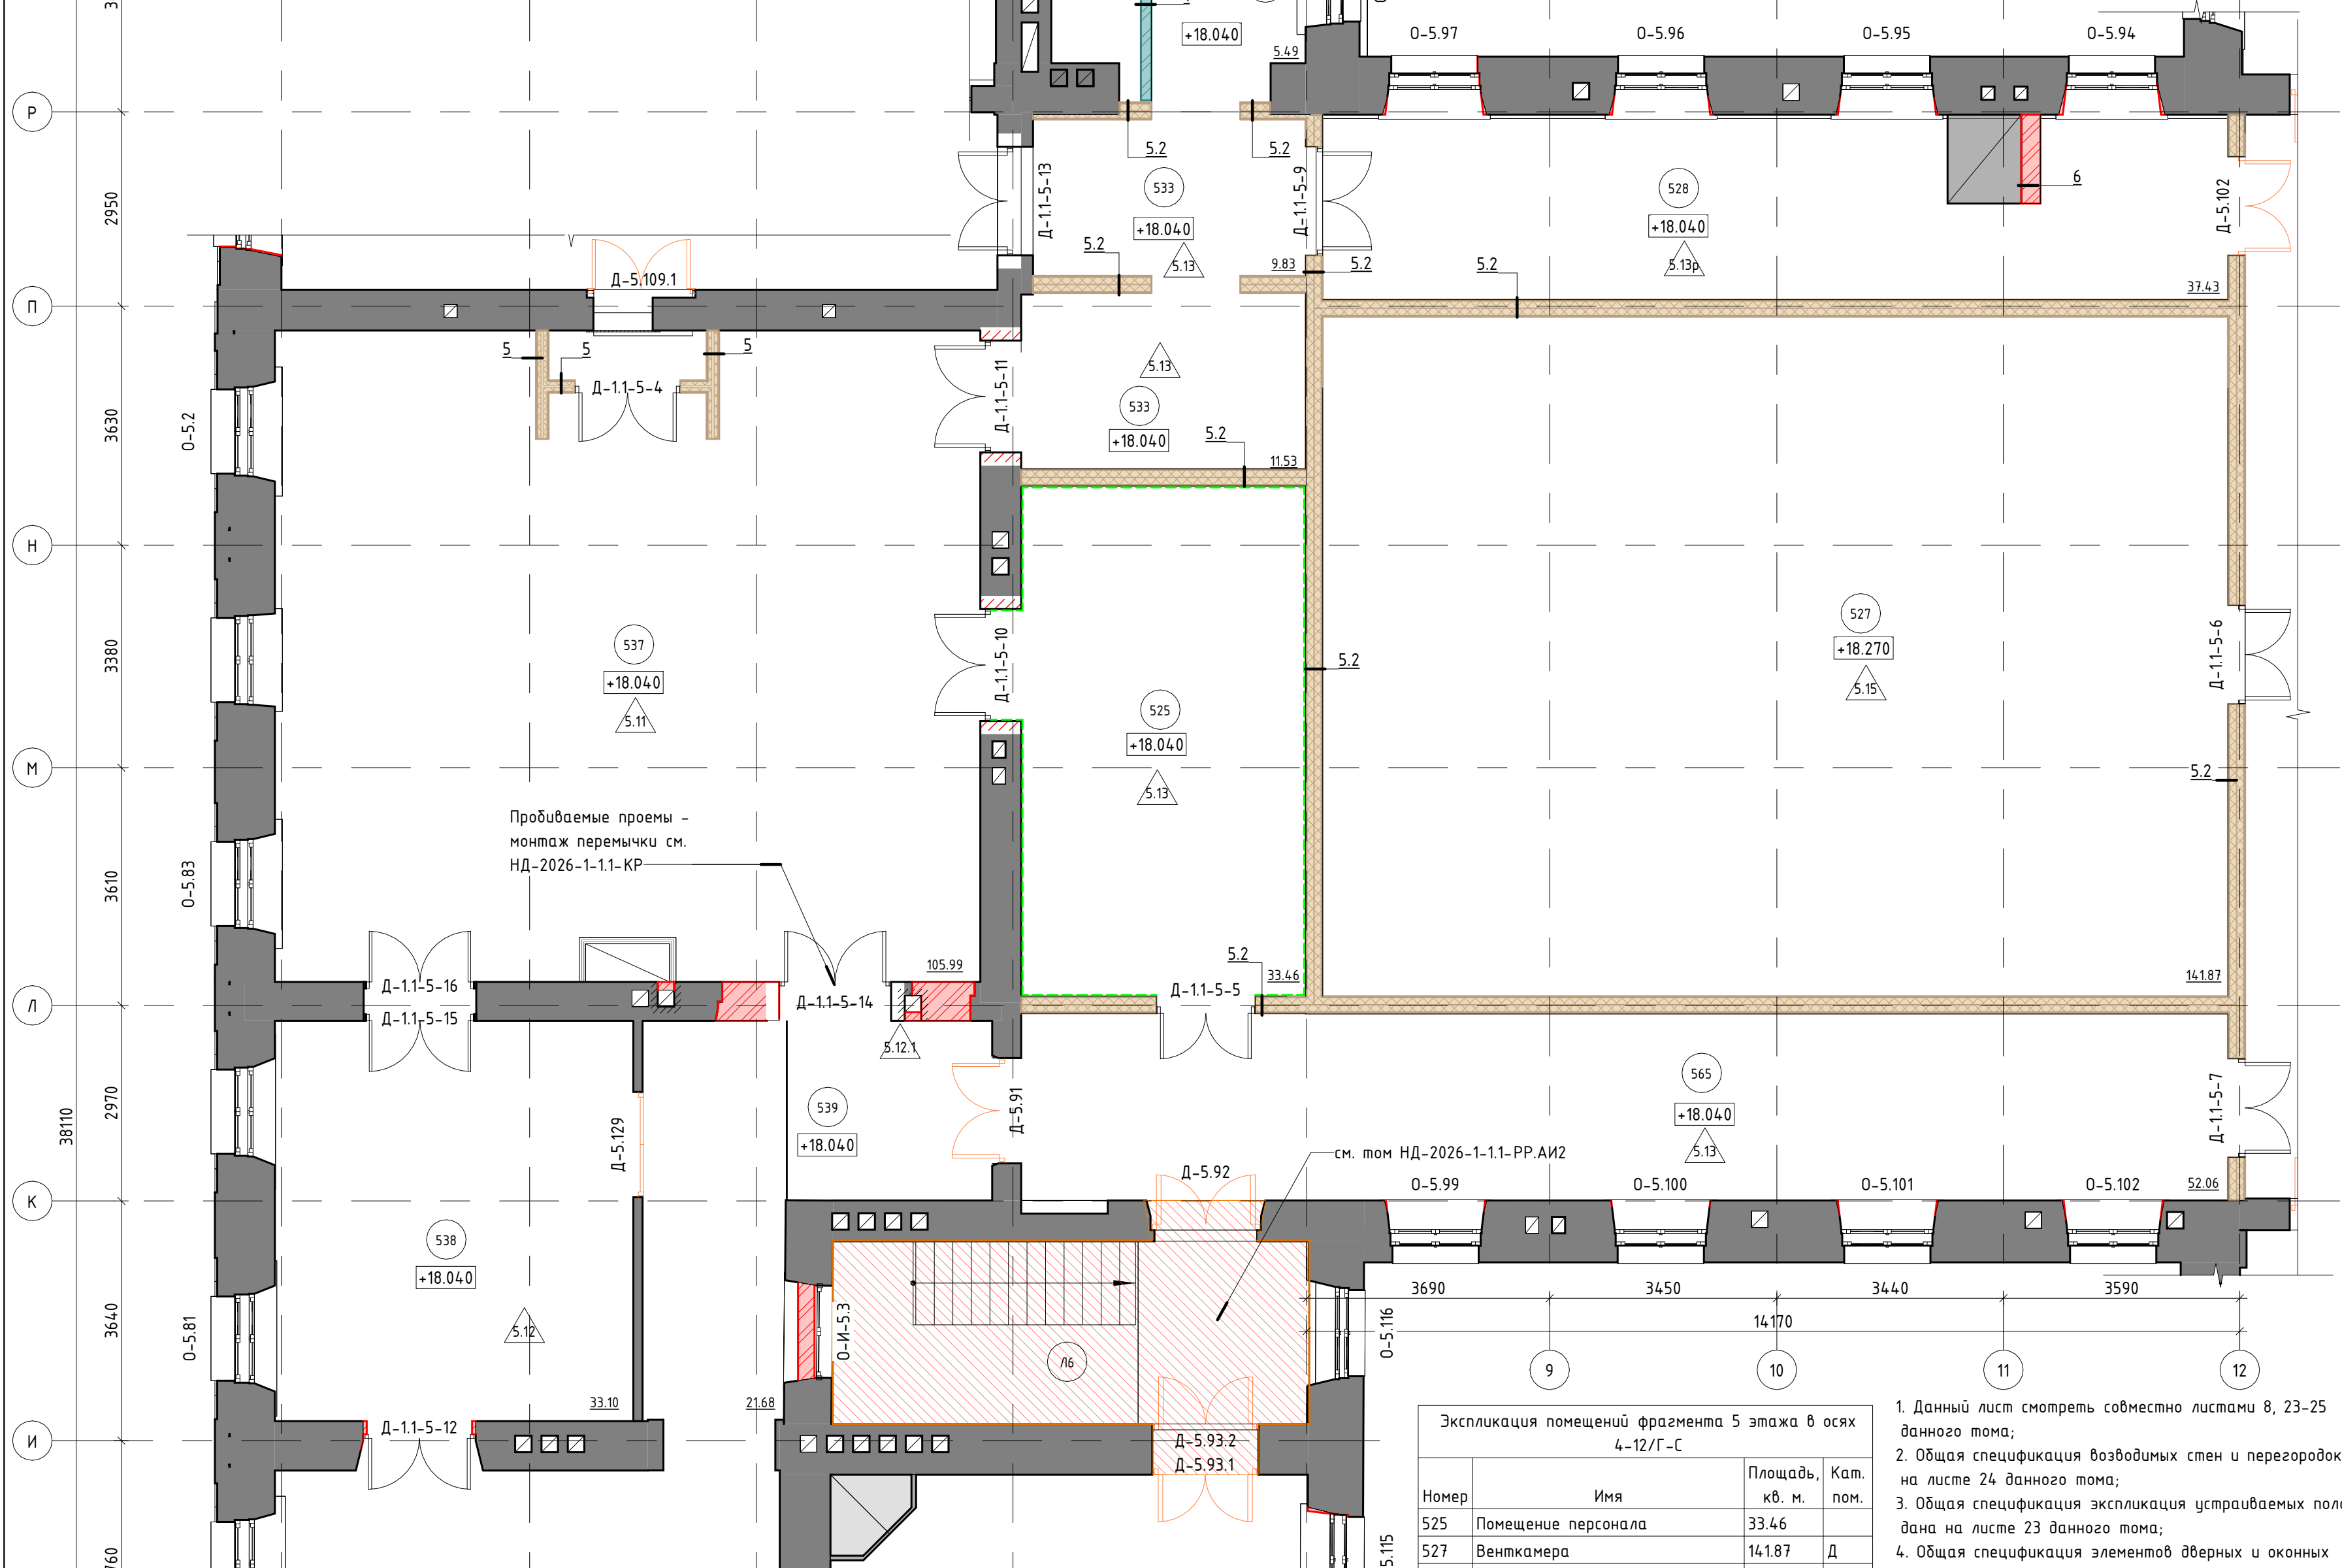

Экспликация помещений фрагмента 5 этажа в осях 4-12/Г-С			
Номер	Имя	Площадь, кв. м.	Кат. пом.
525	Помещение персонала	33.46	
527	Венткамера	141.87	Д

1. Данный лист смотреть совместно листами 8, 23-25 данного тома;
2. Общая спецификация возводимых стен и перегородок дана на листе 24 данного тома;
3. Общая спецификация экспликация устраиваемых полов дана на листе 23 данного тома;
4. Общая спецификация элементов дверных и оконных