


Маркировочный план фрагмента 5 этажа в осях 4-12/Г-С (1 : 75)

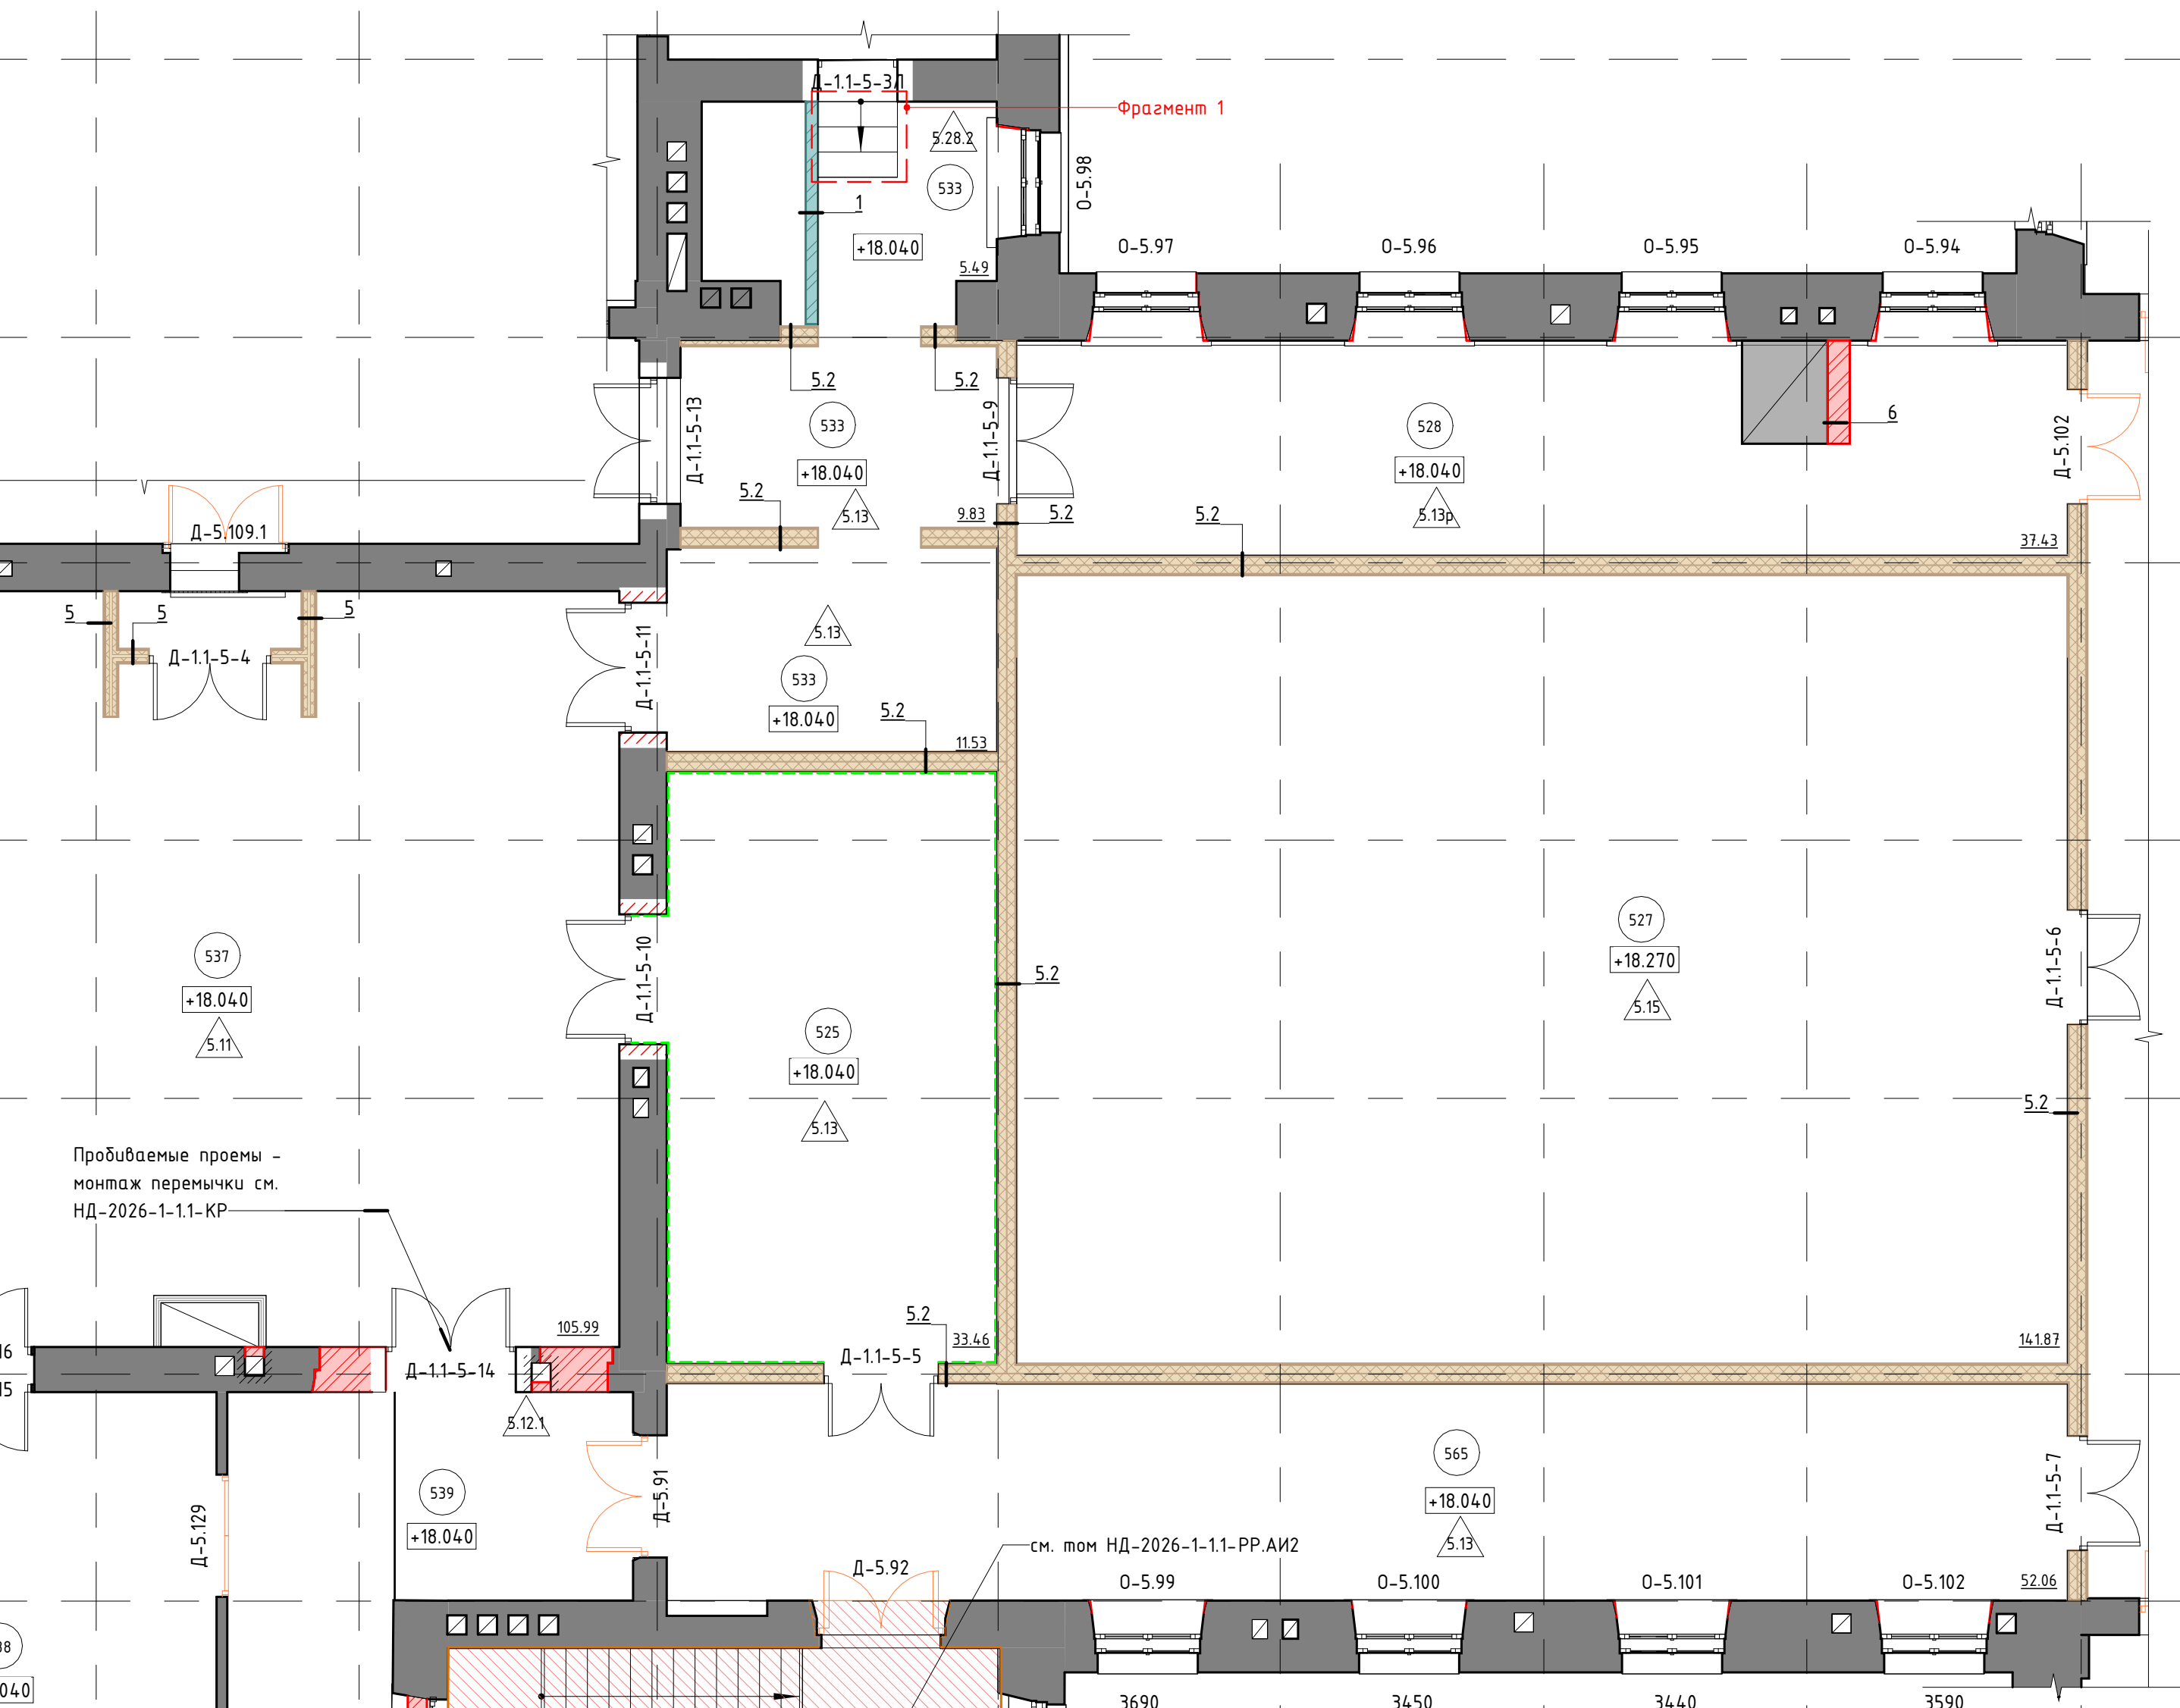

Номер пом.	Тип пола	Схема пола	
5			
537, 540, 544, 546	5.11	Металлическая балка из листа $t=8$ и уголков 60×60, $h=400$ мм	1. Вост. 2. Подп. 15 мм 3. Дой. Суше 4. Ла. 5. Кле. ($\rho=35$) 6. Шт.
538	5.12	Балка 250x220, шаг 1320	1. Вост. 2. Подп. 15 мм Суше 3. Ла. 4. Ба. керам. 5. Су.
539	5.12.1		1. Чис. 2. Подп. 15 мм 3. Ст. мм 4. Ар. 5. За. 6. Су.
524, 525, 526, 528, 530, 531, 533, 565	5.13	Балка 300x200, шаг 1400	1. Чис. 2. Подп. 15 мм Суше 3. Ла. 4. Ба. 5. Пр. 6. Су.
524, 525, 526, 528, 530, 531, 533, 565	5.13p	Балка 300x200, шаг 1400	1. Вост. 2. Подп. 15 мм Суше 3. Ла. 4. Ба. 5. Пр. 6. Су.
527	5.15	Акустический шов	1. На. 2. Ст. мм 3. Ар. 4. П. 5.