


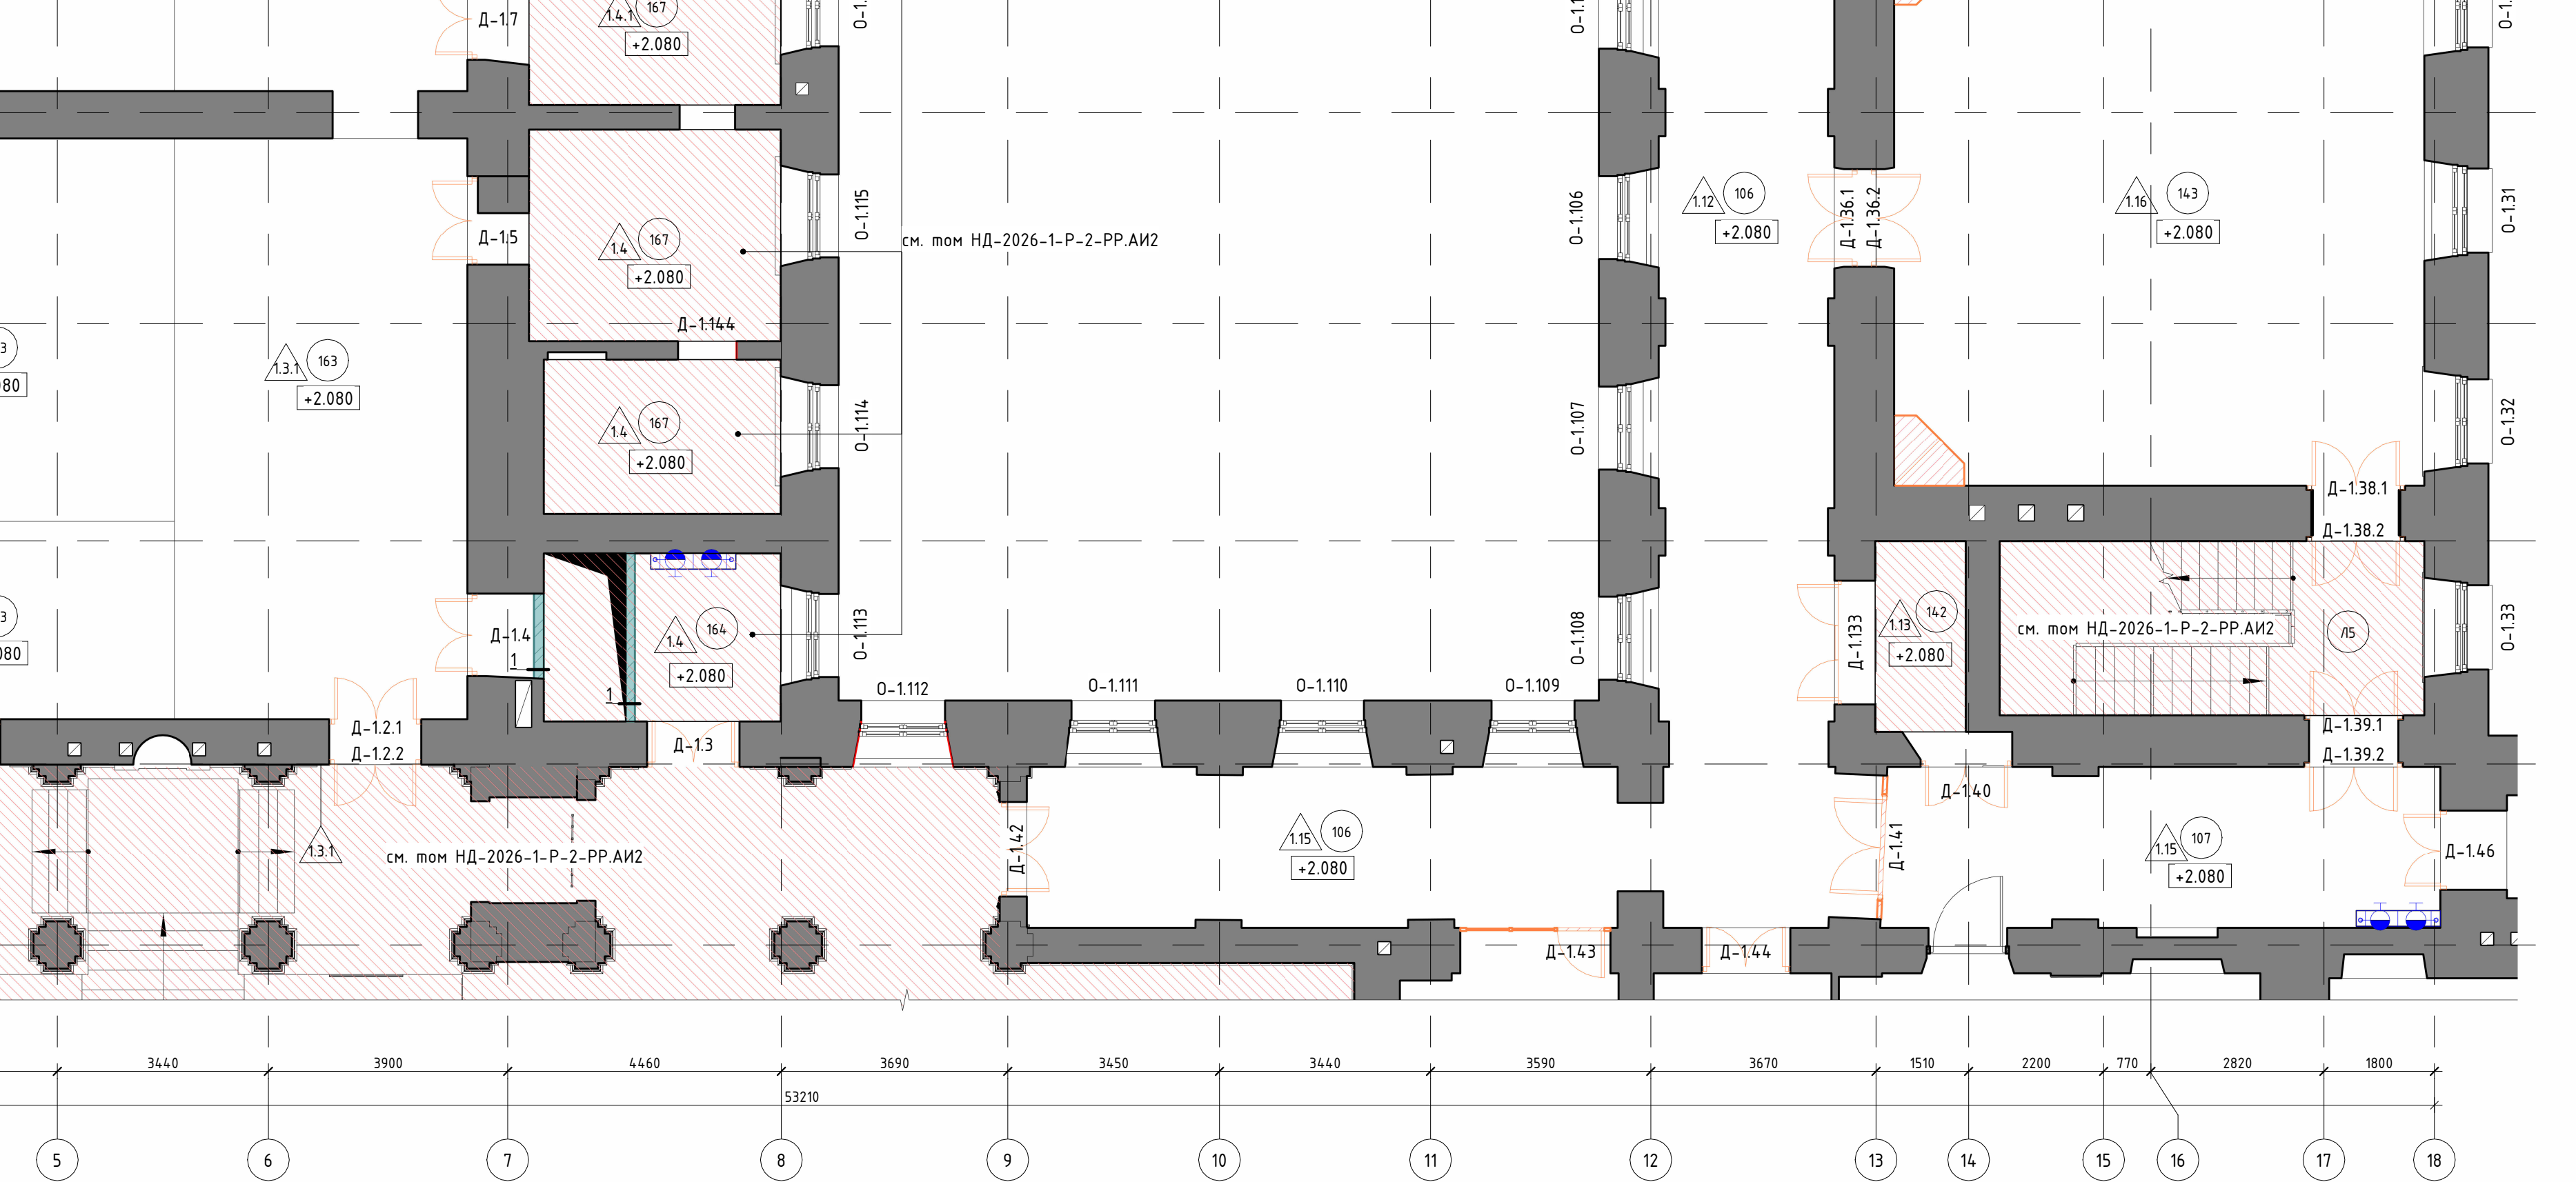

Условные обозначения:

1 - Ось координации

+0,000 - Отметка уровня

- Реставрируемые помещения

- Сохраняемые конструкции

- Пробиваемый проем

- Закладываемый проем

- Рядовая перемычка ГЛ-листами

- Влагостойкая обшивка КНАУФ-листами

- Огнестойкая обшивка КНАУФ-листами

- Перегородка

- Смешанная перегородка

- Сборная конструкция