


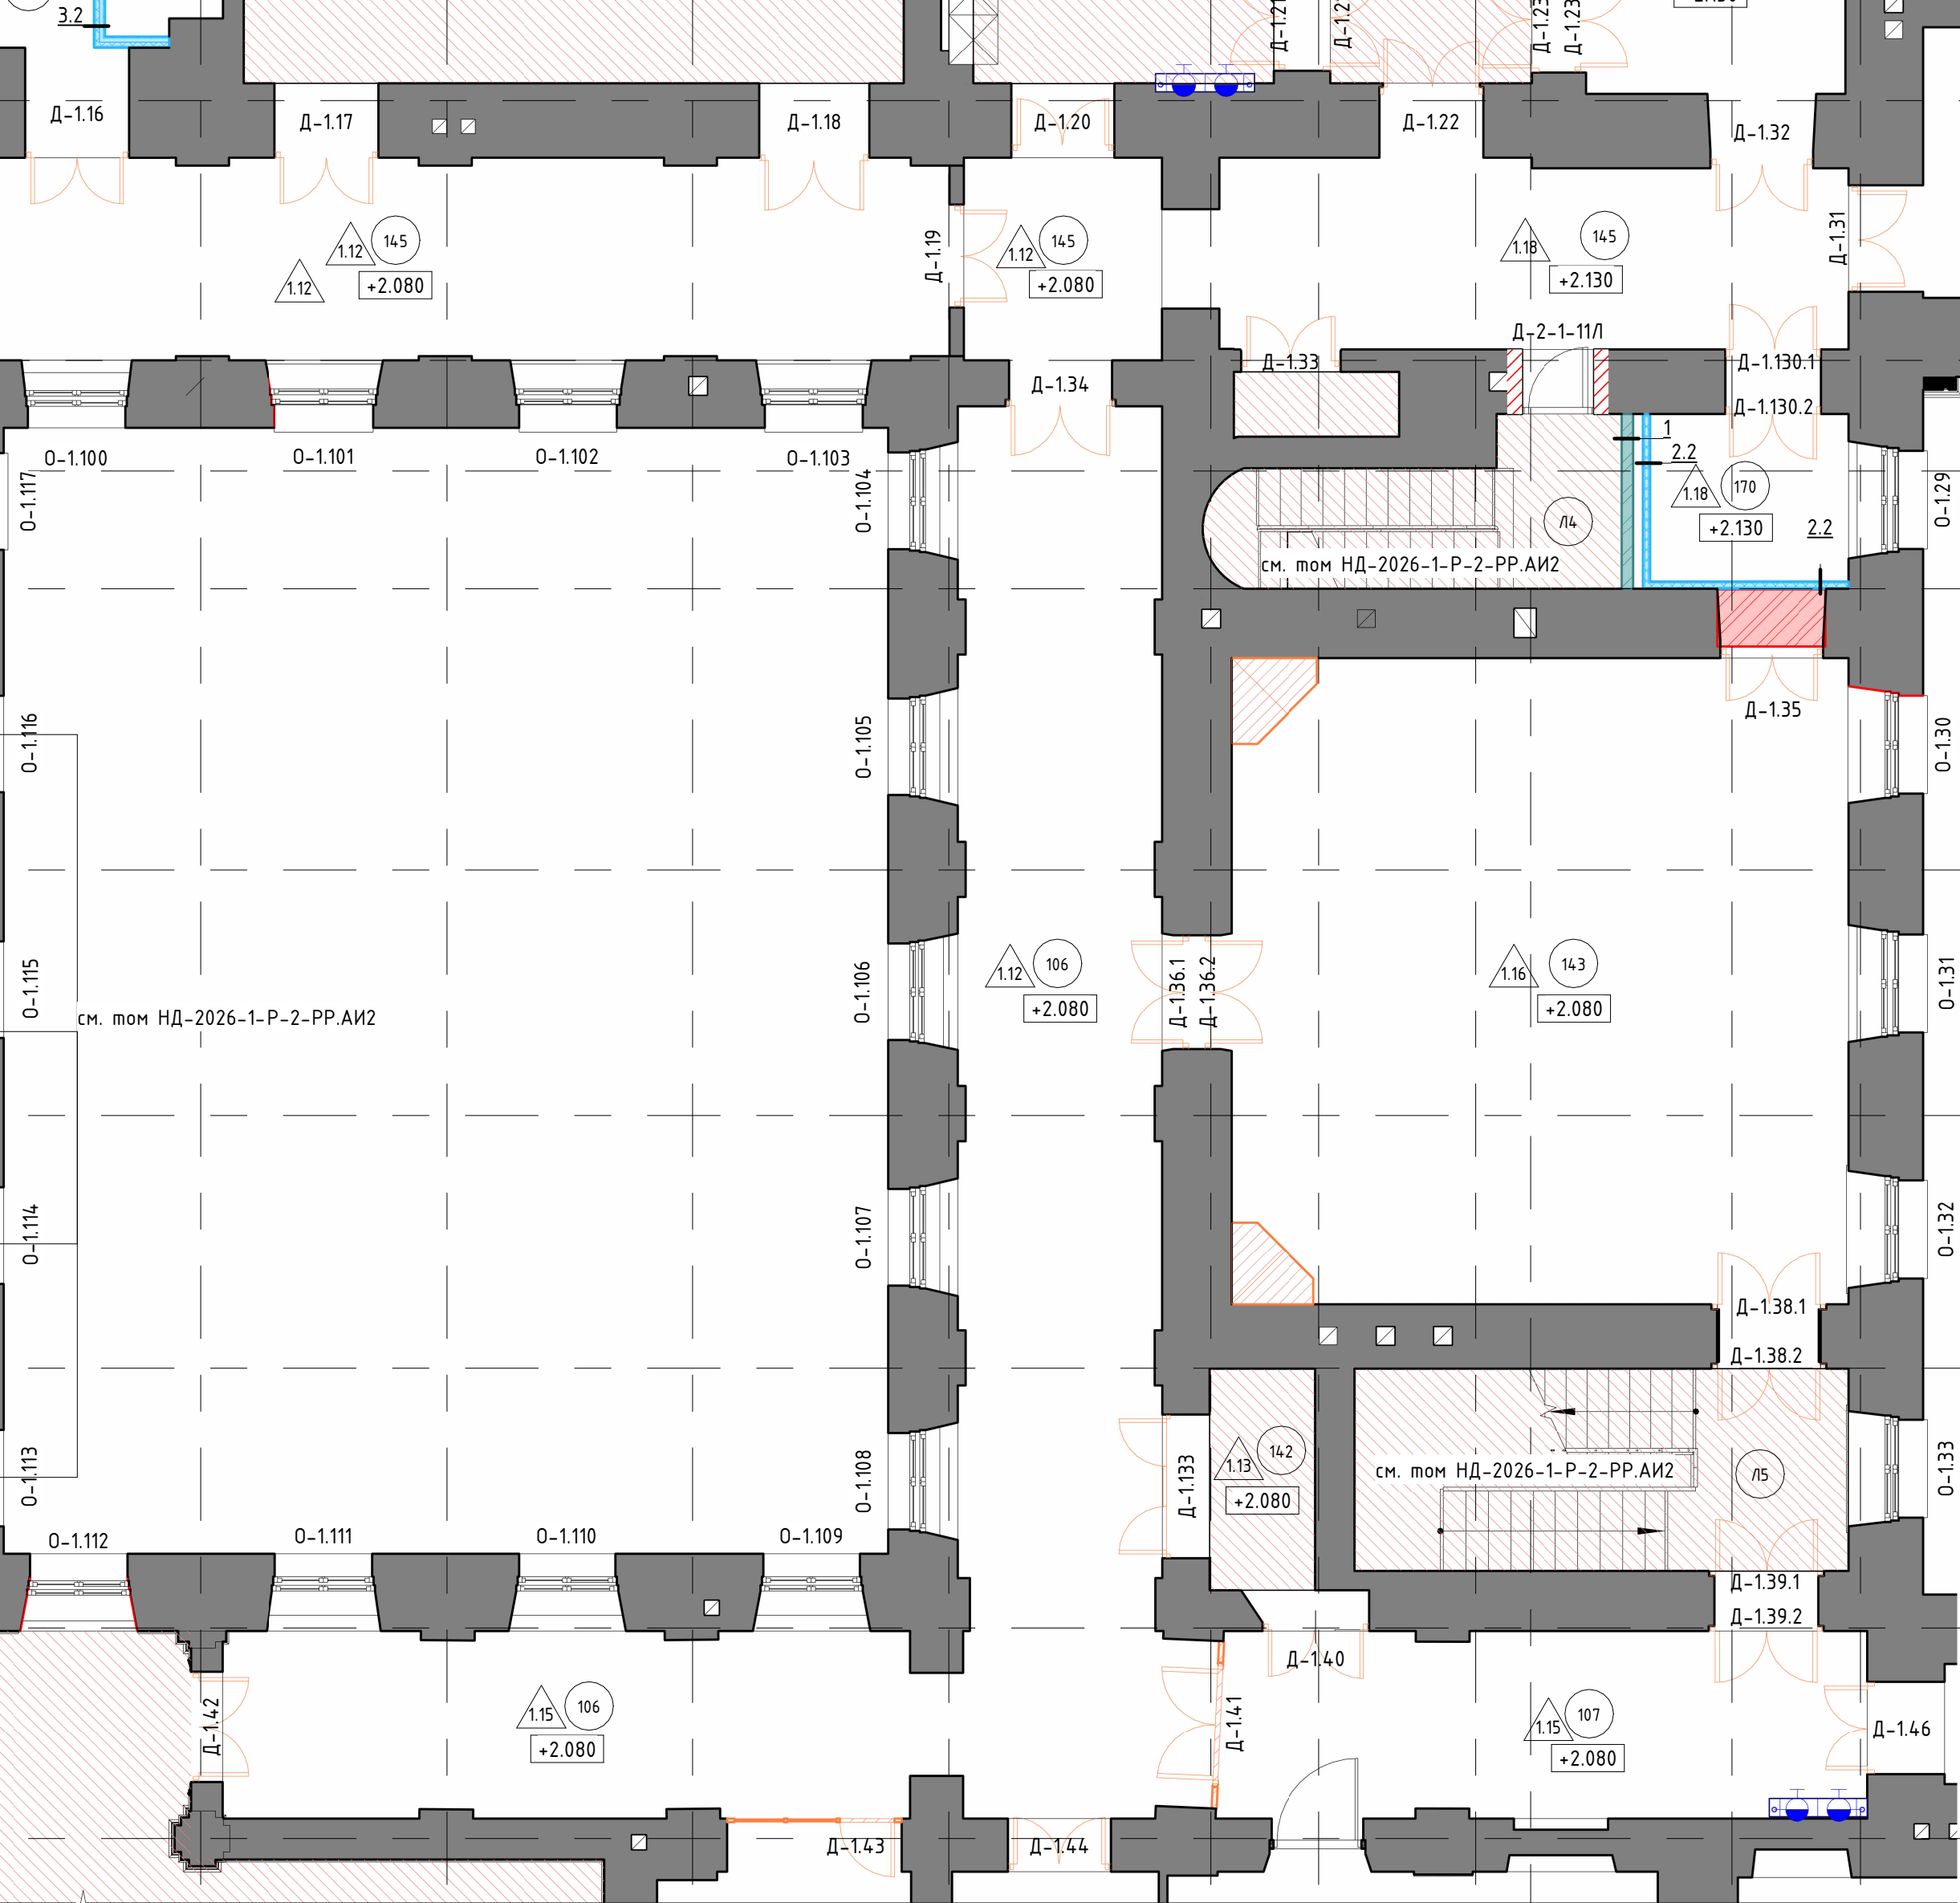

Экспликация помещений фрагмента 1 этажа в осях 1-20/П-Ю

Номер	Имя	Площадь, кв. м.	Кат. пом.
106	Коридор	81.37	
107	Коридор	24.04	
142	ПЧИ	4.62	В4
143	Репетиторий	78.37	
145	Коридор	111.52	
147	Комната отдыха оркестрантов	33.97	
149	Артистическая	38.75	
150	Комната дирижера	14.15	
152	Коридор	14.39	
153	Буфет на 34 посадочных места	83.92	
154	Коридор	7.06	
155	С/У М	3.27	
156	С/У М	2.69	
157	С/У Ж	11.50	
158	ПЧИ	2.14	В4
159	Выставочное пространство	127.50	
160	Выставочное пространство	82.51	
161	Выставочное пространство	9.87	
163	Фойе	185.19	
164	Коридор	6.48	
167	Помещение персонала	37.53	
170	Универсальная кабина МГН	6.55	
175	Моечная столовой посуды	14.70	
176	Кладовая чистой посуды	9.09	
Л1	Лестничная клетка (Тип ЛК: Л2)	25.69	
Л3	Технологическая лестница	8.52	
Л4	Технологическая лестница	11.00	
Л5	Лестничная клетка (Тип ЛК: Л2)	19.67	

1056.06

Д-1.8

Д-1.9

Д-1.10

Д-1.11

Д-1.12

Д-1.13

Д-1.14.2

Д-1.15

Д-1.16

Д-1.17

Д-1.18

Д-1.19

Д-1.20

Д-1.21.1

Д-1.21.2

Д-1.22

Д-1.23.1

Д-1.23.2

Д-1.25

Д-1.31

Д-1.32

Д-1.33

Д-1.34

Д-1.35