


в осях 1-20/П-Ю

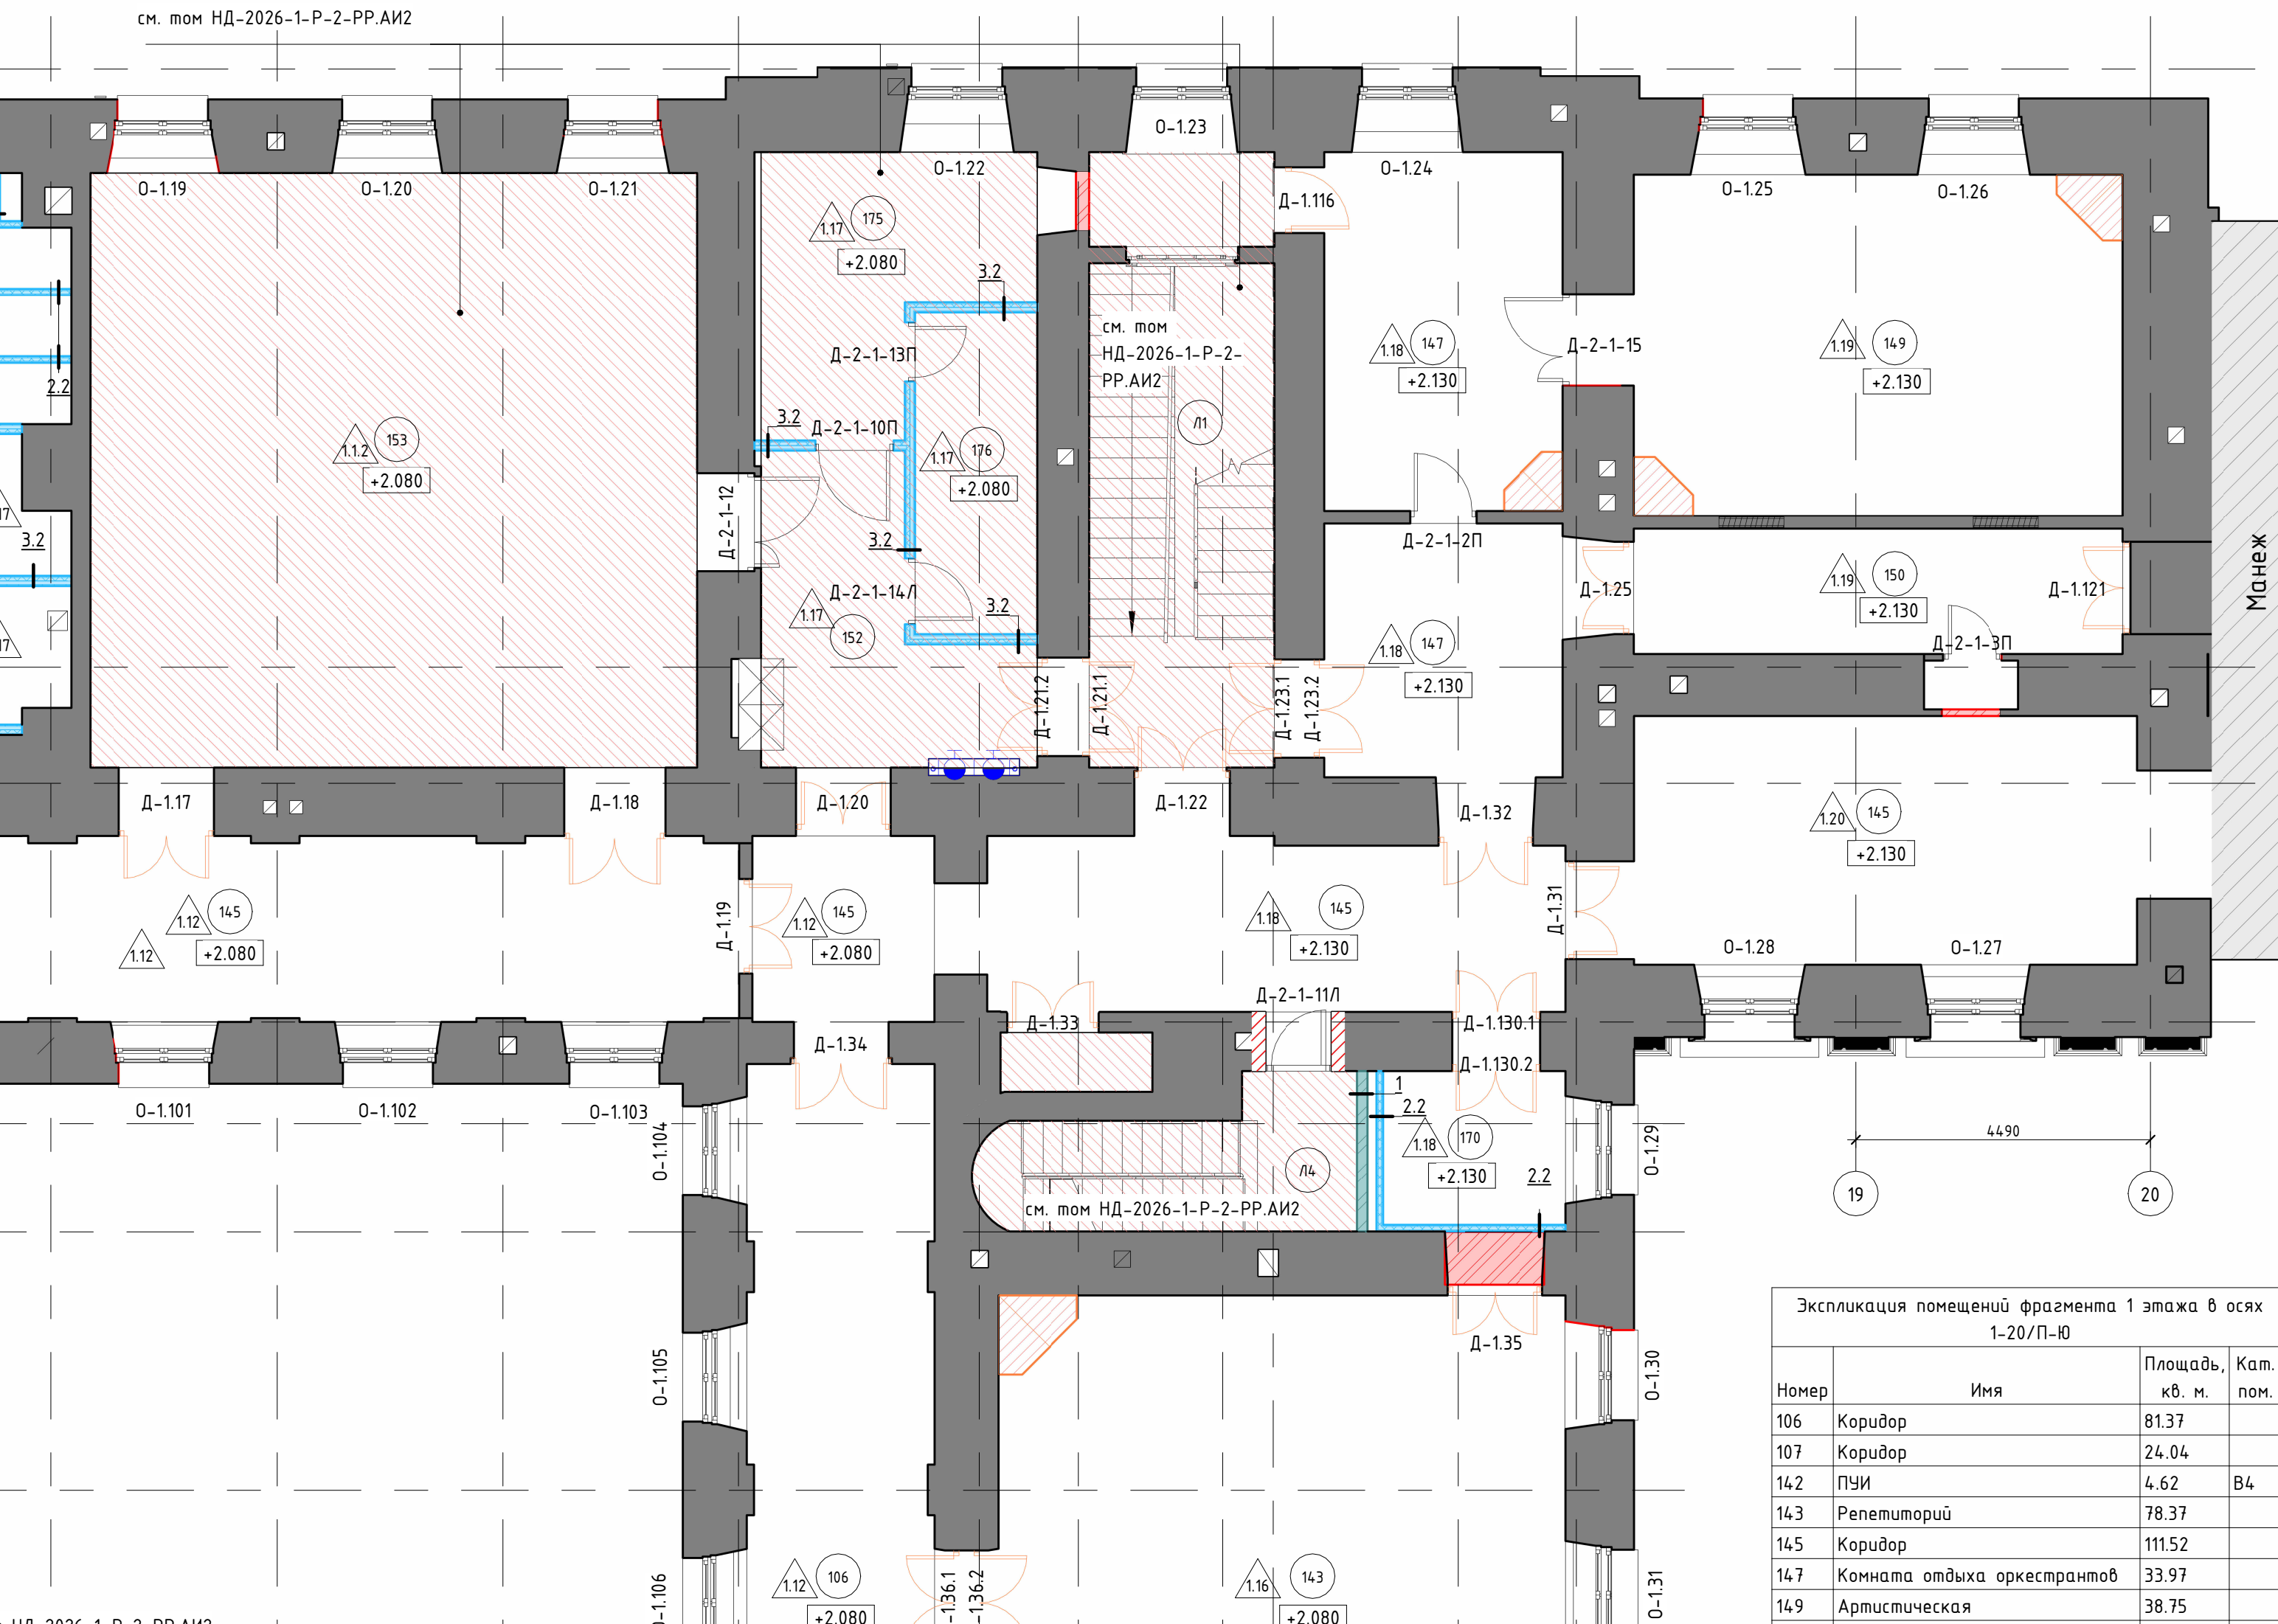

Экспликация помещений фрагмента 1 этажа в осях 1-20/П-Ю			
Номер	Имя	Площадь, кв. м.	Кат. пом.
106	Коридор	81.37	
107	Коридор	24.04	
142	ПУИ	4.62	В4
143	Репетиторий	78.37	
145	Коридор	111.52	
147	Комната отдыха оркестрантов	33.97	
149	Артистическая	38.75	

Марка дверного заполнения	Обозначение
Д-1.1.1	См. том НД-2026-1-2-В
Д-1.1.2	См. том НД-2026-1-2-В
Д-1.2.1	См. том НД-2026-1-2-В
Д-1.2.2	См. том НД-2026-1-2-В
Д-1.3	См. том НД-2026-1-2-В
Д-1.4	См. том НД-2026-1-2-В
Д-1.5	См. том НД-2026-1-2-В
Д-1.7	См. том НД-2026-1-2-В
Д-1.8	См. том НД-2026-1-2-В
Д-1.9	См. том НД-2026-1-2-В
Д-1.10	См. том НД-2026-1-2-В
Д-1.11	См. том НД-2026-1-2-В
Д-1.12	См. том НД-2026-1-2-В
Д-1.13	См. том НД-2026-1-2-В
Д-1.14.2	См. том НД-2026-1-2-В
Д-1.15	См. том НД-2026-1-2-В
Д-1.16	См. том НД-2026-1-2-В
Д-1.17	См. том НД-2026-1-2-В
Д-1.18	См. том НД-2026-1-2-В
Д-1.19	См. том НД-2026-1-2-В
Д-1.20	См. том НД-2026-1-2-В