


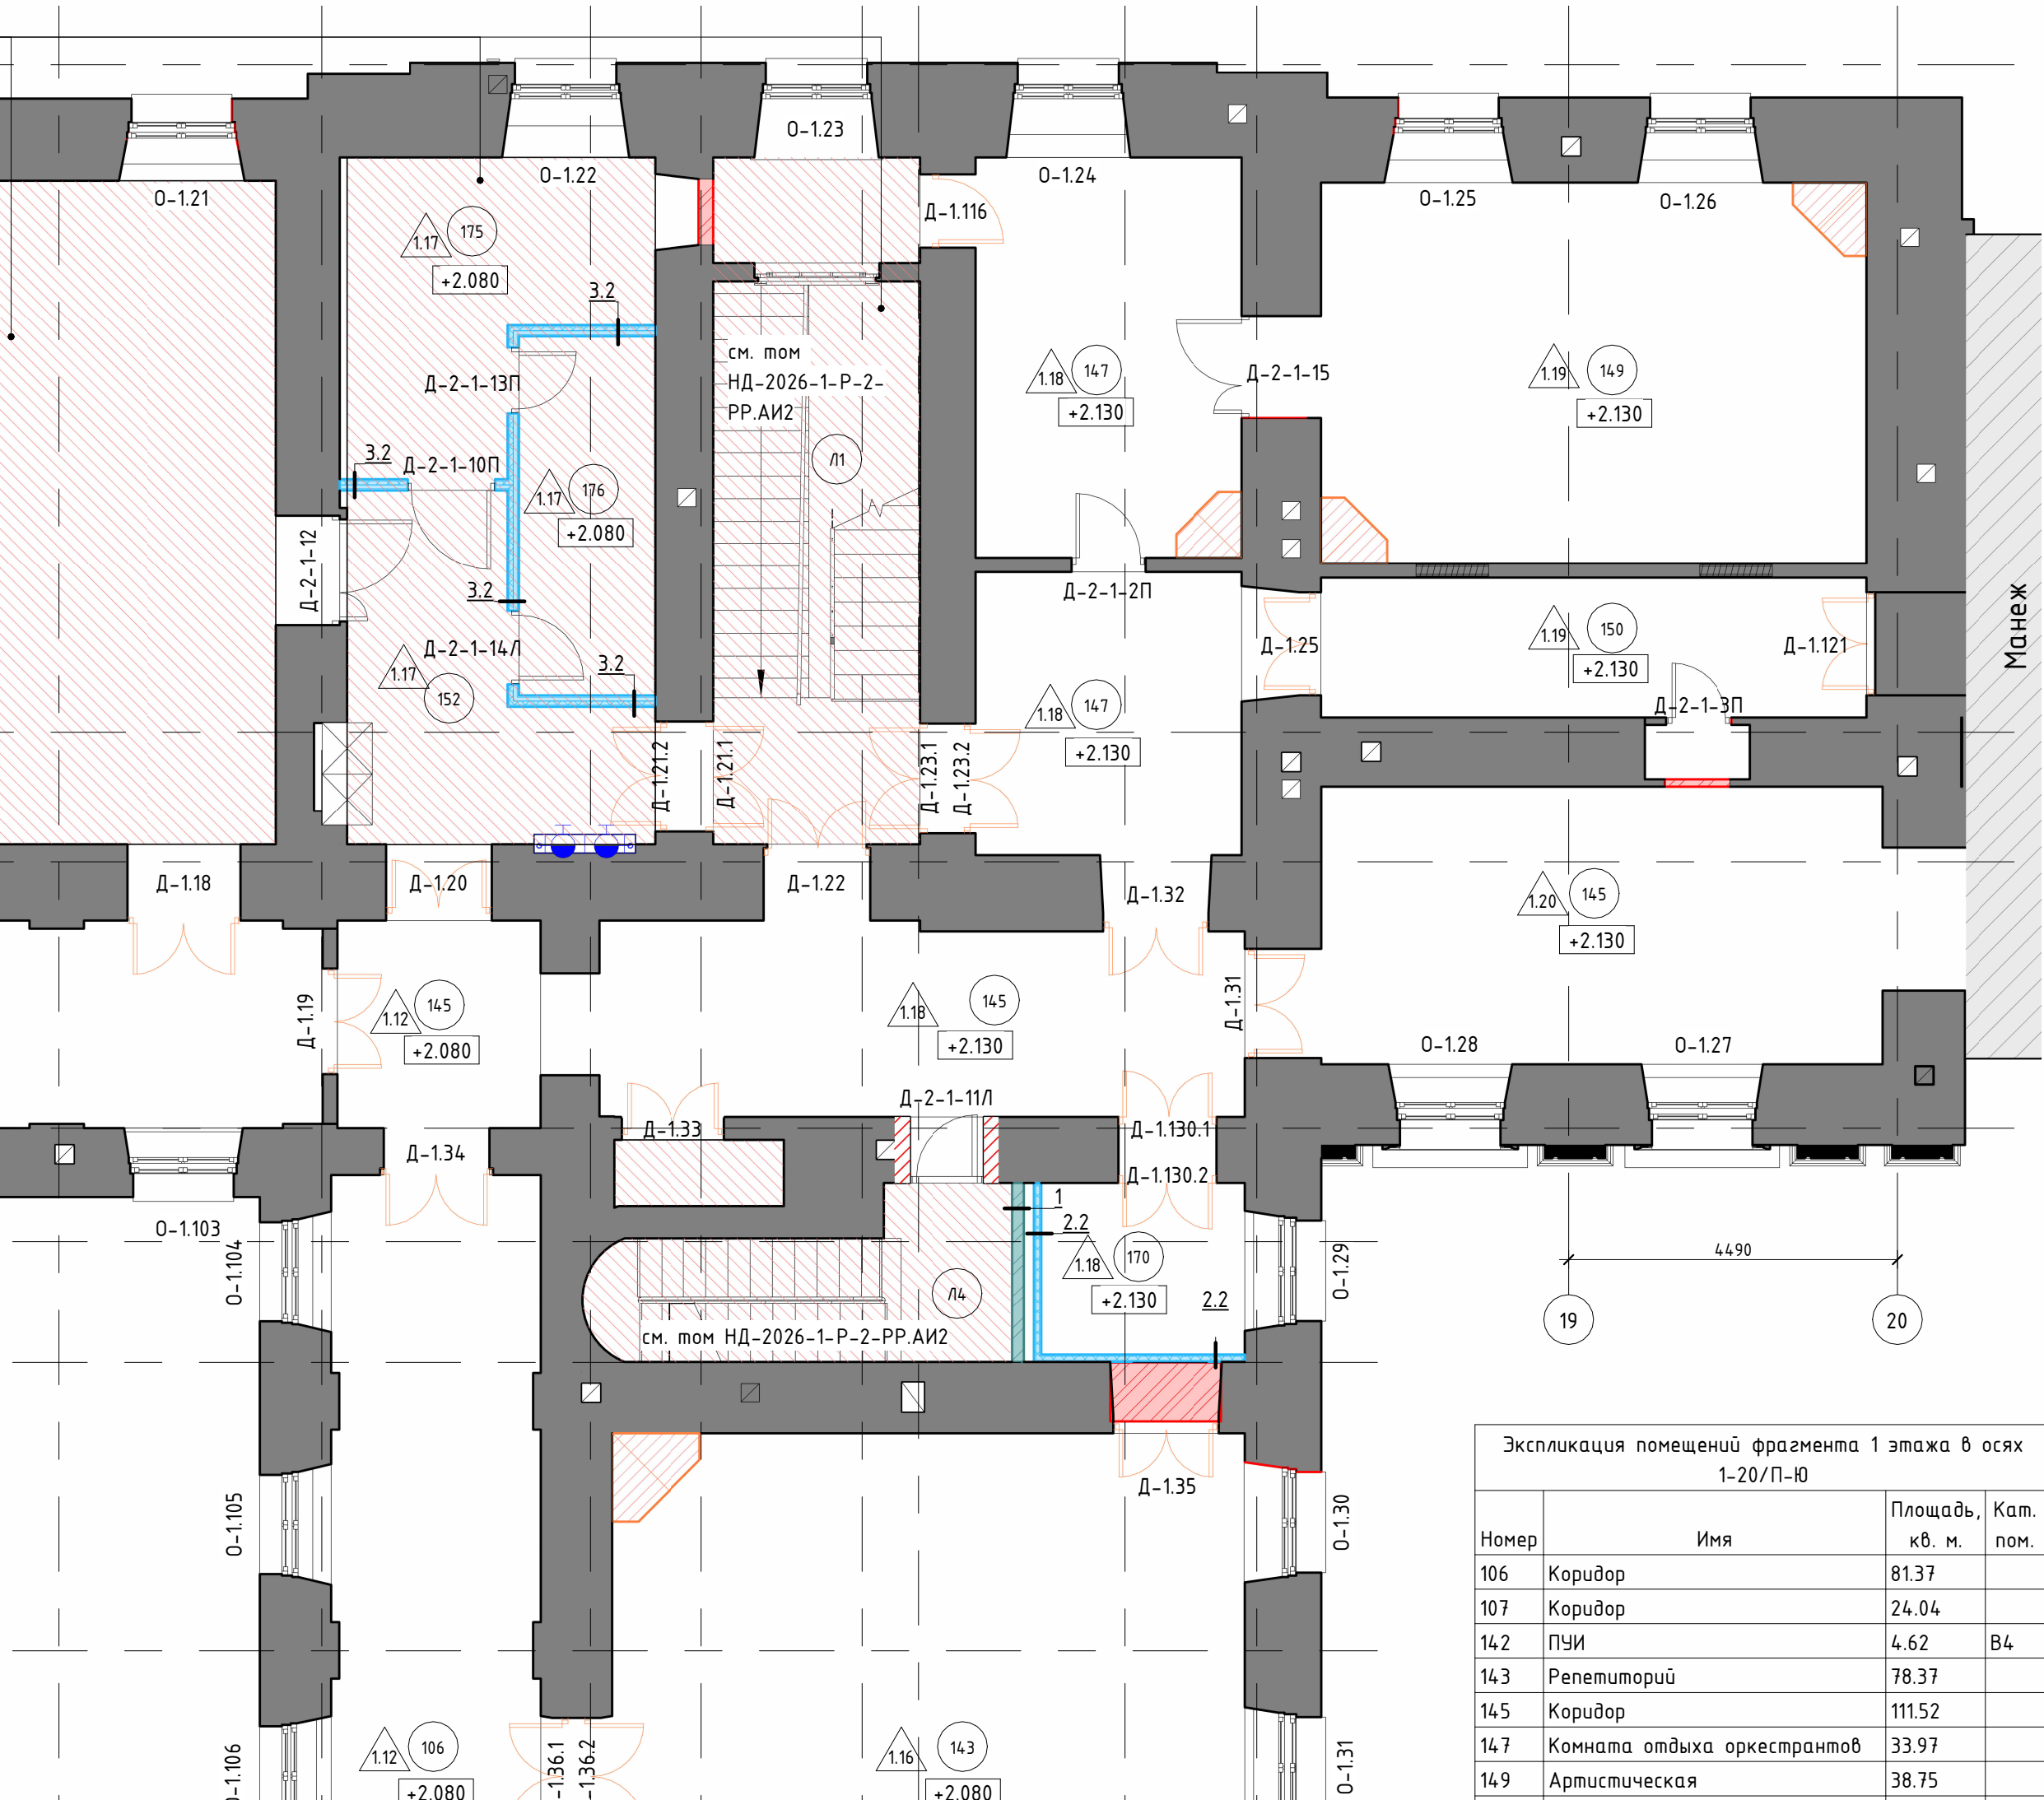

Экспликация помещений фрагмента 1 этажа в осях 1-20/П-Ю			
Номер	Имя	Площадь, кв. м.	Кат. пом.
106	Коридор	81.37	
107	Коридор	24.04	
142	ПУИ	4.62	В4
143	Репетиторий	78.37	
145	Коридор	111.52	
147	Комната отдыха оркестрантов	33.97	
149	Артистическая	38.75	

Спецификация					
Марка дверного заполнения	Обозначение	Наименование	Габариты проем по полотну		Кол-во
			Высота, мм	Ширина, мм	
Д-1.1.1	См. том НД-2026-1-2-РР.Д В	См. том НД-2026-1-2-Р Р.ДВ	2670	1340	1
Д-1.1.2	См. том НД-2026-1-2-РР.Д В	См. том НД-2026-1-2-Р Р.ДВ	2670	1340	1
Д-1.2.1	См. том НД-2026-1-2-РР.Д В	См. том НД-2026-1-2-Р Р.ДВ	2570	1340	1
Д-1.2.2	См. том НД-2026-1-2-РР.Д В	См. том НД-2026-1-2-Р Р.ДВ	2670	1340	1
Д-1.3	См. том НД-2026-1-2-РР.Д В	См. том НД-2026-1-2-Р Р.ДВ	2670	1340	1
Д-1.4	См. том НД-2026-1-2-РР.Д В	См. том НД-2026-1-2-Р Р.ДВ	2720	1190	1
Д-1.5	См. том НД-2026-1-2-РР.Д В	См. том НД-2026-1-2-Р Р.ДВ	2720	1290	1
Д-1.7	См. том НД-2026-1-2-РР.Д В	См. том НД-2026-1-2-Р Р.ДВ	2720	1190	1
Д-1.8	См. том НД-2026-1-2-РР.Д В	См. том НД-2026-1-2-Р Р.ДВ	2170	1290	1
Д-1.9	См. том НД-2026-1-2-РР.Д В	См. том НД-2026-1-2-Р Р.ДВ	1990	780	1
Д-1.10	См. том НД-2026-1-2-РР.Д В	См. том НД-2026-1-2-Р Р.ДВ	2820	1240	1
Д-1.11	См. том НД-2026-1-2-РР.Д В	См. том НД-2026-1-2-Р Р.ДВ	2720	1290	1
Д-1.12	См. том НД-2026-1-2-РР.Д В	См. том НД-2026-1-2-Р Р.ДВ	2870	1340	1
Д-1.13	См. том НД-2026-1-2-РР.Д В	См. том НД-2026-1-2-Р Р.ДВ	2720	1390	1
Д-1.14.2	См. том НД-2026-1-2-РР.Д В	См. том НД-2026-1-2-Р Р.ДВ	2670	1400	1
Д-1.15	См. том НД-2026-1-2-РР.Д В	См. том НД-2026-1-2-Р Р.ДВ	2720	1290	1
Д-1.16	См. том НД-2026-1-2-РР.Д В	См. том НД-2026-1-2-Р Р.ДВ	2720	1290	1
Д-1.17	См. том НД-2026-1-2-РР.Д В	См. том НД-2026-1-2-Р Р.ДВ	2720	1290	1
Д-1.18	См. том НД-2026-1-2-РР.Д В	См. том НД-2026-1-2-Р Р.ДВ	2720	1390	1
Д-1.19	См. том НД-2026-1-2-РР.Д В	См. том НД-2026-1-2-Р Р.ДВ	2720	1290	1
Д-1.20	См. том НД-2026-1-2-РР.Д В	См. том НД-2026-1-2-Р Р.ДВ	2720	1290	1