


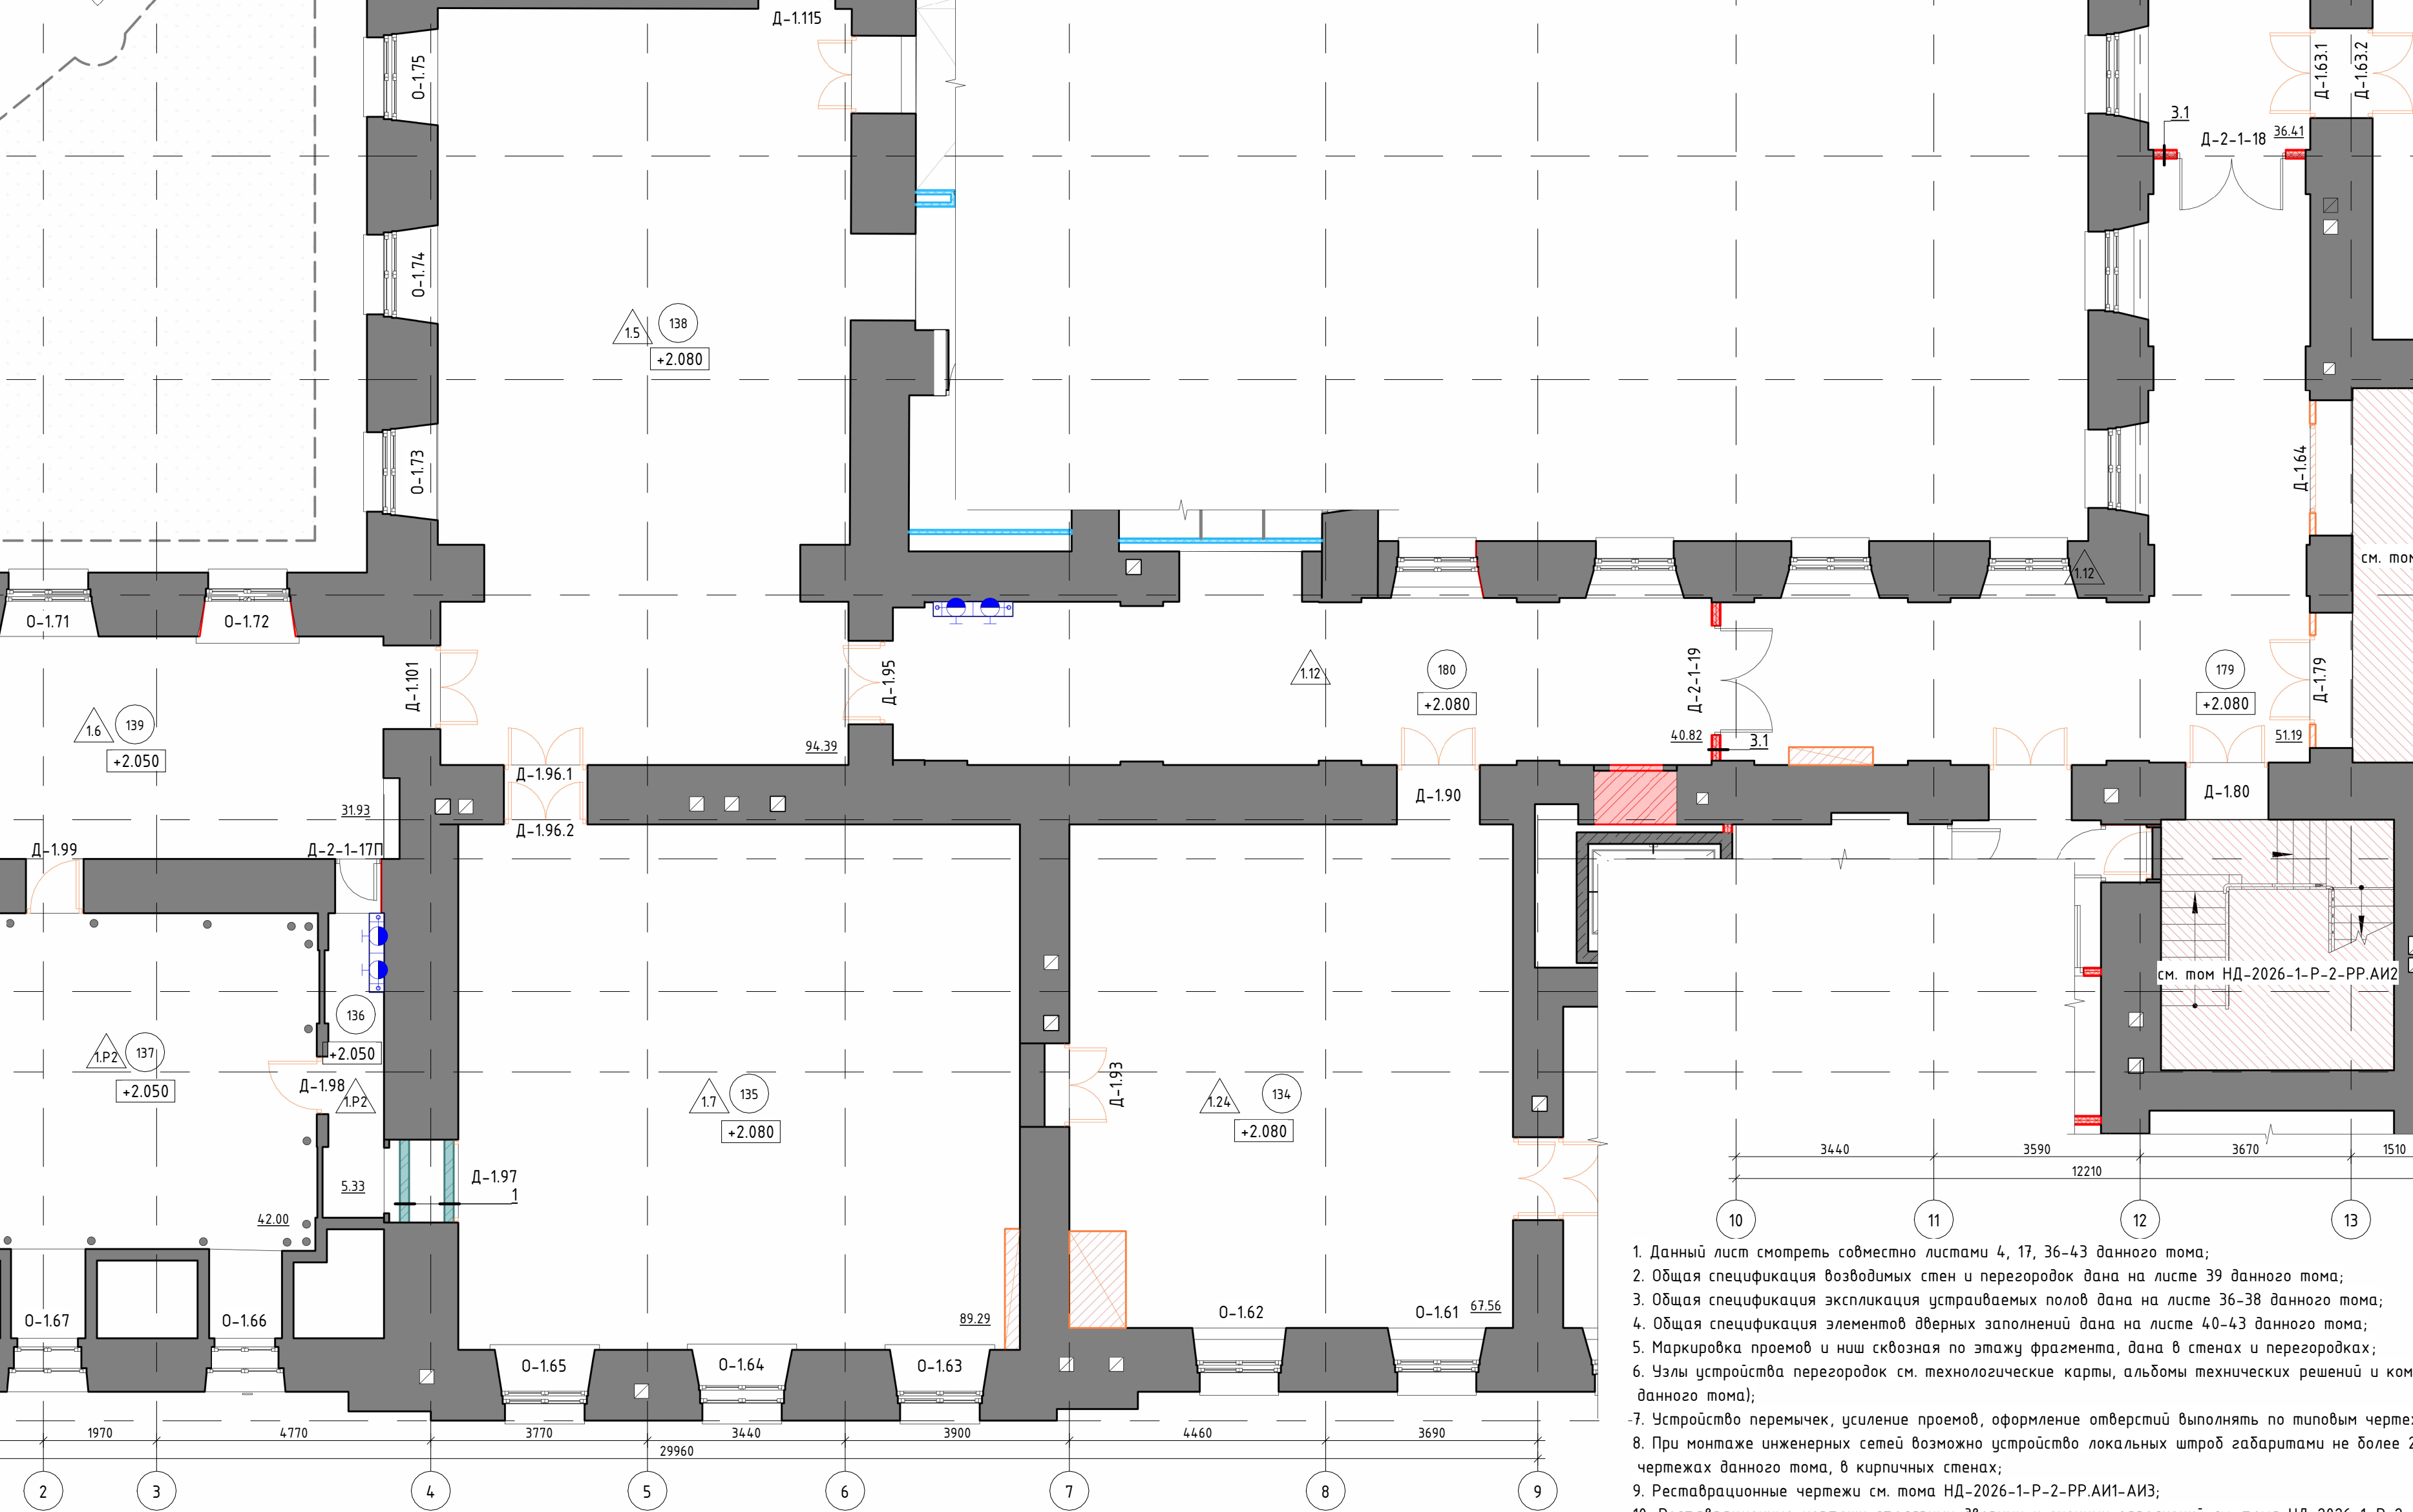

1. Данный лист смотреть совместно листами 4, 17, 36-43 данного тома;
2. Общая спецификация возводимых стен и перегородок дана на листе 39 данного тома;
3. Общая спецификация экспликация устраиваемых полов дана на листе 36-38 данного тома;
4. Общая спецификация элементов дверных заполнений дана на листе 40-43 данного тома;
5. Маркировка проемов и ниш сквозная по этажу фрагмента, дана в стенах и перегородках;
6. Узлы устройства перегородок см. технологические карты, альбомы технических решений и ком. данного тома);
7. Устройство перемычек, усиление проемов, оформление отверстий выполнять по типовым чертежам;
8. При монтаже инженерных сетей возможно устройство локальных штроб габаритами не более 2 см, см. чертежи данного тома, в кирпичных стенах;
9. Реставрационные чертежи см. тома НД-2026-1-Р-2-РР.АИ1-АИЗ;
10. Реставрационные чертежи столярных дверных и оконных заполнений см. тома НД-2026-1-Р-2-