


Согласовано

Взам. инв. №

та

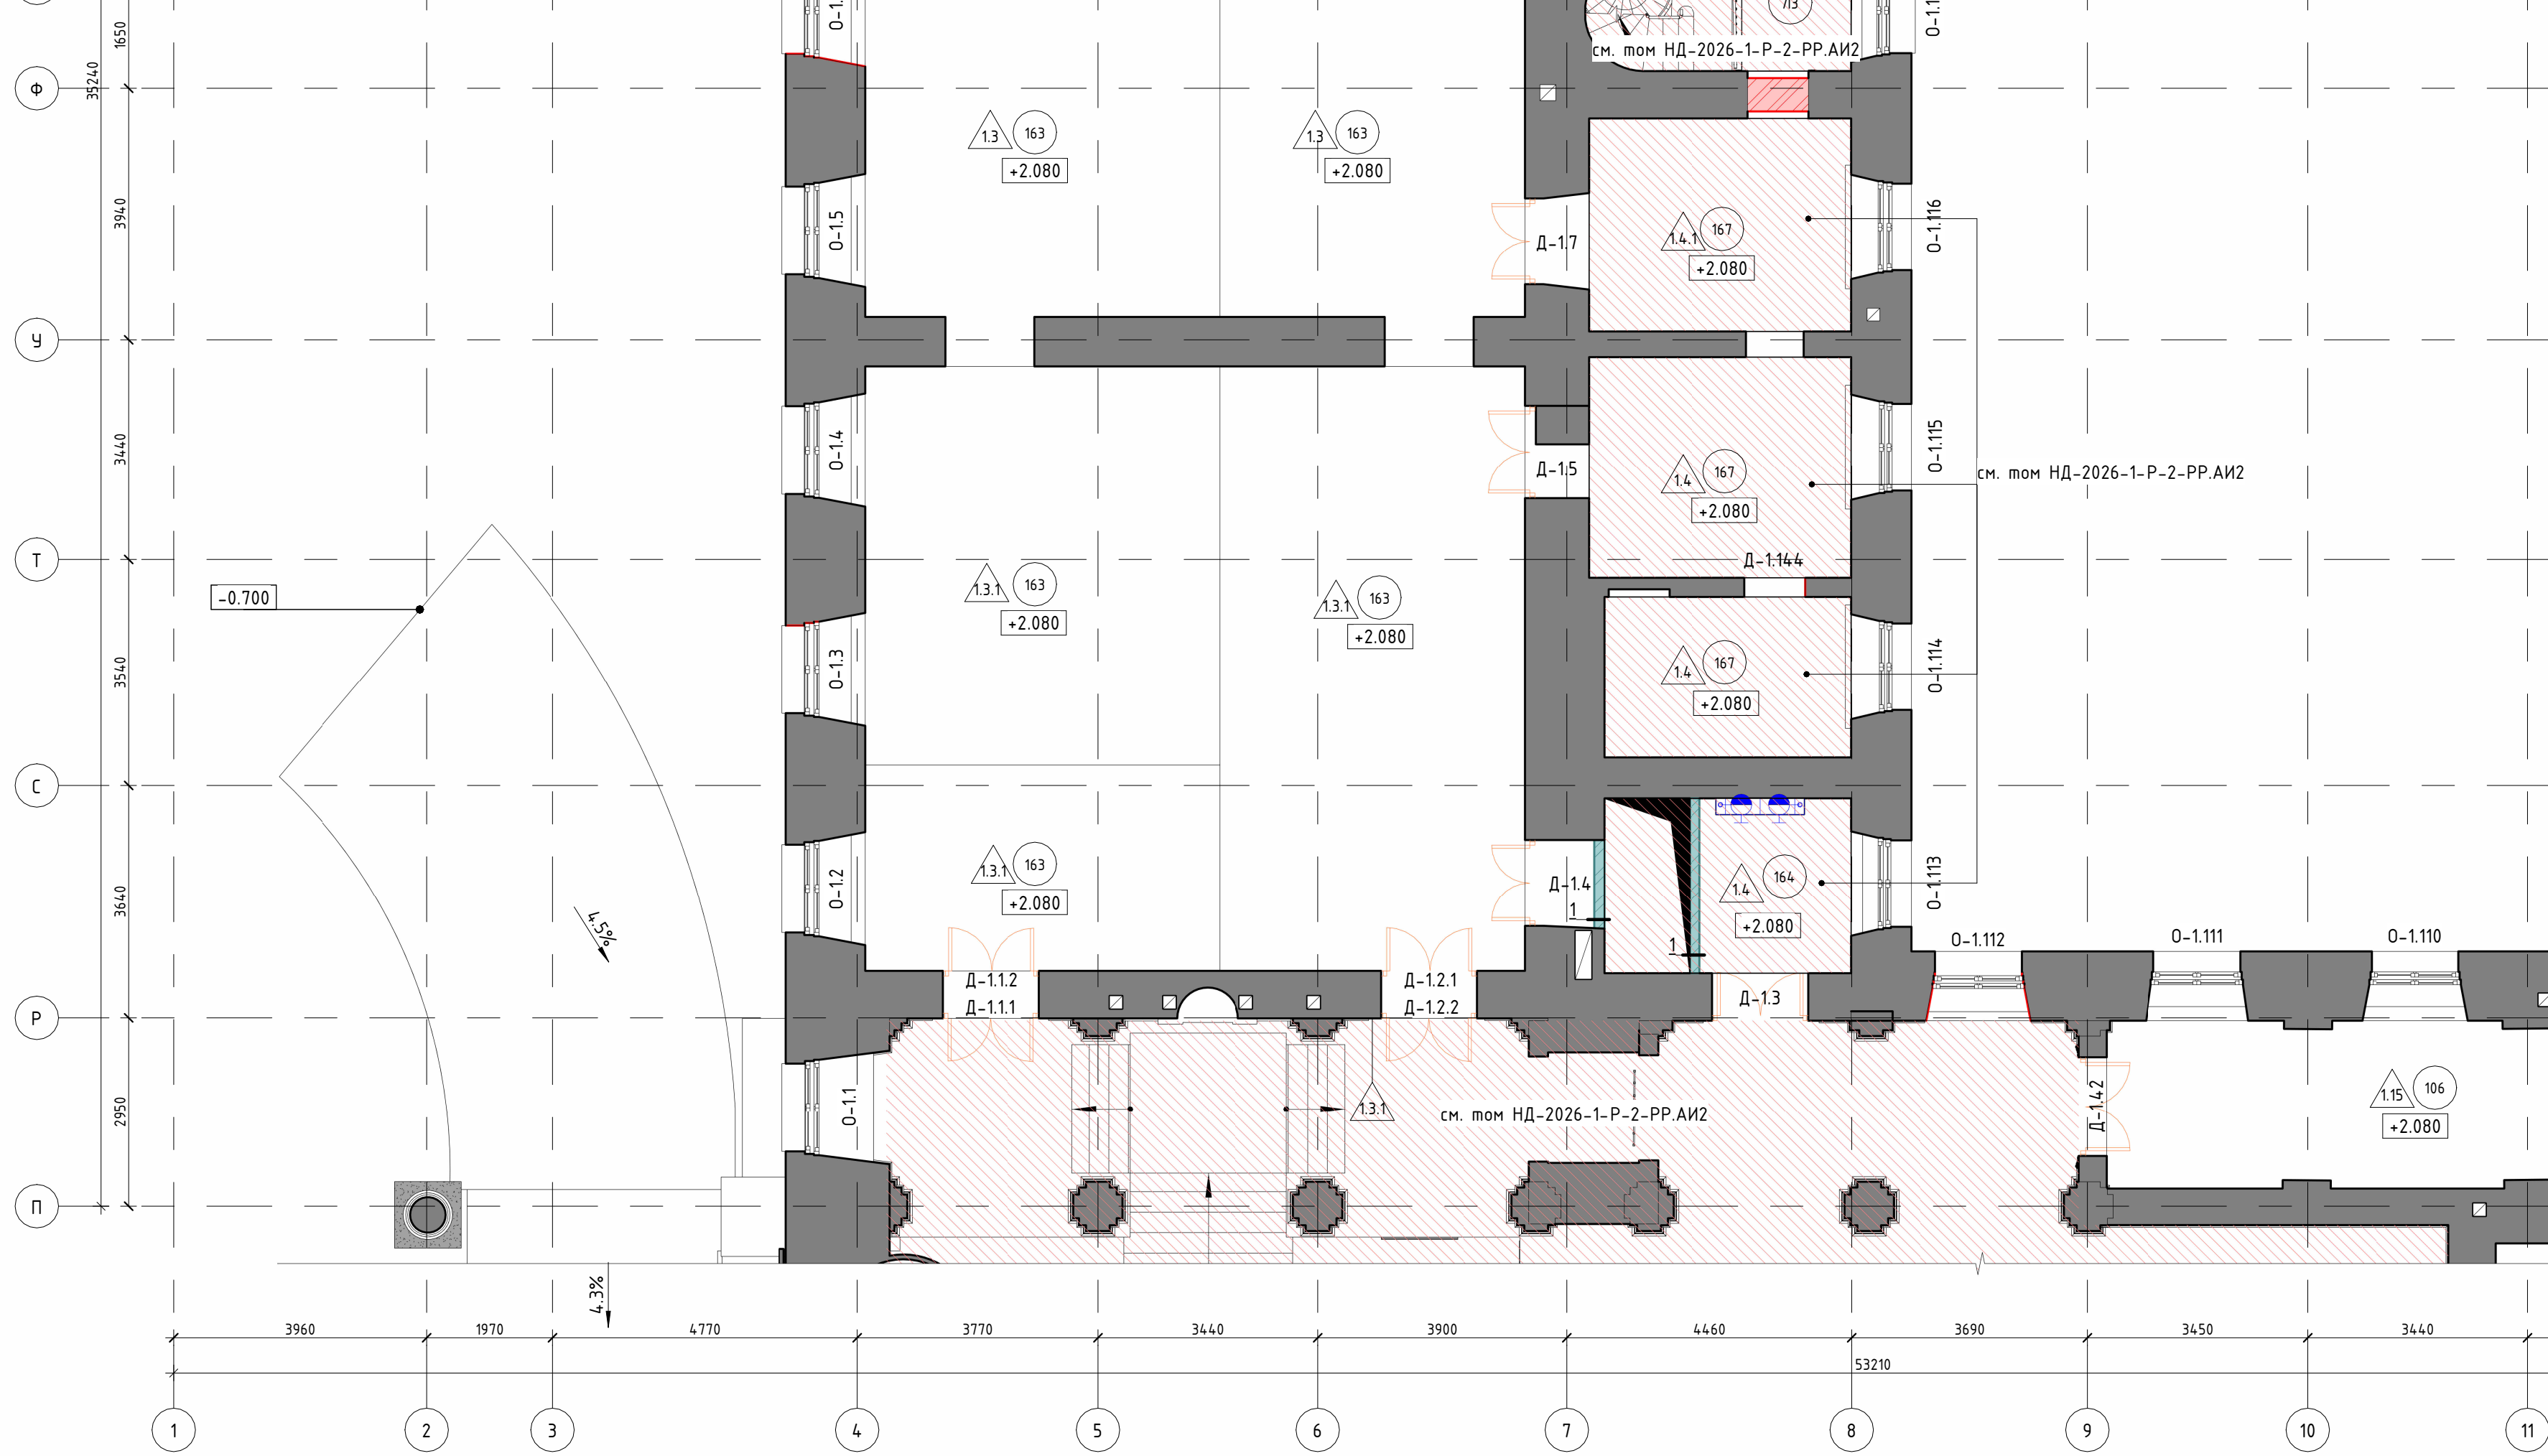

Ведомость возводимых перегородок и стен по фрагменту в осях 1-20/П-Ю 1 этажа			
Марка	Наименование	Площадь, кв. м.	Примечание
1	Перегородка из бетонного камня	9.76	
2.2	КНАУФ перегородка типа Г382	41.10	