


№ подл.	
---------	--

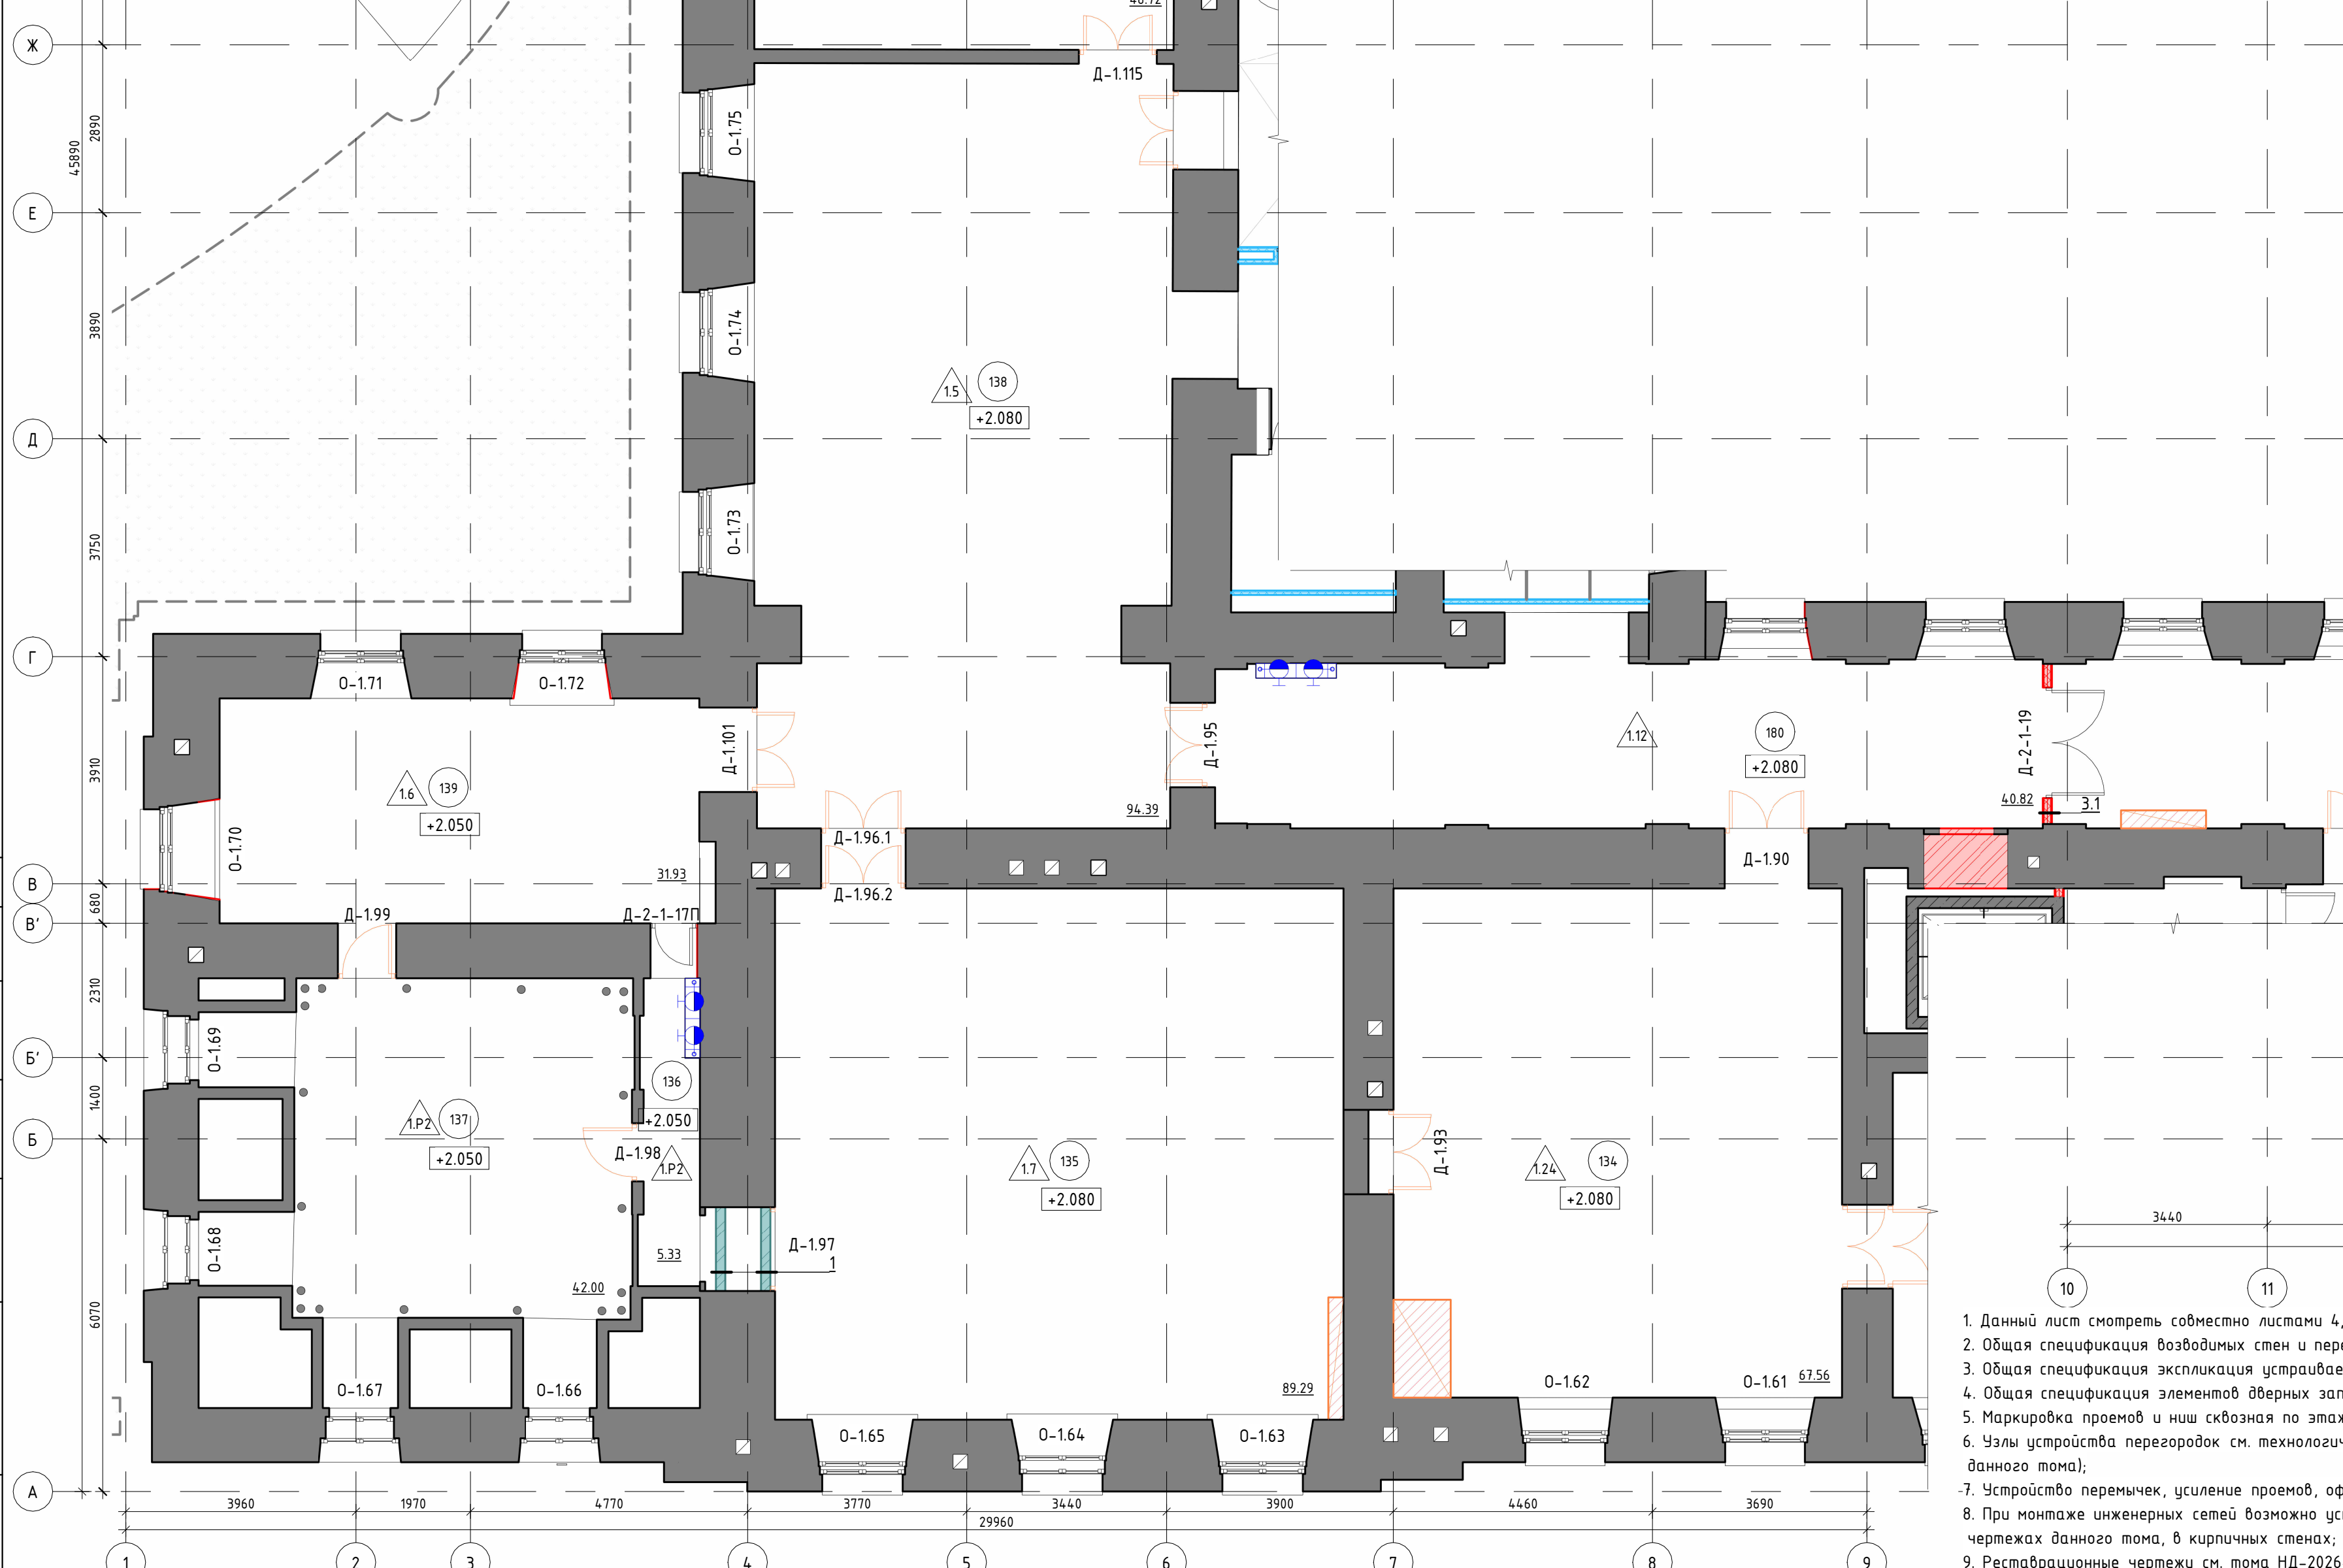

1. Данный лист смотреть совместно листами 4,
2. Общая спецификация возводимых стен и перегородок;
3. Общая спецификация экспликация устраиваемых перегородок;
4. Общая спецификация элементов дверных запорных устройств;
5. Маркировка проемов и ниш сквозная по этажам;
6. Узлы устройства перегородок см. технологические карты данного тома);
- 7. Устройство перемычек, усиление проемов, оконных откосов;
8. При монтаже инженерных сетей возможно использование чертежей данного тома, в кирпичных стенах;
9. Реставрационные чертежи см. тома НД-2026