


Инв. № подл.	Подп. и дата	Взам. инв. №	Согласовано

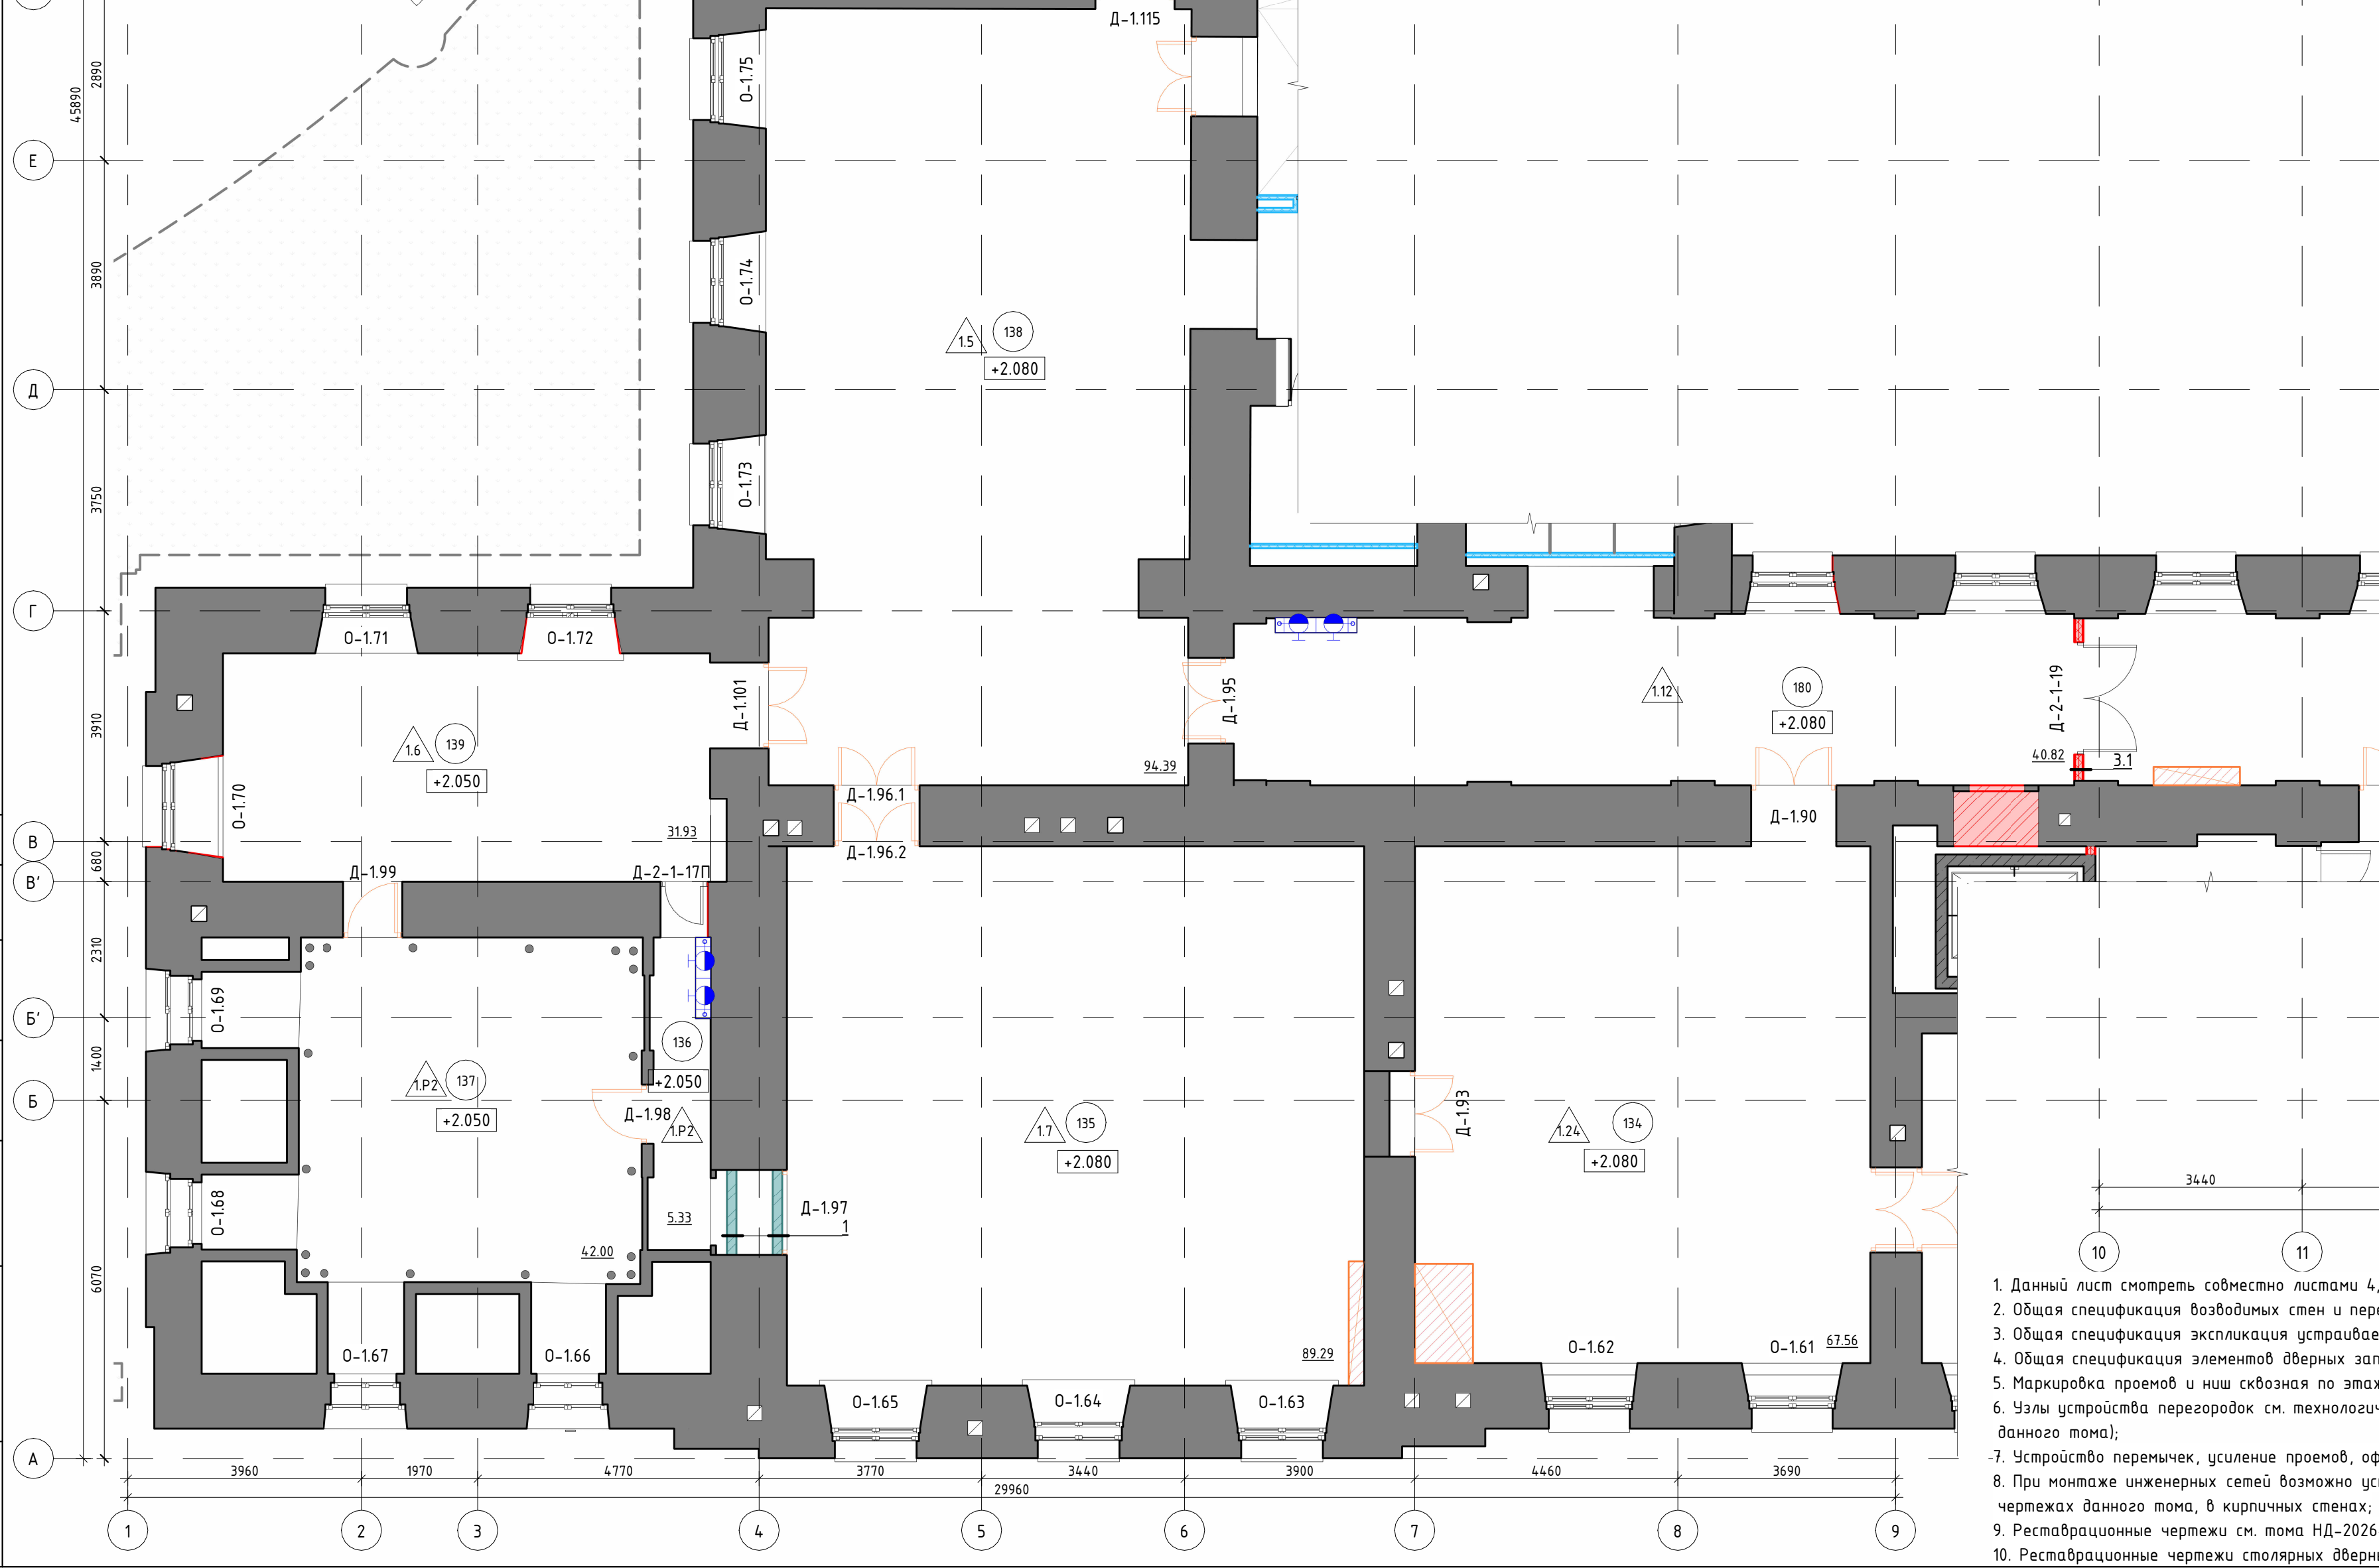

1. Данный лист смотреть совместно листами 4, 5, 6, 7, 8, 9, 10, 11.
2. Общая спецификация возводимых стен и перегородок.
3. Общая спецификация экспликация устраиваемых помещений.
4. Общая спецификация элементов дверных запорных устройств.
5. Маркировка проемов и ниш сквозная по этажу.
6. Узлы устройства перегородок см. технологические карты.
7. Устройство перемычек, усиление проемов, оформление проемов.
8. При монтаже инженерных сетей возможно усиление проемов, см. чертежи данного тома, в кирпичных стенах.
9. Реставрационные чертежи см. тома НД-2026.
10. Реставрационные чертежи столярных дверей.