


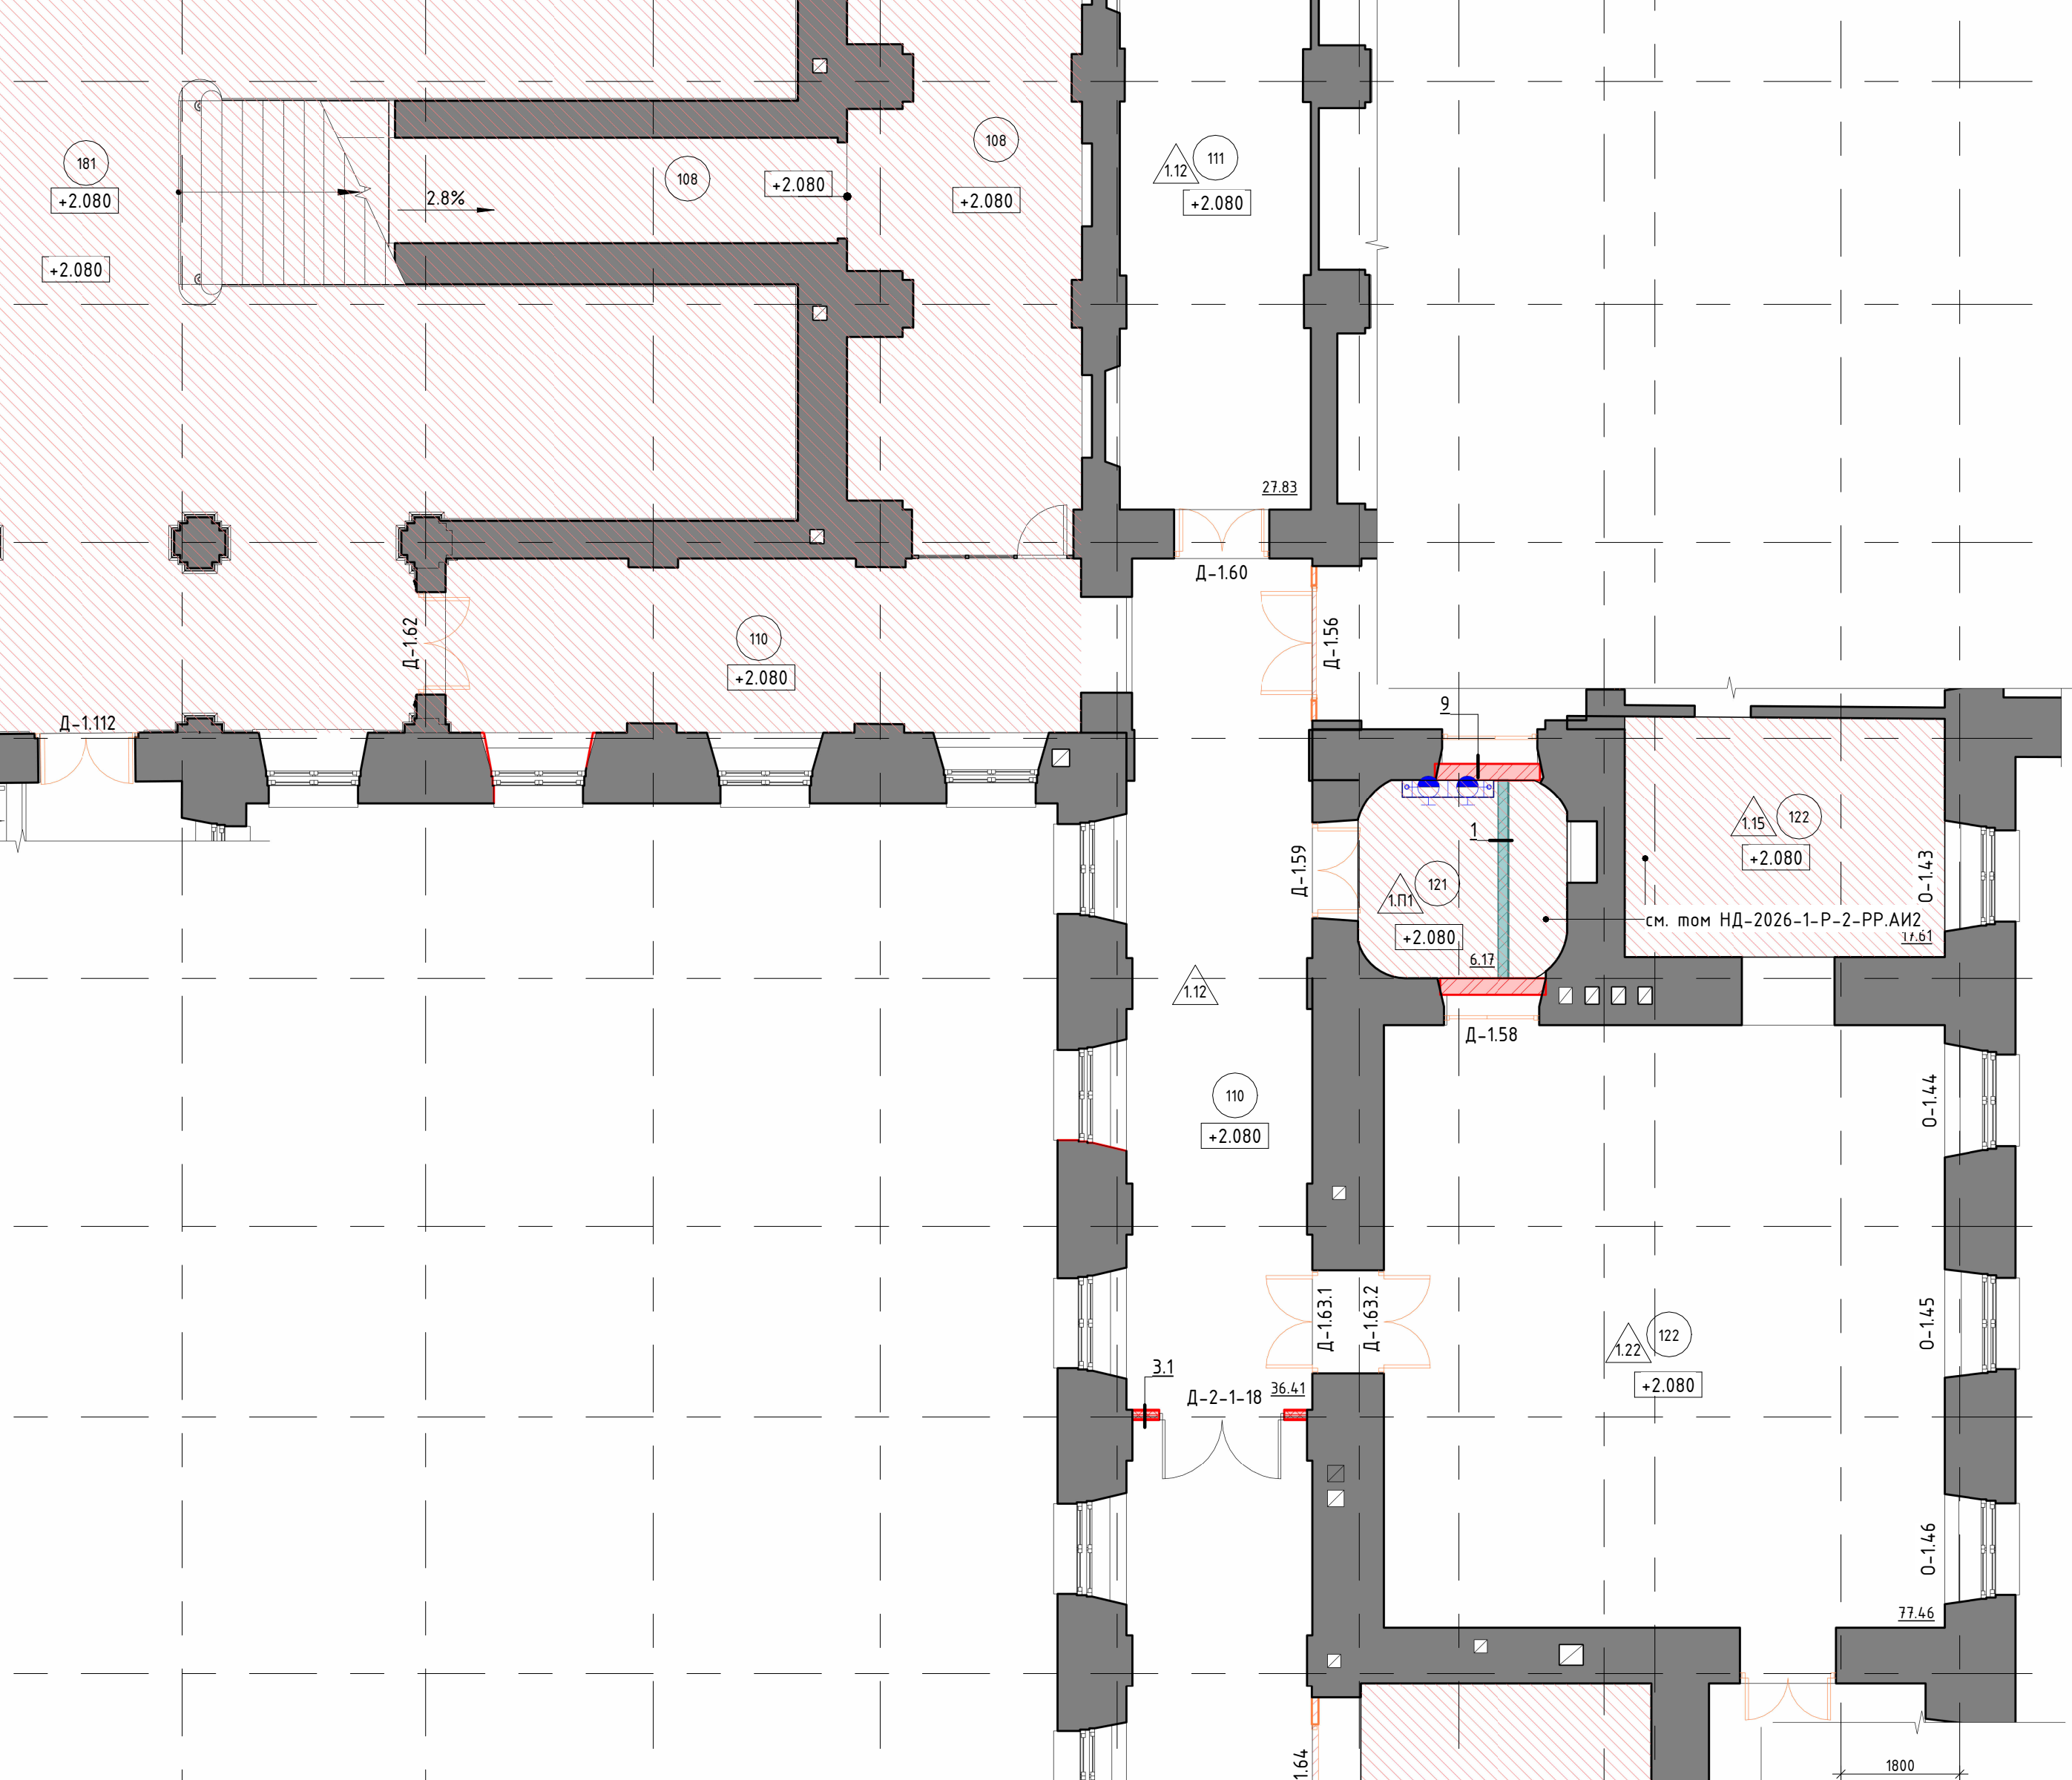

105	Пост охраны	5.49	
108	Помещение для хранения технических средств для обслуживания светильников	41.94	Д
110	Коридор	61.70	
111	Коридор	27.83	
121	Коридор	6.17	
122	Репетиторий	95.08	
134	Репетиторий	67.56	
135	Репетиторий	89.29	
136	Коридор	5.33	
137	Репетиторий	42.00	
138	Холл	94.39	
139	Холл	31.93	
174	Холл	48.72	
179	Коридор	51.19	
180	Коридор	40.82	
181	Многоцветное пространство	316.18	
Л7	Технологическая лестница	26.18	
Л8	Лестничная клетка (Тип ЛК: Н2)	17.65	

1085.76

Ведомость возводимых перегородок и стен по фрагменту в осях 1-18/А-П 1 этажа			
Марка	Наименование	Площадь, кв. м.	Примечание
1	Перегородка из бетонного камня	31.95	
3.1	КНАУФ перегородка типа на основе С135	20.80	
9	Кирпичная кладка	4.86	

57.61