



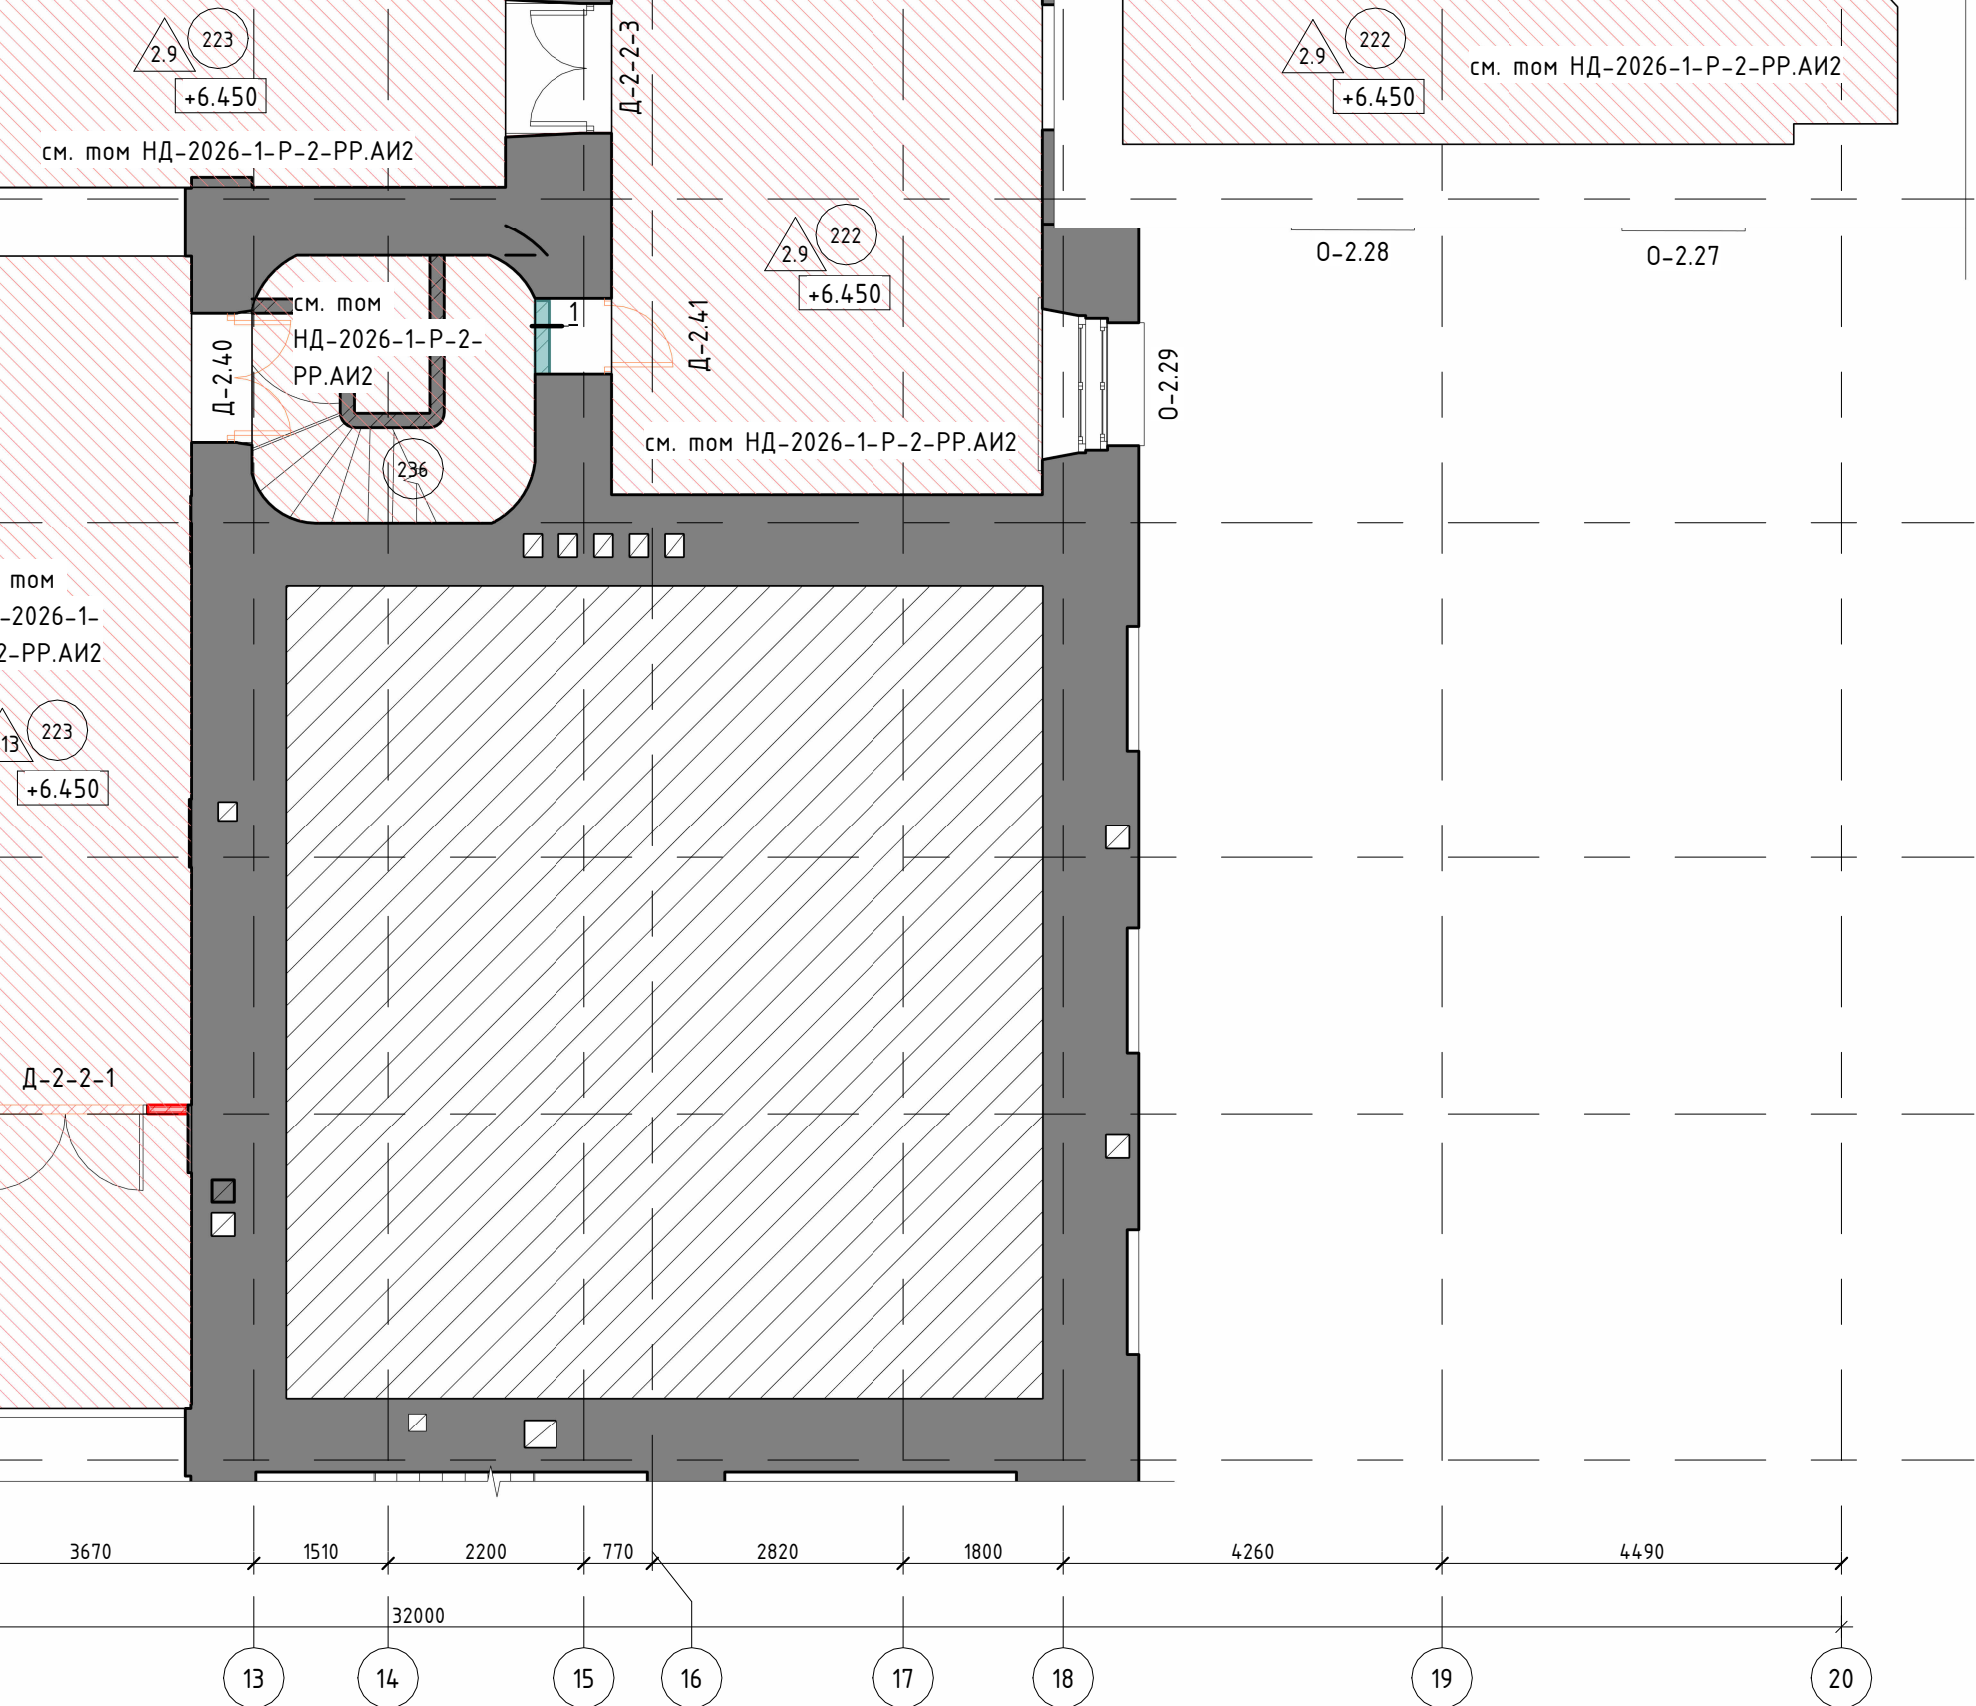


Экспликация помещений фрагментов 2 этажа в осях 10-Д-П, 12-16/Б-Д, 6-8/Д-И		
Имя	Площадь, кв. м.	Кат. пом.
	82.14	
	2.15	В4
	7.02	
	54.78	
	21.85	
	67.32	
	43.67	
	9.60	
	33.15	
	18.45	

Экспликация помещений фрагментов 2 этажа в осях 7-20/П-Ю, 9-20/Д-П, 12-16/Б-Д, 6-8/Д-И				
Номер	Имя	Площадь, кв. м.	Кат. пом.	
230	Коридор	25.40		
231	Кладовая	9.24	В3	
232	Кладовая	7.65	В3	
233	Кладовая	9.27	В3	
234	Коридор	11.86		
236	Коридор	6.37		
242	Комната отдыха	64.54		
252	ПУИ	4.61	В4	
253	С/У М	15.99		
254	Коридор	13.85		

Экспликация помещений фрагментов 2 этажа в осях 7-20/П-Ю, 9-20/Д-П, 12-16/Б-Д, 6-8/Д-И				
Номер	Имя	Площадь, кв. м.	Кат. пом.	
257	Коридор	24.96		
Л1	Лестничная клетка (Тип ЛК: Л2)	21.56		
Л2	Технологическая лестница	20.79		
Л3	Технологическая лестница	4.74		
Л4	Технологическая лестница	10.22		
Л5	Лестничная клетка (Тип ЛК: Л2)	19.68		
Л7	Технологическая лестница	26.26		
Л8	Лестничная клетка (Тип ЛК: Н2)	19.25		
		971.51		

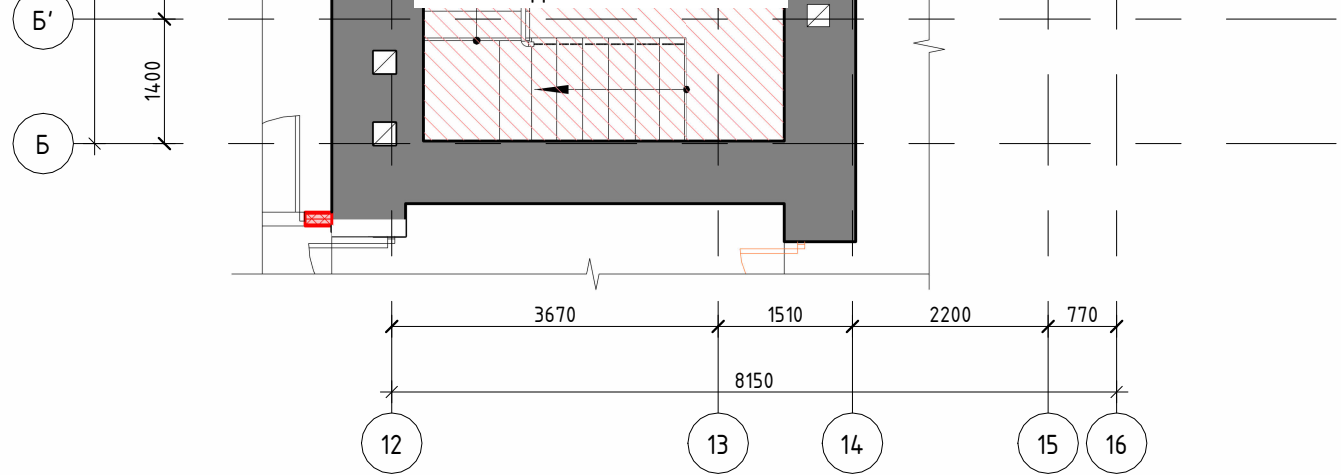

Маркировочный план фрагмента 2 этажа в осях 6-8/Д-И

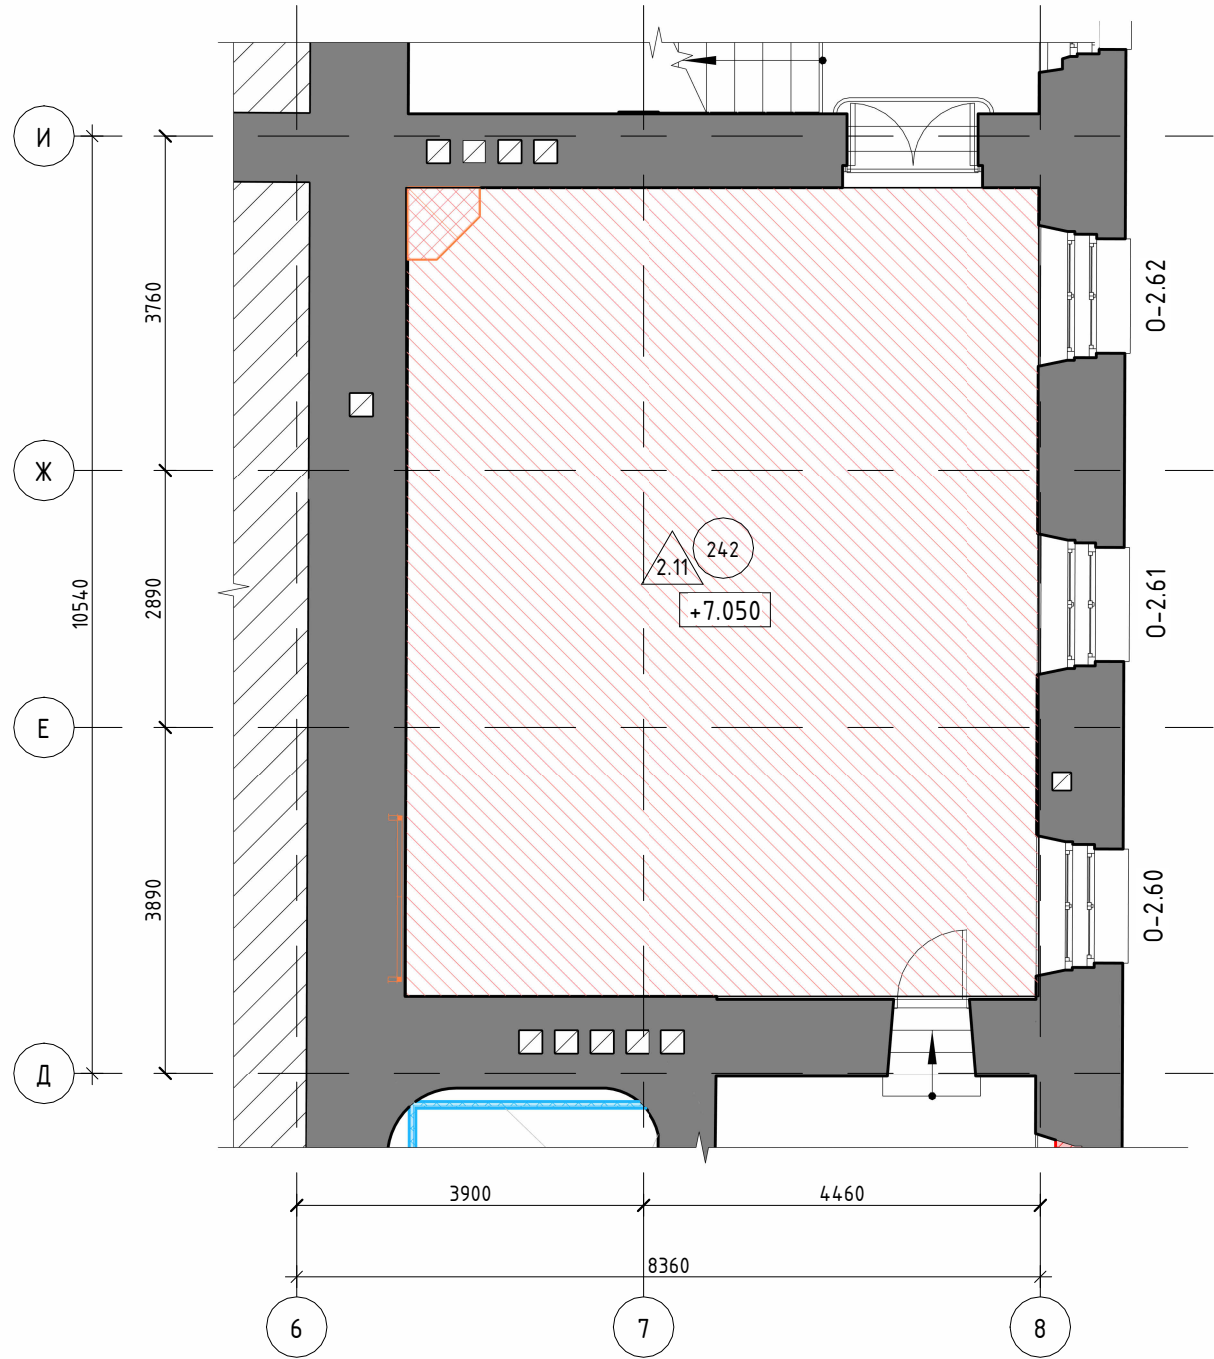

1. Данный лист смотреть совместно листами 5-6, 19-20, 36-43 данного тома;
2. Общая спецификация возводимых стен и перегородок дана на листе 39 данного тома;
3. Общая спецификация экспликация устраиваемых полов дана на листе 36-38 данного тома;
4. Общая спецификация элементов дверных заполнений дана на листе 40-43 данного тома;
5. Маркировка проемов и ниш сквозная по этажу фрагмента дана в стенах и перегородках.