


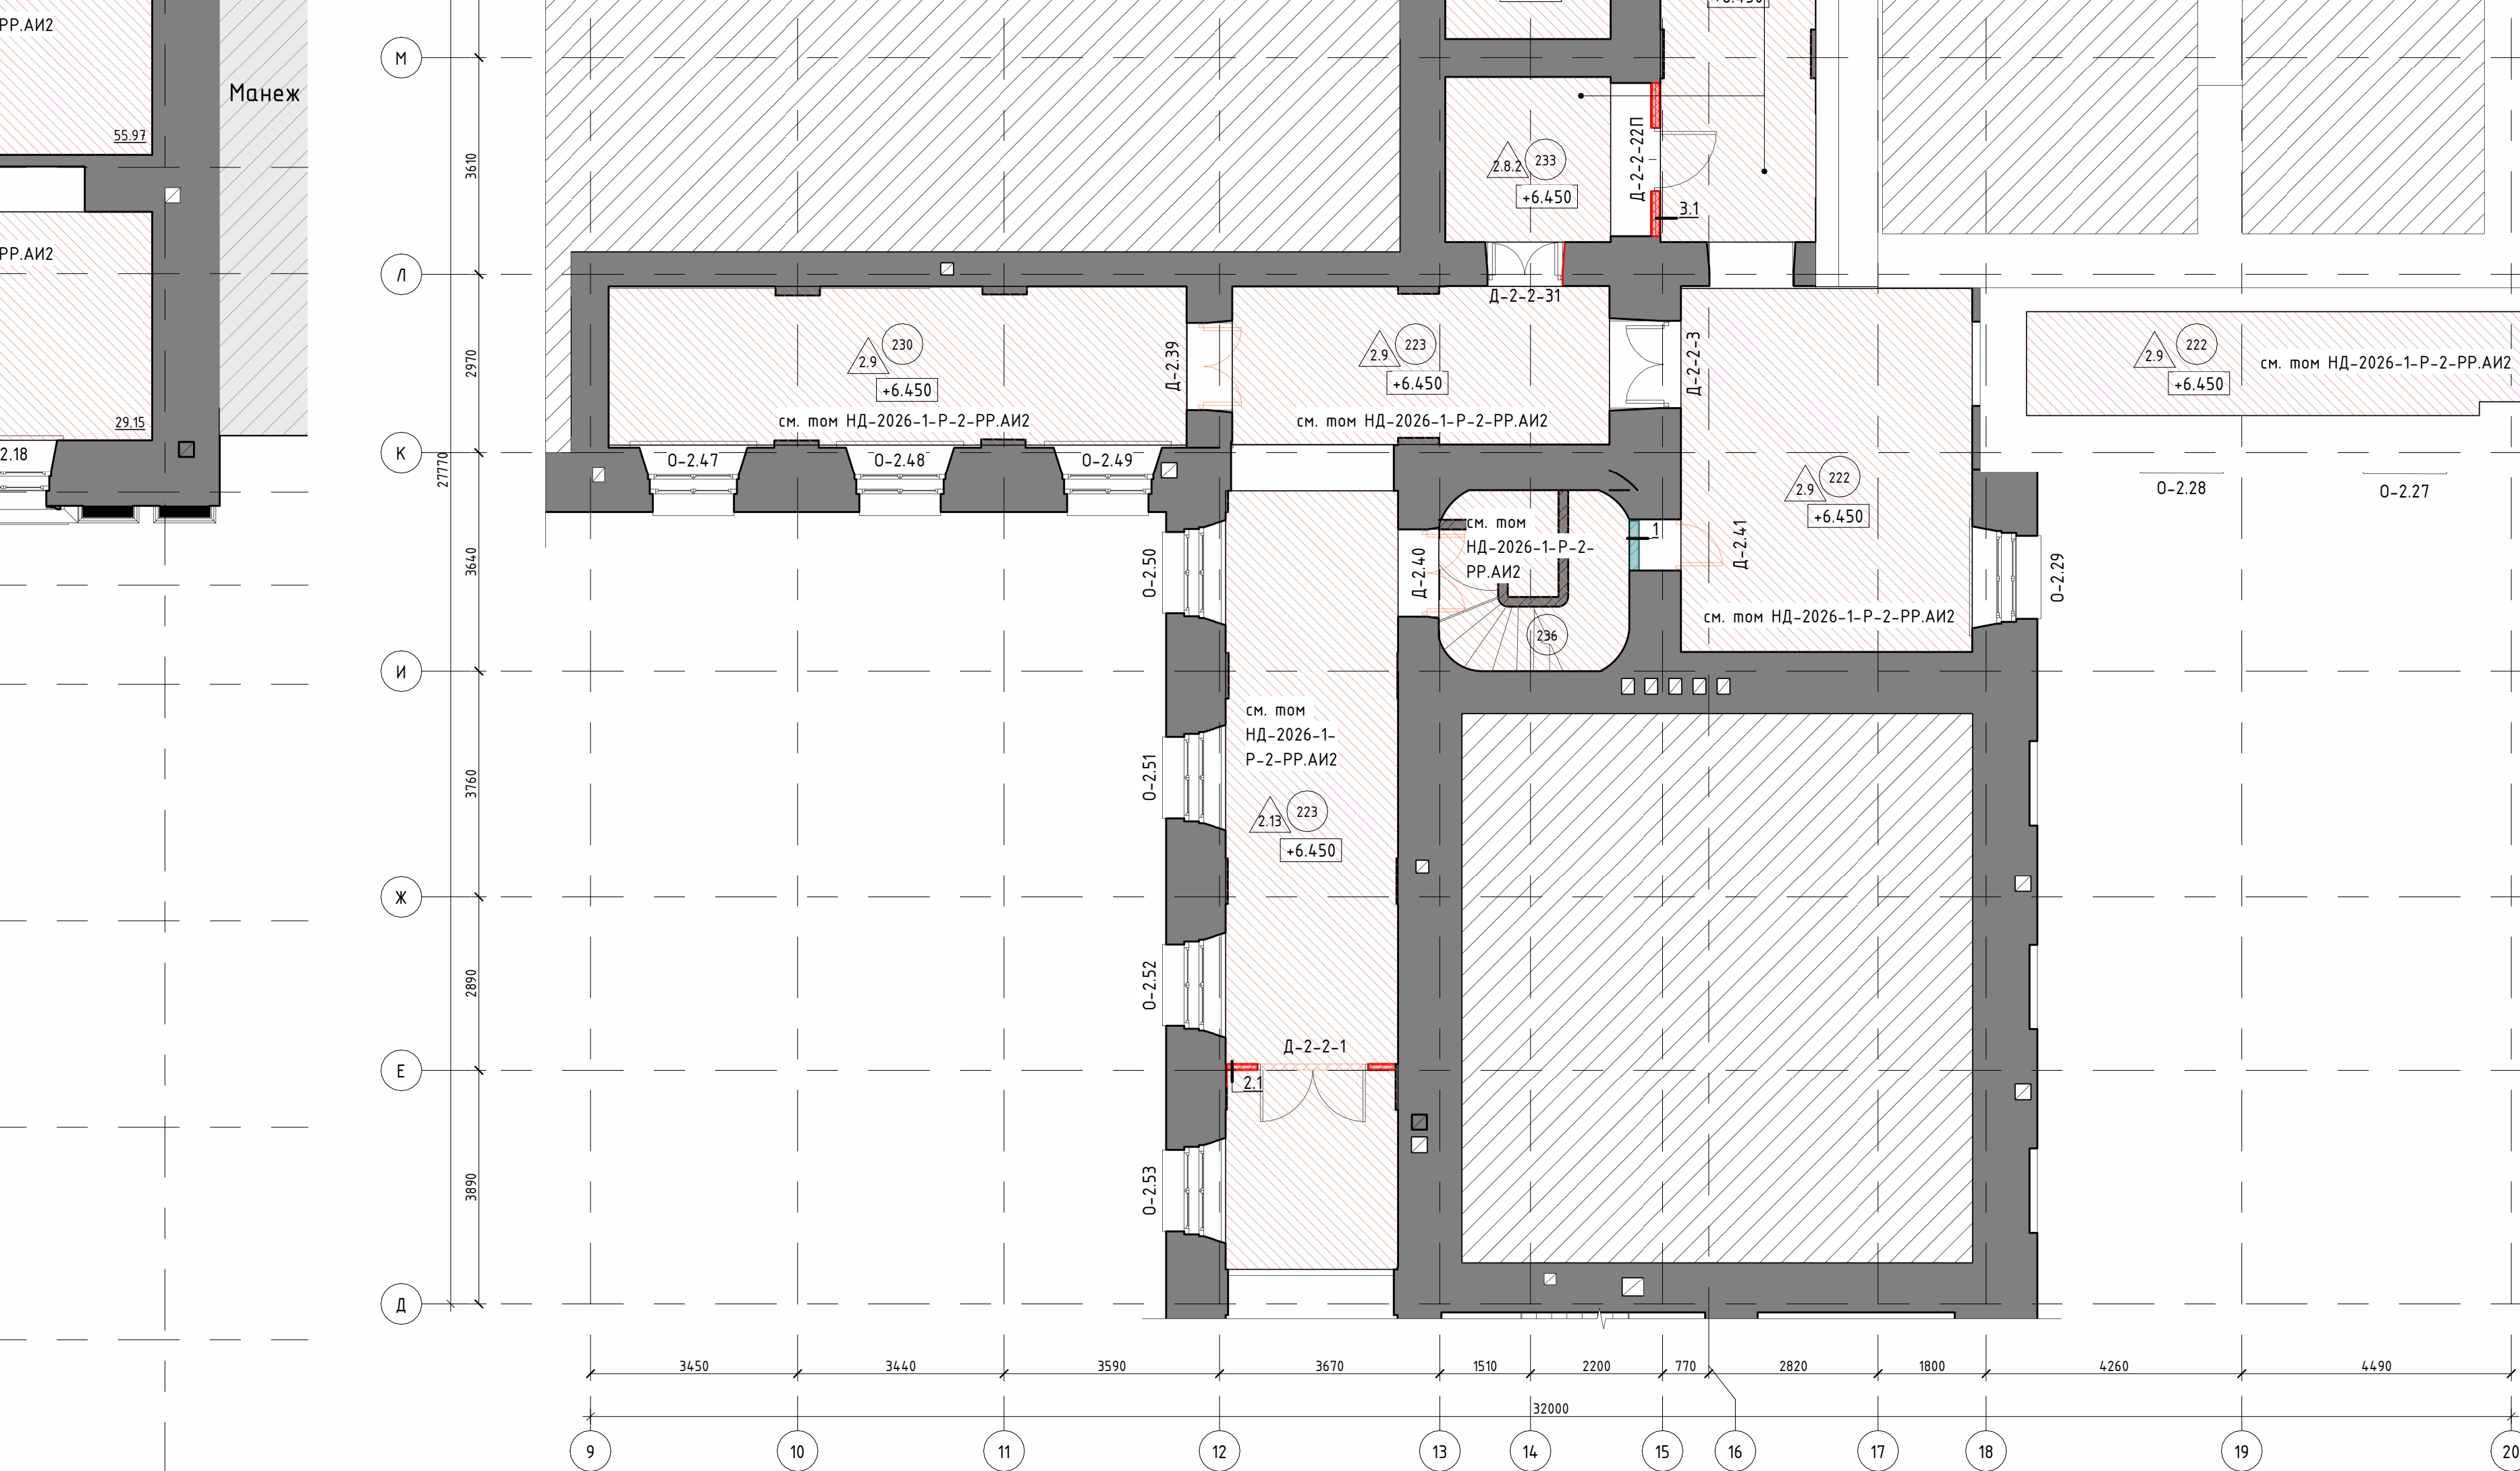

0-2.26				Экспликация помещений фрагментов 2 этажа в осях 7-20/П-Ю, 9-20/Д-П, 12-16/Б-Д, 6-8/Д-И				Экспликация помещений фрагментов 2 этажа в осях 7-20/П-Ю, 9-20/Д-П, 12-16/Б-Д, 6-8/Д-И				Экспликация помещений фрагментов 2 этажа в осях 7-20/П-Ю, 9-20/Д-П, 12-16/Б-Д, 6-8/Д-И				Экспликация помещений фрагментов 2 этажа в осях 7-20/П-Ю, 9-20/Д-П, 12-16/Б-Д, 6-8/Д-И			
ном НД-2026-1-				Номер	Имя	Площадь, кв. м.	Кат. пом.	Номер	Имя	Площадь, кв. м.	Кат. пом.	Номер	Имя	Площадь, кв. м.	Кат. пом.	Номер	Имя	Площадь, кв. м.	Кат. пом.
				202	С/У Ж	10.30		214	Коридор	82.14		230	Коридор	25.40		257	Коридор	24.96	