


агментов в осях 1-20/П-Ю 3 этажа

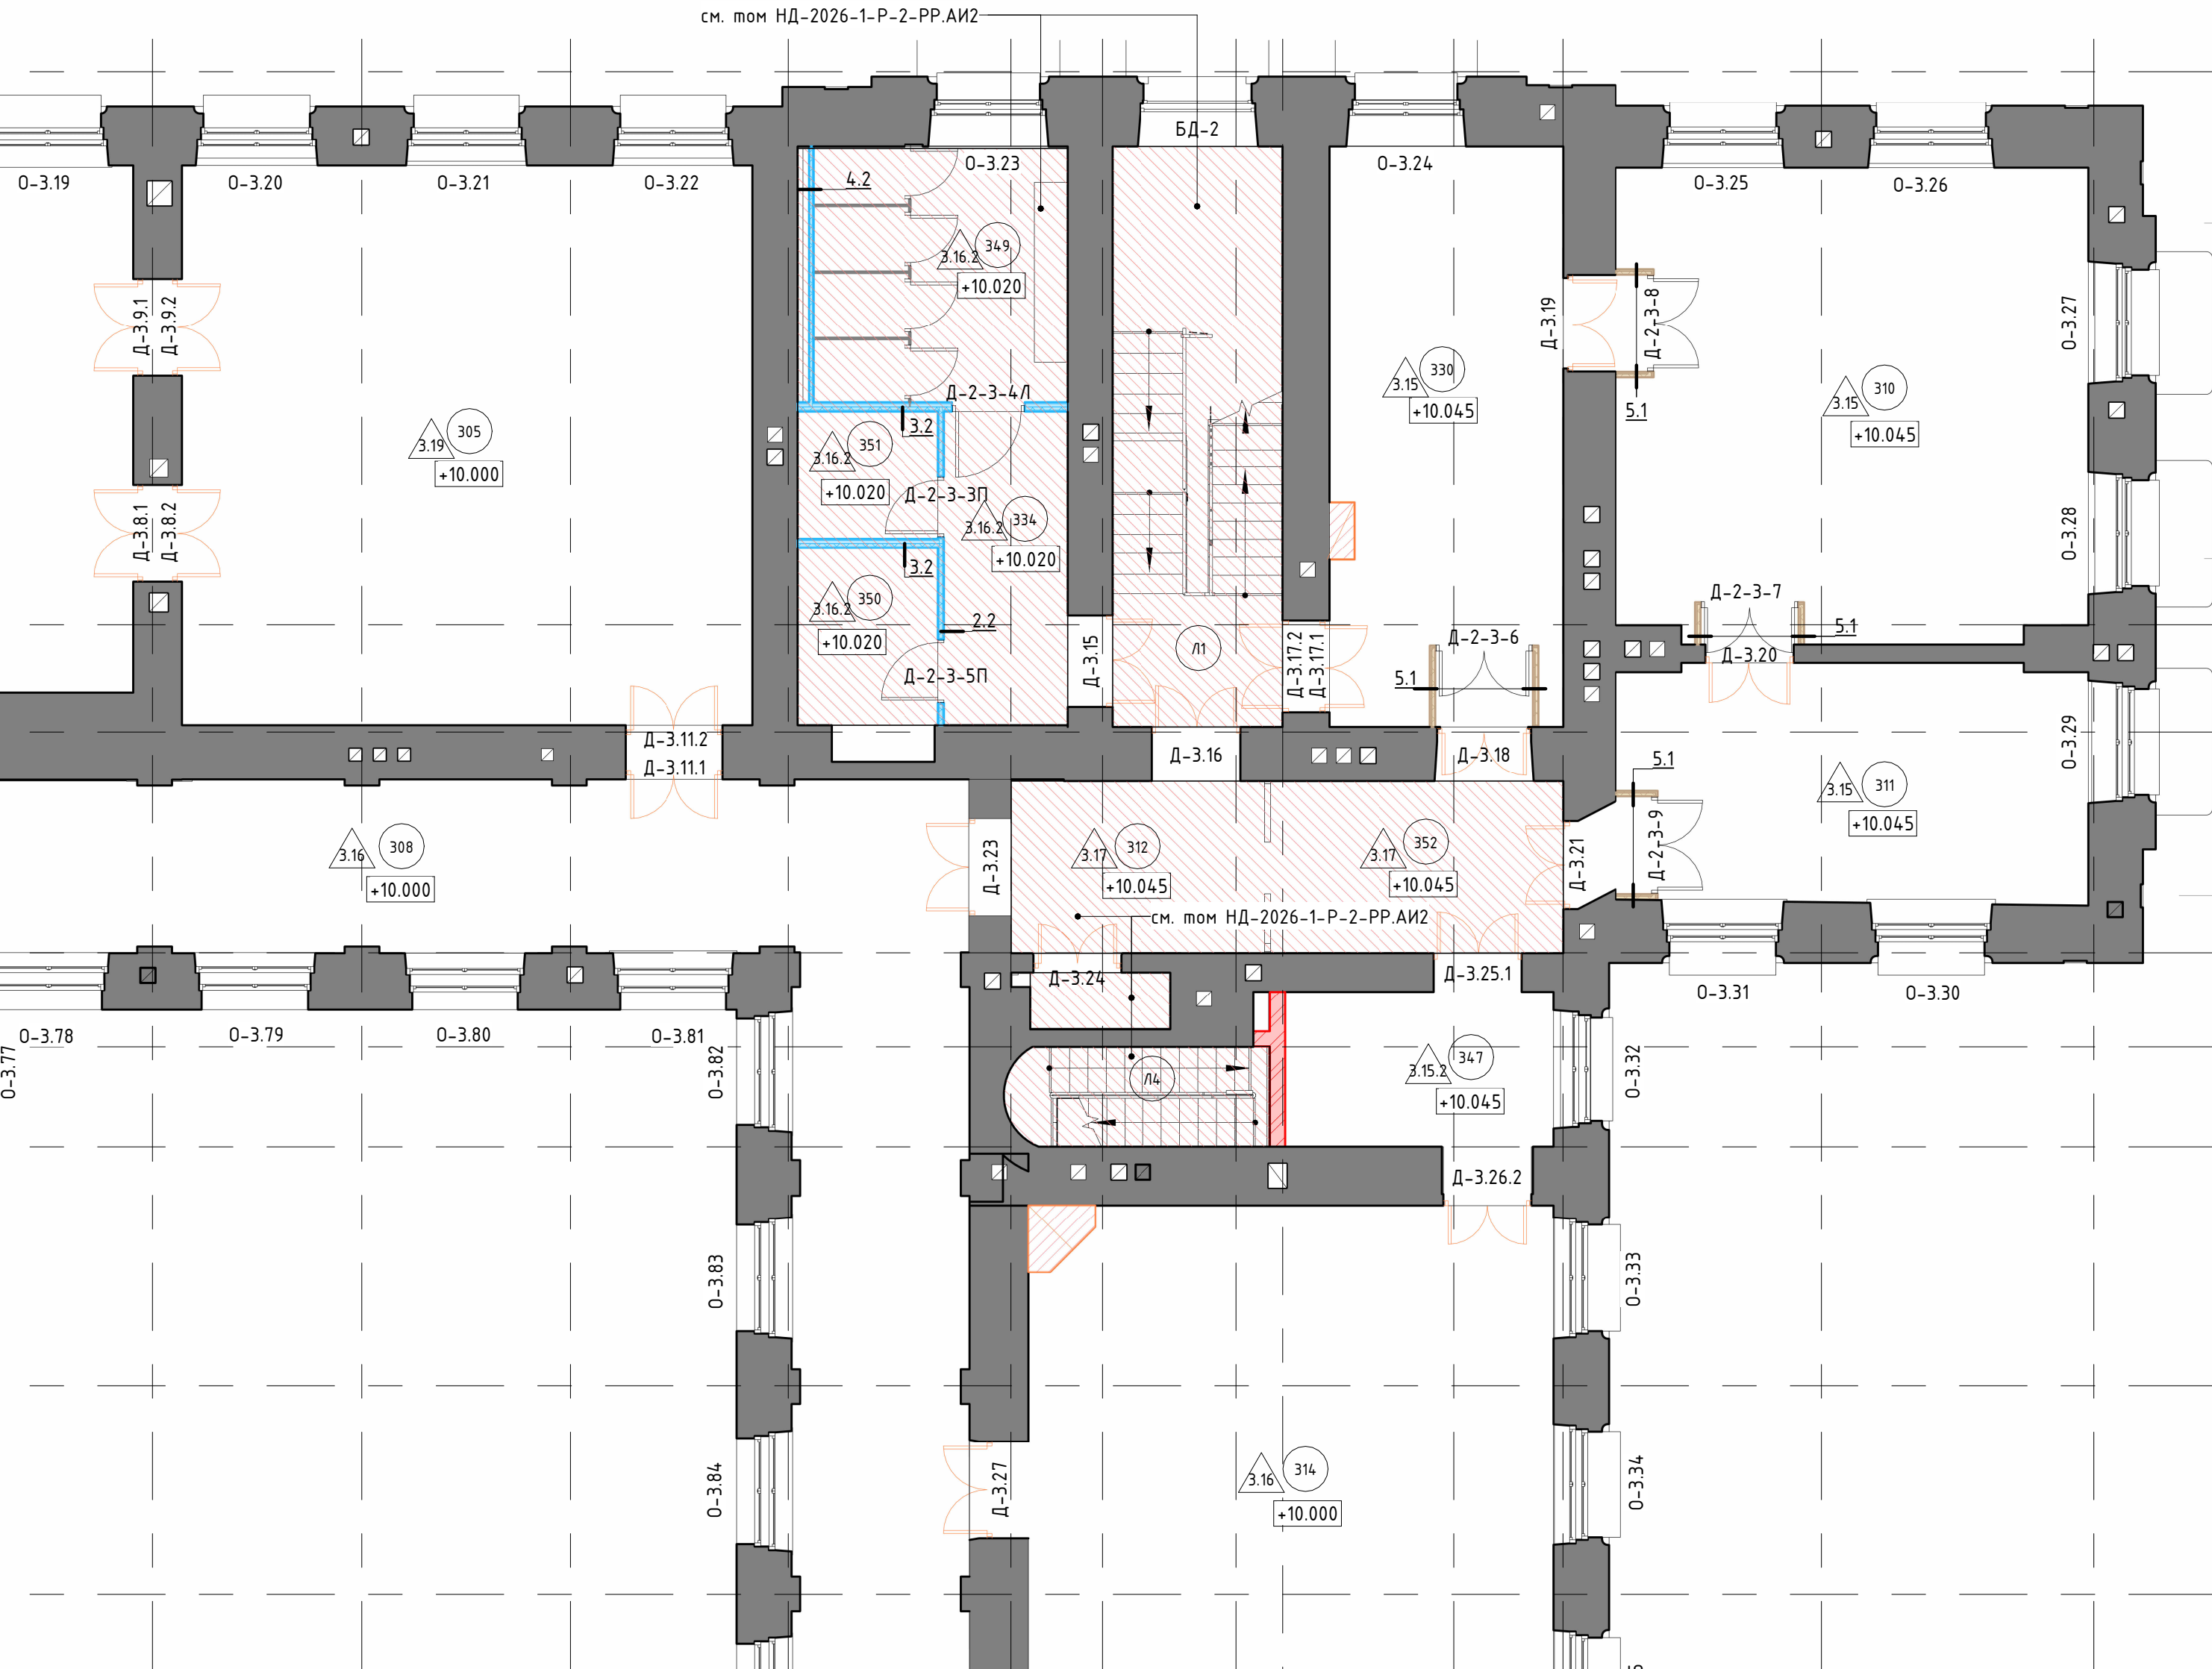

Экспликация помещений фрагмента 3 этажа в осях 1-20/П-Ю			
Номер	Имя	Площадь, кв. м.	Кат. пом.
303	Концертный зал	300.63	
304	Виртуальный концертный зал №1	248.29	
305	Холл	86.89	
307	Коридор	5.65	
308	Коридор	110.33	
309	Аппаратная	10.99	ВЗ
310	Репетиторий	60.54	
311	Репетиторий	30.42	
312	Коридор	11.81	
314	Артистическая	79.75	
315	Коридор	4.98	
330	Репетиторий	36.93	
334	Коридор	10.53	
347	Кладовая чистой посуды	11.49	
349	С/У М	17.57	
350	Моечная	6.74	
351	Душевая	4.85	
352	Коридор	13.67	
Л1	Лестничная клетка (Тип ЛК: Л2)	26.76	
Л2	Технологическая лестница	10.92	
Л3	Технологическая лестница	8.56	
Л4	Технологическая лестница	6.93	
Л5	Лестничная клетка (Тип ЛК: Л2)	14.09	
		1119.29	

Ведомость возводимых перегородок и стен по фрагменту в осях 1-20/П-Ю 3 этажа			
Марка	Наименование	Площадь, кв. м.	Примечание
1	Перегородка из бетонного камня	14.33	
2.2	КНАУФ перегородка типа С382	13.82	
3.2	КНАУФ перегородка типа С385.2	21.24	
5.1	Перегородка звукоизоляционная 90 мм	17.30	
		66.68	

Ведомость закладываемых проемов фрагмента 3 этажа в осях 1-20/П-Ю			
Марка	Наименование	Объем, куб. м.	Примечание
Зп-2-3-2	Кирпичная кладка	0.24	
Зп-2-3-3	Кирпичная кладка	2.49	
		2.73	