


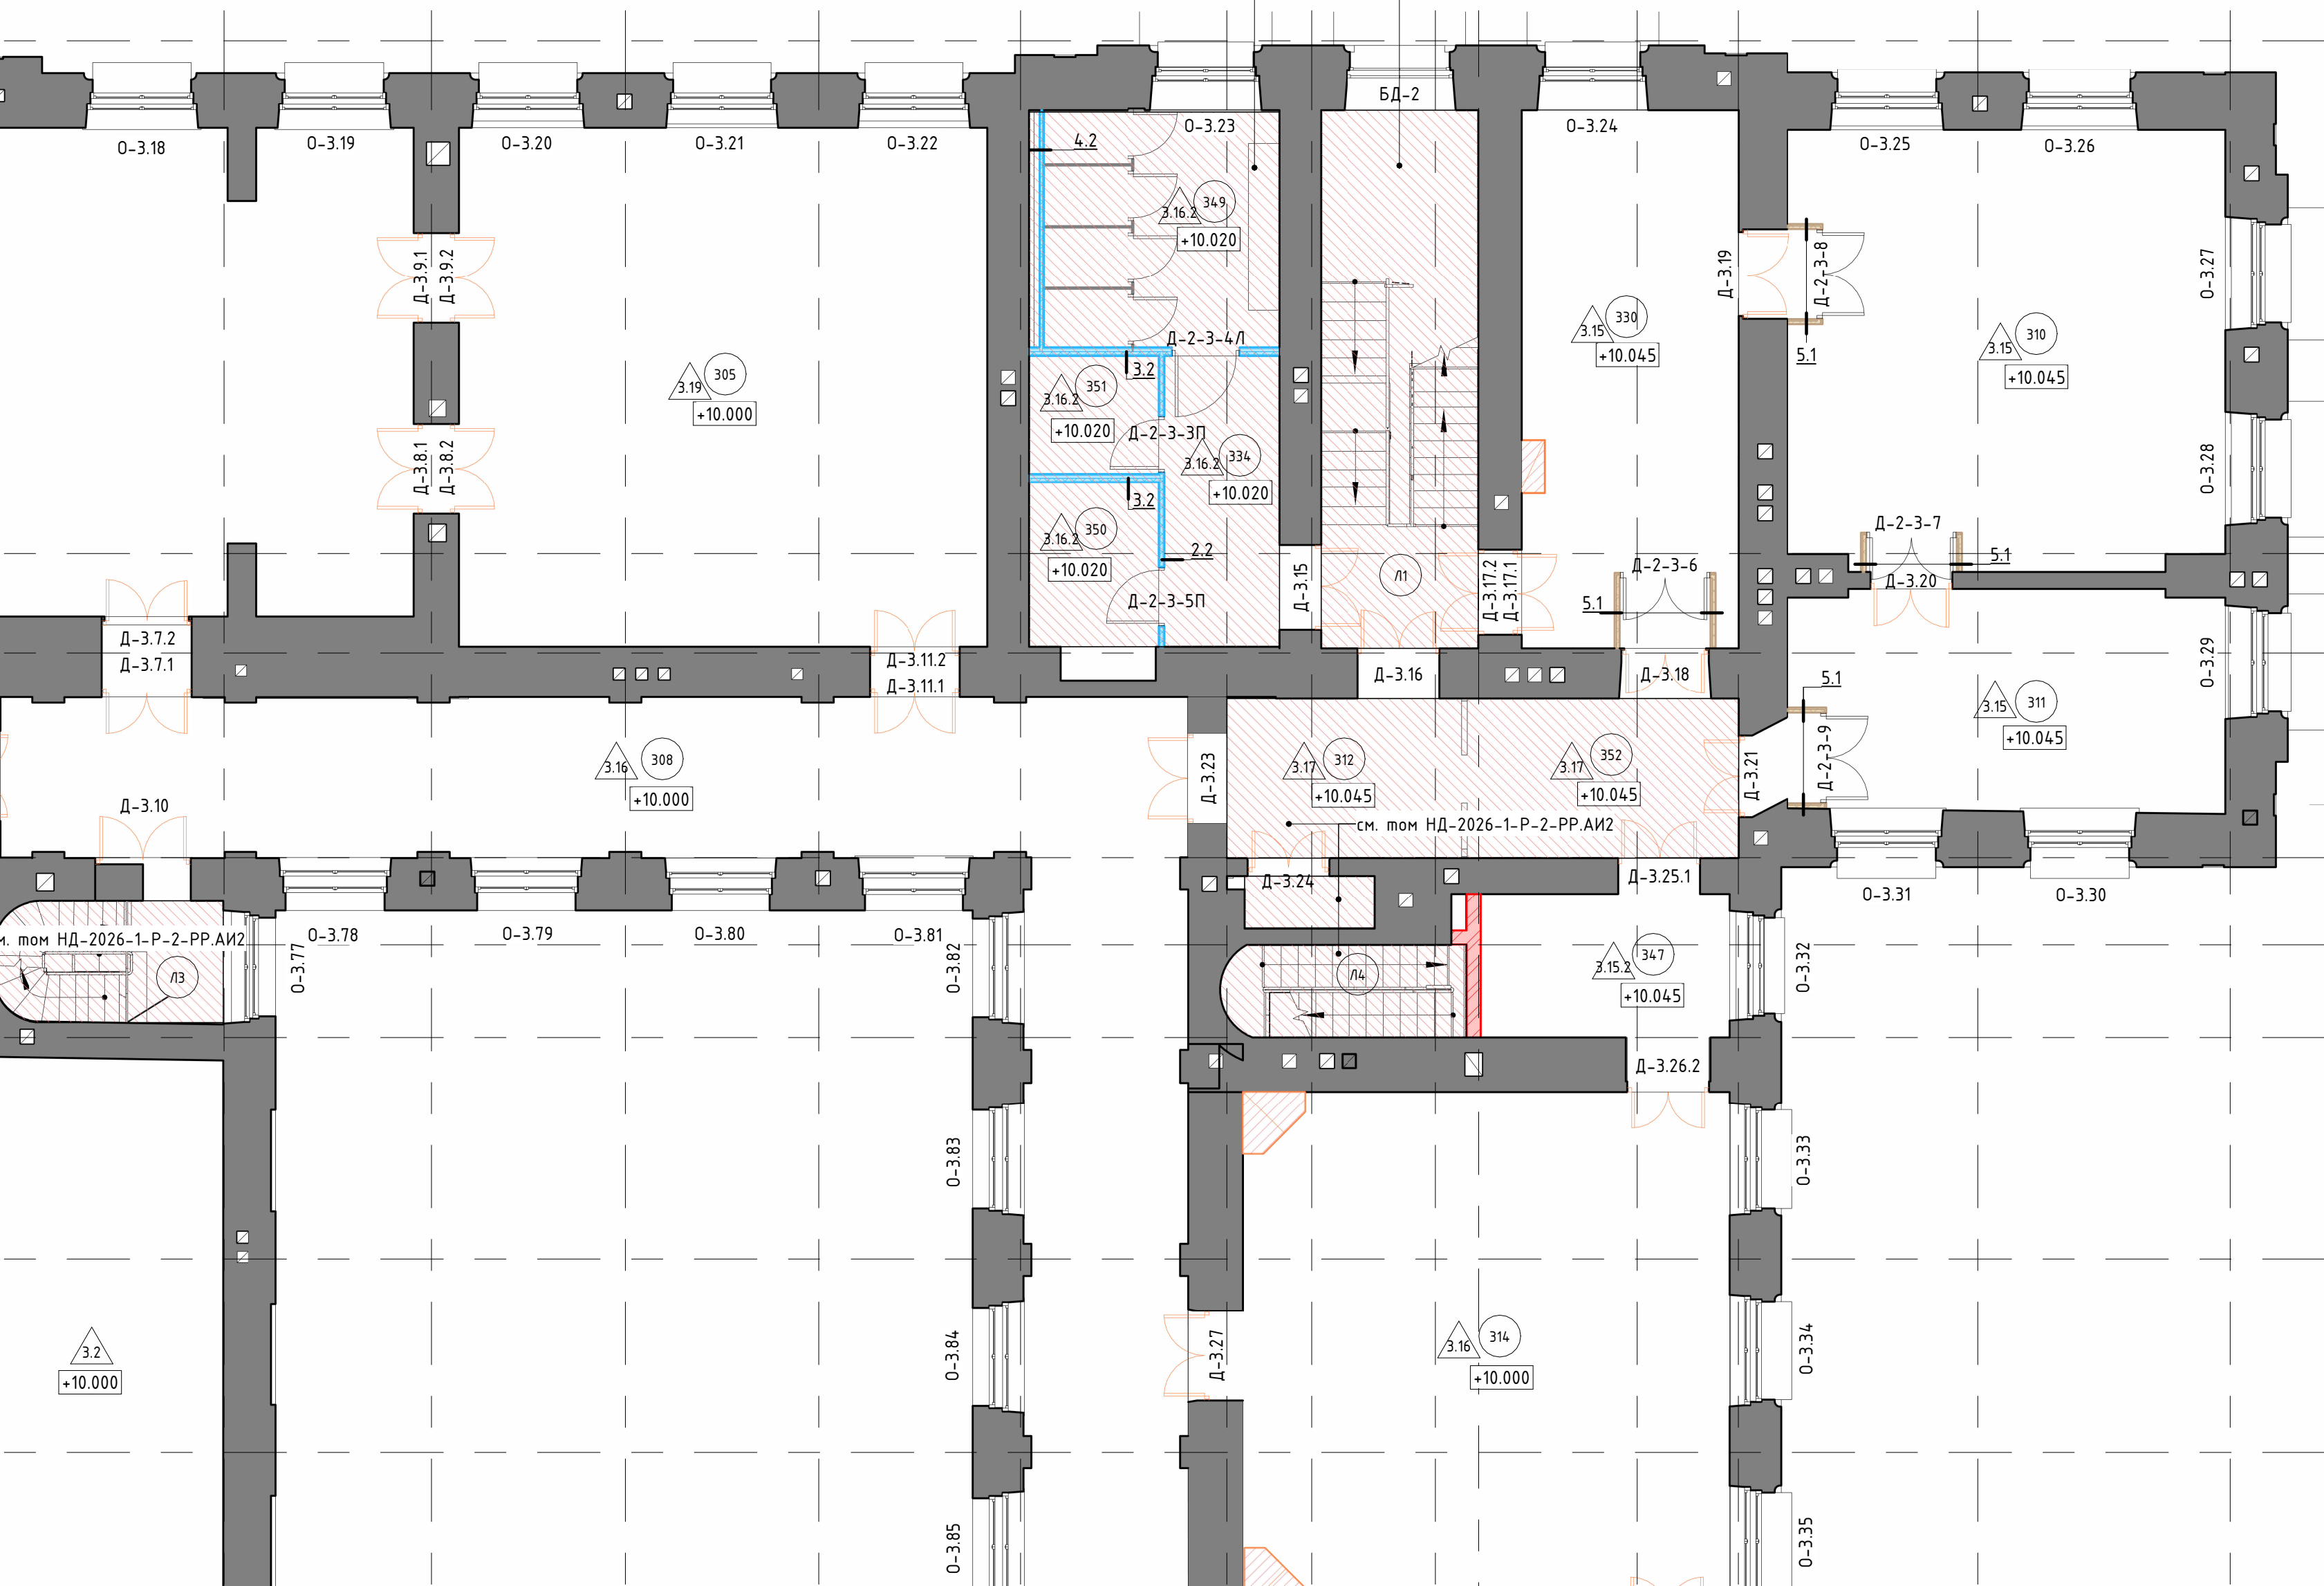

Ведомость возводимых конструкций по фрагменту в о	
Марка	Наименование
1	Перегородка бетонного ко
2.2	КНАУФ перегородка типа С382
3.2	КНАУФ перегородка типа С385.2
5.1	Перегородка звукоизоляционная 90 мм

Ведомость закладываемых фундаментов в осях	
Марка	Наименование
Зп-2-3-2	Кирпичная кладка
Зп-2-3-3	Кирпичная кладка