


Инв. № подл.	Подп. и дата	Взам. инв. №	Согласовано

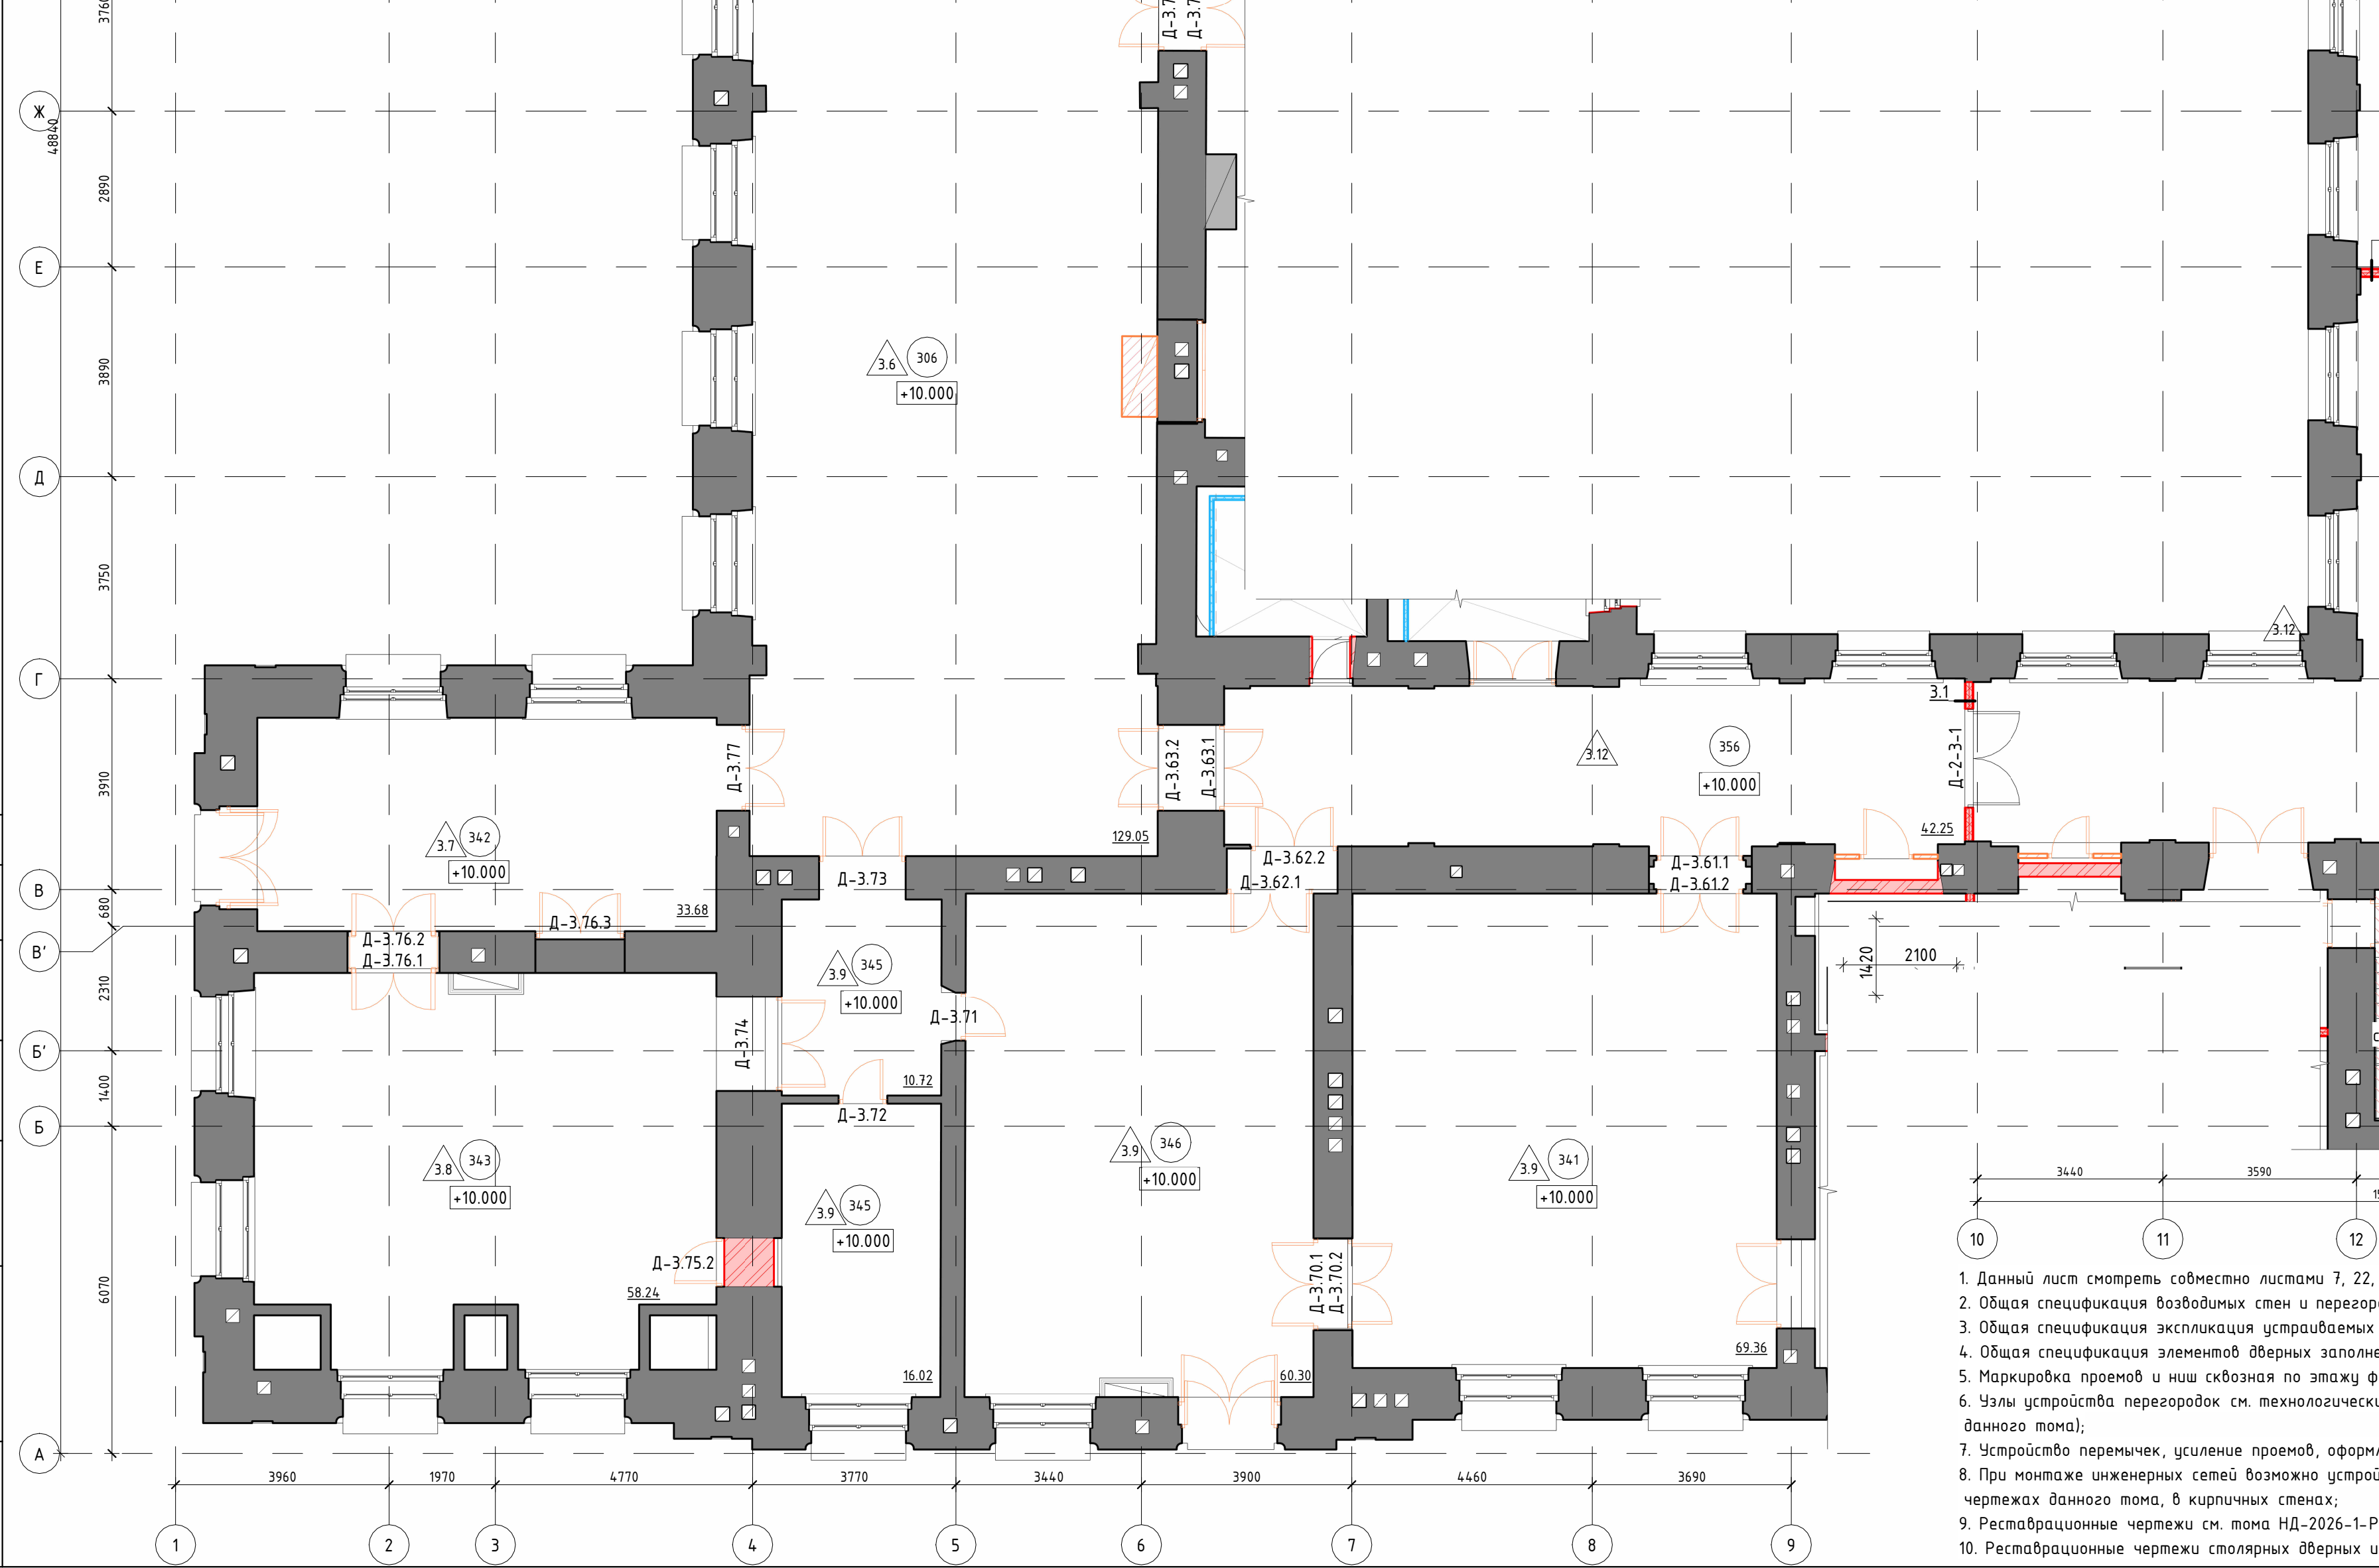

1. Данный лист смотреть совместно листами 7, 22,
2. Общая спецификация возводимых стен и перегородок
3. Общая спецификация экспликация устраиваемых
4. Общая спецификация элементов дверных заполнения
5. Маркировка проемов и ниш сквозная по этажу ф
6. Узлы устройства перегородок см. технологическ
- данного тома);
7. Устройство перемычек, усиление проемов, оформ
8. При монтаже инженерных сетей возможно устрой
- чертежах данного тома, в кирпичных стенах;
9. Реставрационные чертежи см. тома НД-2026-1-Р
10. Реставрационные чертежи столярных дверных и