


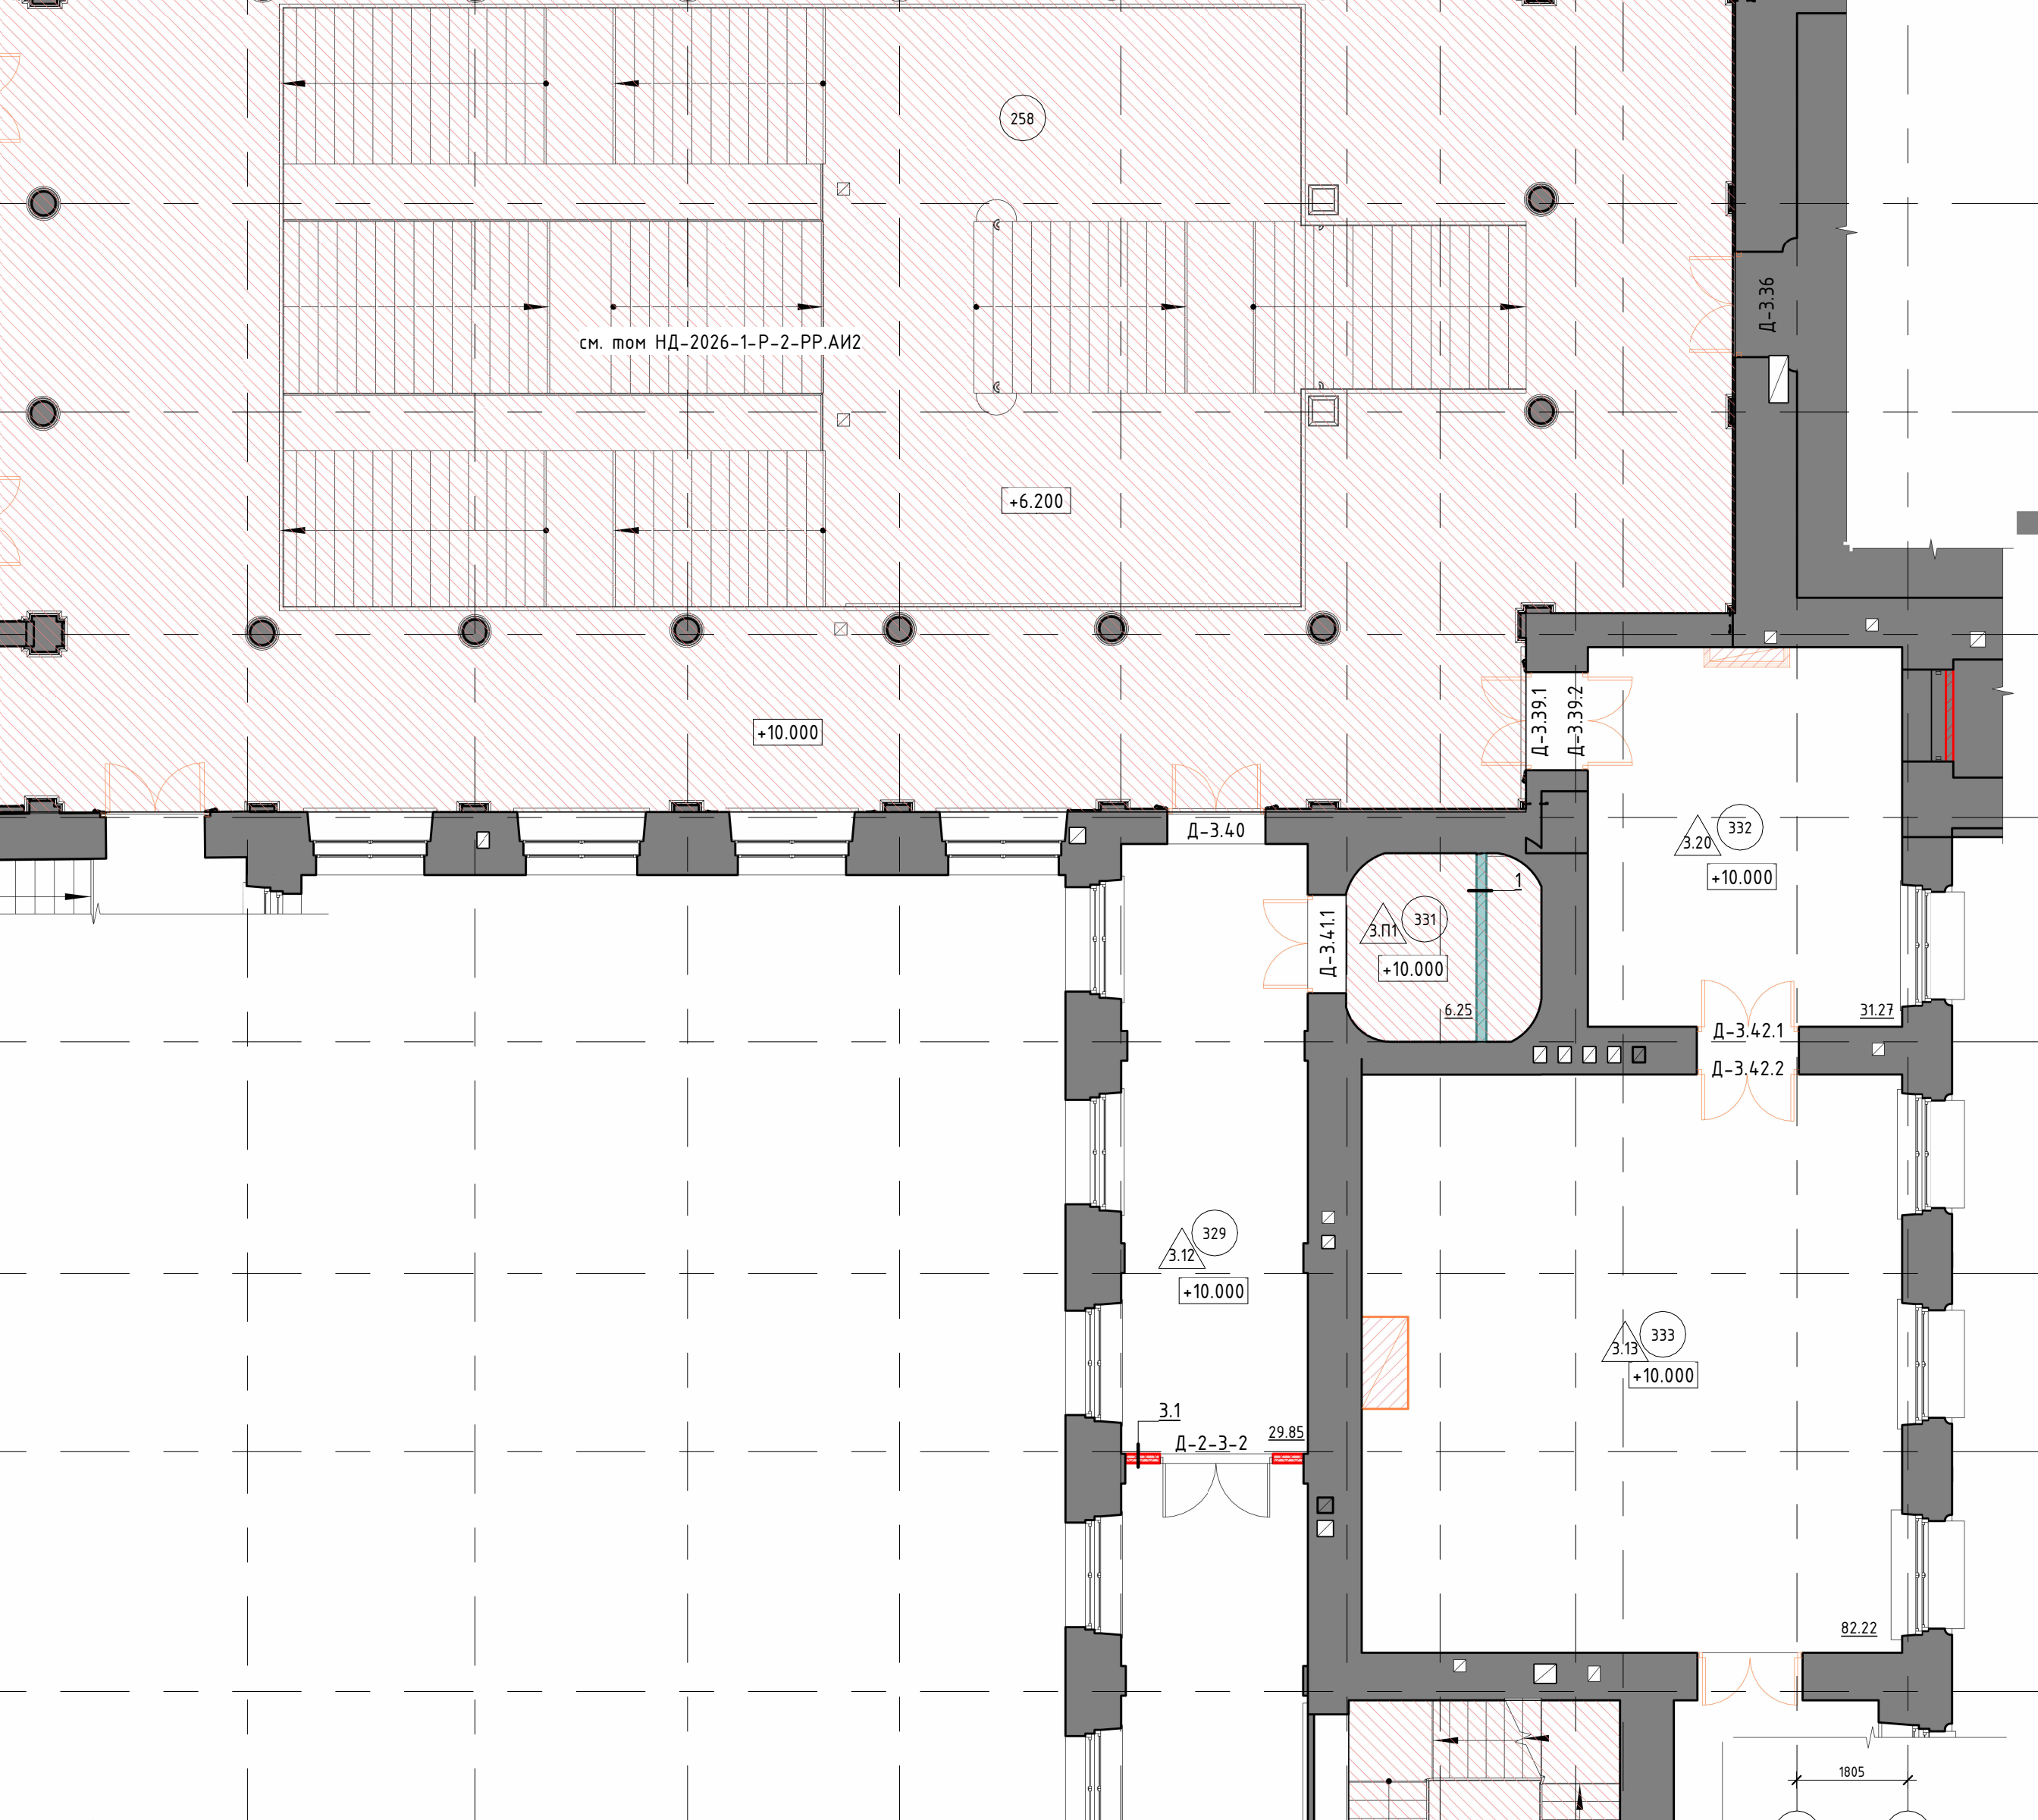

331	Коридор	6.25	
332	Кабинет	31.27	
333	Репетиторий	82.22	
341	Артистическая	69.36	
342	Артистическая	33.68	
343	Артистическая	58.24	
345	Буфет	26.75	
346	Кабинет	60.30	
354	Многоцветное пространство	281.03	
355	Коридор	53.84	
356	Коридор	42.25	
Л7	Технологическая лестница	26.90	
Л8	Лестничная клетка (Тип ЛК: Н2)	17.45	
		1098.04	

Ведомость возводимых перегородок и стен фрагмента 3 этажа в осях 1-18/А-Р			
Марка	Наименование	Площадь, кв. м.	Примечание
1	Перегородка из бетонного камня	11.78	
3.1	КНАУФ перегородка типа на основе С135	10.40	
		22.17	