Фрагмент плана потолка 5 этажа в осях 4-12/Г-С (1 : 75)

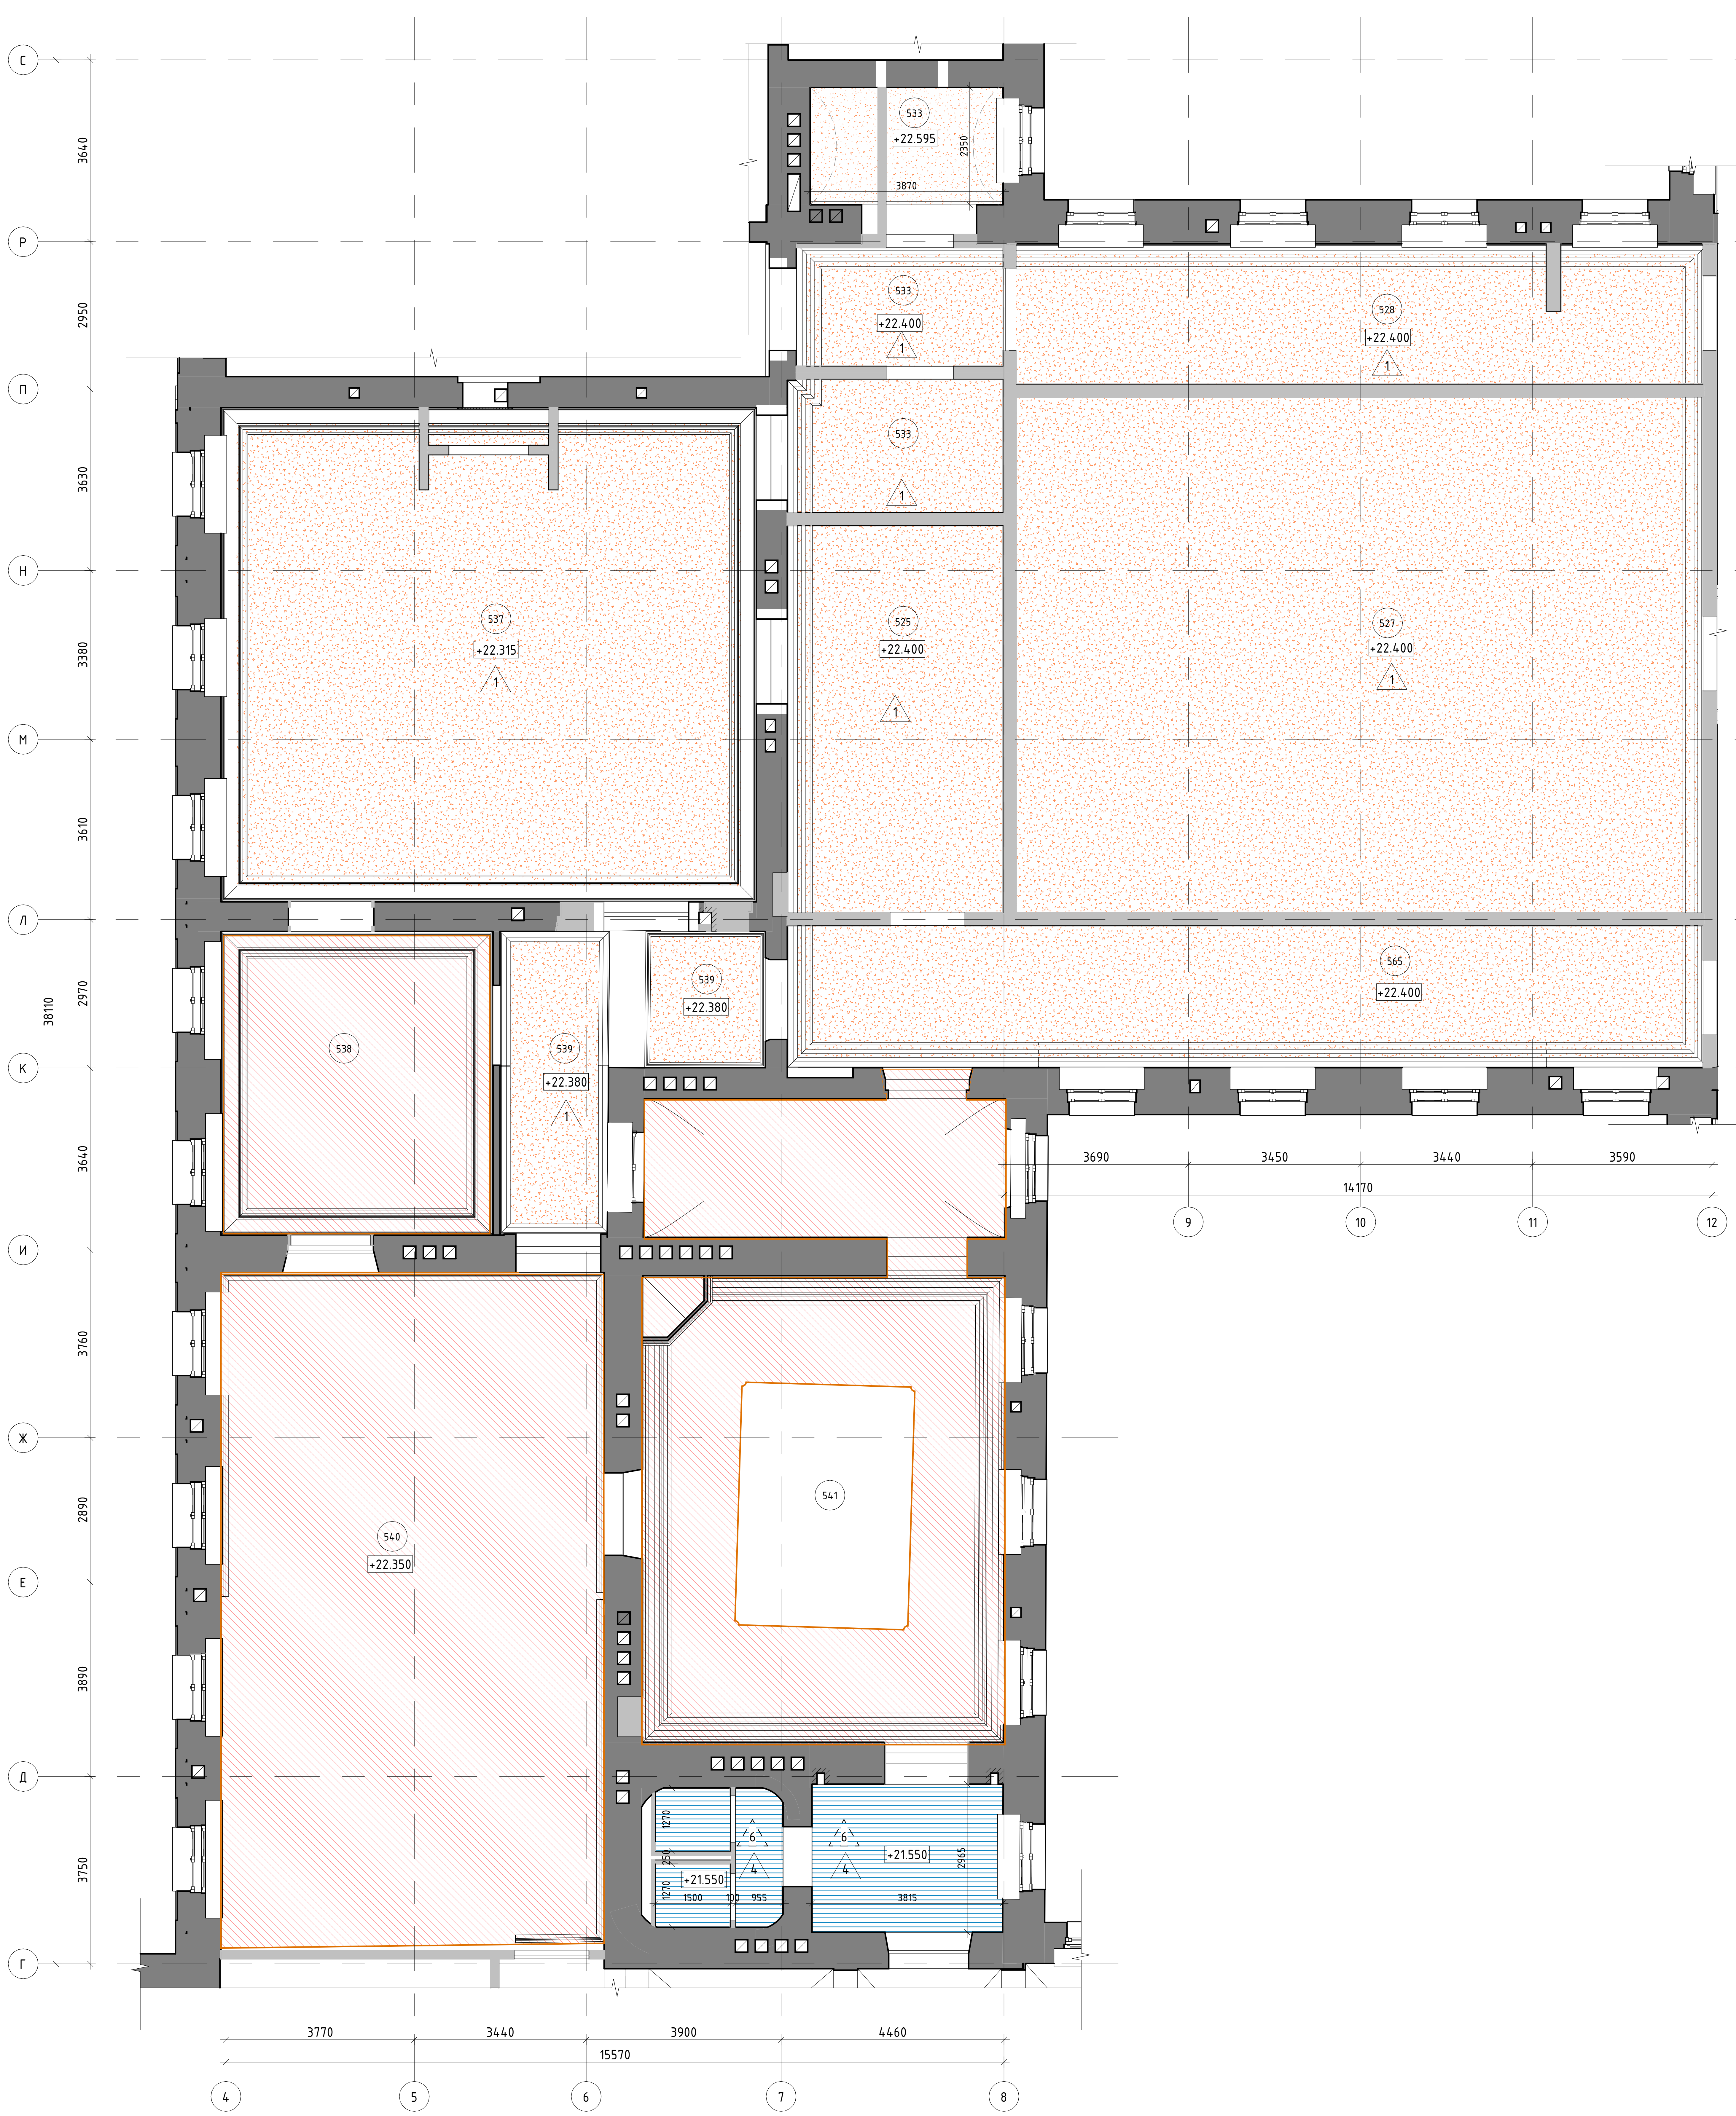

Экспликация помещений фрагмента 5 этажа в осях 4-12/Г-С			
Номер	Имя	Площадь, кв. м.	Кат. пом.
525	Помещение персонала	33.46	
527	Венткамера	141.87	Д
528	Коридор	37.43	
533	Коридор	26.86	
537	Гостиная	105.99	
538	Комната отдыха	33.10	
539	Коридор	21.68	
540	Буфет	104.58	
541	Холл	67.54	
542	С/У	17.97	
565	Коридор	52.06	
Л6	Лестничная клетка (Тип ЛК: Л2)	20.05	
		662.60	

Ведомость ремонта фрагмента потолков в осях 4-12/Г-С 5 этажа					
Марка	Схема потолка	Описание	Площадь, кв.м.	Вид работ	Примечание
1		Улучшенная известково-гипсовая штукатурка по подготовленному основанию (перекрытию) - 25 мм	418.65	1. Убрать красочные слои 2. Демонтаж штукатурного слоя только в местаж примыкания демонтированных перегородок/стен к потолку. Ремонт кирпичной кладки при необходимости (вычинка/инъектирование) 3. Восполнение штукатурного слоя в местаж примыкания демонтированных перегородок/стен к потолку. 4. Перетирка гладкой штукатурной поверхности потолка 5. Ремонт штукатурного декора	

Ведомость декора фрагмента потолков в осях 4-12/Г-С 5 этажа						
Наименование	Эскиз	Длина тяги	Длина огиба профиля, м	Площадь сечения, кв. м.	Вид работ	Примечание
Карнизная тяга пом. 525, 527, 528, 533, 565		31.5			Новый элемент	
Карнизная тяга пом. 525, 527, 528, 533, 565		28.1			Ремонт	
Карнизная тяга пом. 537		41.2			Ремонт	
Карнизная тяга пом. 539		8.9			Новый элемент	
Карнизная тяга пом. 539		17.7			Ремонт	

Ведомость потолков фрагмента 5 этажа				
Марка	Схема потолка	Данные элементов потолка, мм	Площадь, кв.м.	Примечание
4		КНАУФ подвесной потолок из влагостойкого гипсокартона (ГСП-Н2) на одноуровневом профиле типа П113 (по подготовленному основанию кирпичного свода или железобетонной плиты) – 50-600 мм	17.82	
			17.82	

Условные обозначения:

1	– Ось координации
+0,000	– Отметка уровня
122	– Марка помещения
▨	– Реставрируемые помещения
▬	– Сохраняемые конструкции
△ 2	– Марка потолка
▬	– Возводимые перегородки
▤	– ГКЛ
▤	– ГКЛВ
▒	– Штукатурка
▒	– Влагостойкая штукатурка

1. Данный лист следует рассматривать совместно с листами 8, 15 данного тома;
2. Устройство перемычек, усиление проемов и оформление отверстий выполнять по типовым чертежам, разработанным в НД-2026-1-Р-1.1-КР;
3. Реставрационные чертежи см. в томе НД-2026-1-Р-1.1-РР.АИ;
4. В помещениях с подвесным потолком штукатурные работы следует выполнять до монтажа потолочной зашивки, см. том НД-2026-1-Р-1.1-РР.АИ;
5. В помещениях различного функционального назначения предусмотреть дифференциацию по типам штукатурки:
   - — в мокрых зонах под подвесной потолок — влагостойкая улучшенная известково-гипсовая штукатурка;
   - — в административной, общественной и артистической зонах под подвесной потолок — улучшенная известково-гипсовая штукатурка;
   - — в административной, общественной и артистической зонах без подвесного потолка — высококачественная финишная штукатурка с отделкой согласно разделу АИ.
6. В каждом помещении предусмотреть отделку соответствующим типом штукатурки толщиной 25–30 мм. Уменьшение толщины слоя не допускается.
7. Работы по реставрации кирпичной кладки учтены в томе в томе НД-2026-1-Р-1.1-РР.АИ1, работы по штукатурке см. тома: НД-2026-1-Р-1.1-АИ, если потолок не входит в предмет охраны, и НД-2026-1-Р-1.1-РР.АИ1, если потолок входит в предмет охраны.

Согласовано
Взам. инв. №
Подп. и дата
Инв. № подл.

Изм.	Кол.уч.	Лист	№док.	Подпись	Дата
Разработал		Андреенко			03.26
Разработал		Лысюк			03.26
Рук. проекта		Суша			03.26
ГИП		Чапова			03.26
ГАП		Ермолаева			03.26
Н. контр.		Шапченко			03.26

НД-2026-1-Р-1.1-АР2

г. Санкт-Петербург, пл. Труда, д. 4, литера В

«Ремонт, реставрация и приспособление для современного использования (капитальный ремонт, оснащение технологическим оборудованием, в том числе проектирование) объектов культурного наследия федерального значения «Дворец», «Манеж», «Корпус служебный», «Конюшни главные дворцовые», расположенных по адресу: г. Санкт-Петербург, пл. Труда, д. 4, литера В, входящих в состав объекта культурного наследия федерального значения «Дворец Великого князя Николая Николаевича (Ксенинский институт)»

Стадия	Лист	Листов
Р	22	28

«Дворец». План потолка фрагмента в осях 4-12/Г-С 5 этажа

ОБЩЕСТВО С ОГРАНИЧЕННОЙ ОТВЕТСТВЕННОСТЬЮ
НИиПИ СПЕЦРЕСТАВРАЦИЯ

A1 (594x841)