Общая экспликация полов тома

Номер пом.	Тип пола	Схема пола	Данные элементов пола, мм	Площадь	Примечание
Цоколь					
033, 034, 045, 055, 074, 076	0.2.1	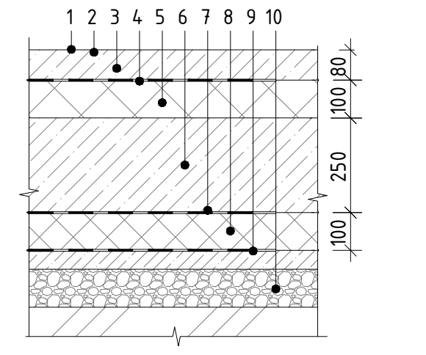	1. Пропитка поверхности укрепляющим и обеспыливающим составом 2. Грунтовка 3. Стяжка уклонообразующая на цементно-песчаном растворе М200, армированная сеткой d5, Вр1 100x100 – 50-80 мм 4. Армированная полиэтиленовая пленка – 300 мкм 5. Минераловатные плиты (ρ=110 кг/м^3) – 100 мм Нижележащие слои учтены в разделе НД-2026-1-Р-1.1/1.2/1.3/1.4/2-КР 6. Плита монолитная железобетонная – 250 мм 7. Армированная полиэтиленовая пленка - 300 мкм 8. Экструдированный пенополистирол Пеноплэкс Фундамент или аналог (ρ=35 кг/м^3) – 100 мм 9. Гидроизоляция рулонная битумосодержащая – 2 слоя 10. Слои инженерной подготовки (бетонная/песчаная/щебеночная подготовка по геотекстилю 200 гр/м^2	83.81	Плавающий пол технического помещения; По периметру помещения (Р=125,25 м) предусмотреть акустический шов толщиной 5 см с закладкой упругим утеплителем (плотность не менее 100 кг/м^3)
003, 009, 011, 015, 017, 020, 021, 025, 026, 039, 060, 064, 073, Л1, Л5, Л6, Л8	0.5	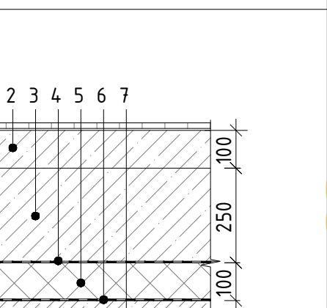	1. Керамогранитная плитка (Ктр=0,40; класс износостойкости 3) на клею см. раздел НД-2026-1-Р-1.1/1.3/1.4/2-АИ– 15+5 мм 2. Стяжка на цементно-песчаном растворе М200, армированная сеткой d5, Вр1 100x100 – 100 мм Нижележащие слои учтены в разделе НД-2026-1-Р-1.1/1.2/1.3/1.4/2-КР 3. Плита монолитная железобетонная – 250 мм 4. Армированная полиэтиленовая пленка - 300 мкм 5. Экструдированный пенополистирол Пеноплэкс Фундамент или аналог (ρ=35 кг/м^3) – 100 мм 6. Гидроизоляция рулонная битумосодержащая – 2 слоя 7. Слои инженерной подготовки (бетонная/песчаная/щебеночная подготовка по геотекстилю 200 гр/м^2	20.61	
027, 028	0.9	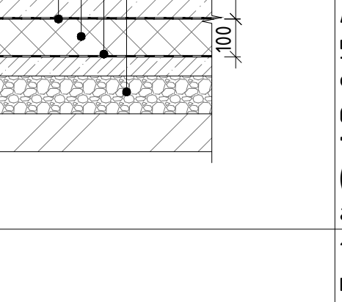	1. Плитка метлахская (Ктр=0,40; класс износостойкости 3) на клею см. раздел НД-2026-1-Р-1.1/1.3/1.4/2-АИ – 15+5 мм 2. Стяжка на цементно-песчаном растворе М200, армированная сеткой d5, Вр1 100x100 – 100 мм Нижележащие слои учтены в разделе НД-2026-1-Р-1.1/1.2/1.3/1.4/2-КР 3. Плита монолитная железобетонная – 250 мм 4. Армированная полиэтиленовая пленка - 300 мкм 5. Экструдированный пенополистирол Пеноплэкс Фундамент или аналог (ρ=35 кг/м^3) – 100 мм 6. Гидроизоляция рулонная битумосодержащая – 2 слоя 7. Слои инженерной подготовки (бетонная/песчаная/щебеночная подготовка по геотекстилю 200 гр/м^2	108.89	
029, 030, 040, 056, 057, 058	0.10	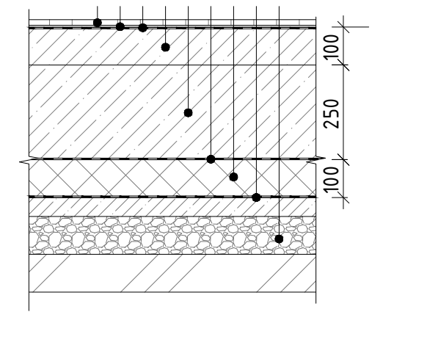	1. Плитка метлахская (Ктр=0,40; класс износостойкости 3) на клею см. раздел НД-2026-1-Р-1.1/1.3/1.4/2-АИ) – 15+5 мм 2. Гидроизоляция обмазочная на цементной основе (завести на стену, обработать узлы прохода и крепления трубопроводов) – 2 слоя 3. Грунтовка 4. Стяжка уклонообразующая на цементно-песчаном растворе М200, армированная сеткой d5, Вр1 100x100 – 50-100 мм Нижележащие слои учтены в разделе НД-2026-1-Р-1.1/1.2/1.3/1.4/2-КР 5. Плита монолитная железобетонная – 250 мм 6. Армированная полиэтиленовая пленка - 300 мкм 7. Экструдированный пенополистирол Пеноплэкс Фундамент или аналог (ρ=35 кг/м^3) – 100 мм 8. Гидроизоляция рулонная битумосодержащая – 2 слоя 9. Слои инженерной подготовки (бетонная/песчаная/щебеночная подготовка по геотекстилю 200 гр/м^2	25.56	Пол санитарного/санитарно-техническо го помещения; Завести гидроизоляцию на стену на высоту 200 миллиметров от уровня чистового покрытия, на узлы прохода и крепления трубопроводов (S= 30,65 м^2)
				238.86	
Этаж 1					
138, 140, 141, 171	1.5.2	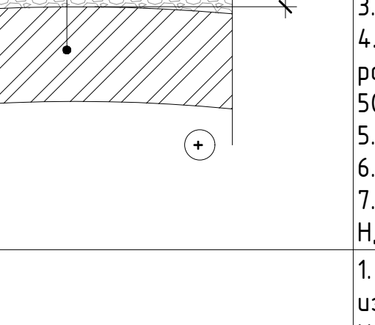	1. Керамогранитная плитка (Ктр=0,40; класс износостойкости 3) на клею см. раздел НД-2026-1-Р-1.1/1.3/1.4/2-АИ) – 15+5 мм 2. Гидроизоляция обмазочная на цементной основе (завести на стену, обработать узлы прохода и крепления трубопроводов) – 2 слоя 3. Грунтовка 4. Стяжка уклонообразующая на цементно-песчаном растворе М200, армированная сеткой d5, Вр1 100x100 – 50-100 мм 5. Армированная полиэтиленовая пленка – 300 мкм 6. Засыпка керамзитом М350 Ф10–20 – 170-430 мм 7. Существующее основание – кирпичный свод (см. раздел НД-2026-1-ТО1.3)	73.24	Пол санитарного/санитарно-техническо го помещения; Завести гидроизоляцию на стену на высоту 200 миллиметров от уровня покрытия, на узлы прохода и крепления трубопроводов (S= 100, 46 м^2); Обеспечить жесткую фиксацию керамзита – после укладки пролить цементным молочком
138, 140, 141, 171	1.5.2р		1. Керамогранитная плитка (Ктр=0,40; класс износостойкости 3) на клею см. раздел НД-2026-1-Р-1.1/1.3/1.4/2-РР.АИ) – 15+5 мм 2-7. см. тип 1.5.2	10.79	см. тип 1.5.2
113, 116, 117, 118, 142	1.13	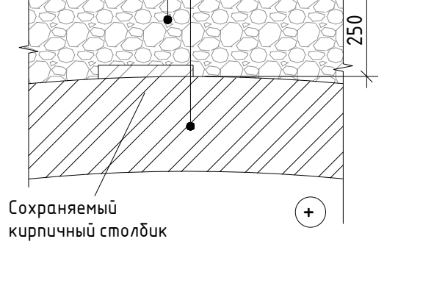	1. Керамогранитная плитка с раскладкой, имитирующей исторический рисунок паркета (Ктр не менее 0,35; класс износостойкости не менее 3) на клею – 15+5 мм 2. Стяжка на цементно-песчаном растворе М200, армированная сеткой d5, Вр1 100x100 – 70 мм 3. Армированная полиэтиленовая пленка – 300 мкм 4. Засыпка керамзитом М350 Ф10–20 – 190-390 мм 5. Существующее основание – кирпичный свод (см. раздел НД-2026-1-ТО1.3)	16.65	Обеспечить жесткую фиксацию керамзита – после укладки пролить цементным молочком
112	1.13.2	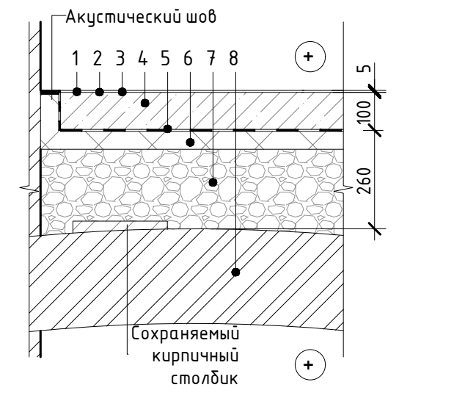	1. Антистатический наливной пол в два слоя – 5 мм 2. Токопроводящий грунт 3. Грунтовочный слой с устройством заземляющего контура (ленты медные с липким токопроводящим слоем, ширина 10 мм) 4. Стяжка на цементно-песчаном растворе М200, армированная сеткой d5, Вр1 100x100 – 100 мм 5. Армированная полиэтиленовая пленка – 300 мкм 6. Минераловатные плиты (ρ=110 кг/м^3) – 50 мм 7. Засыпка керамзитом М350 Ф10–20 – 190-390 мм 8. Существующее основание – кирпичный свод (см. раздел НД-2026-1-ТО1.3)	64.77	Плавающий пол технического помещения; По периметру помещения (Р=46,65 м) предусмотреть акустический шов толщиной 5 см с закладкой упругим утеплителем (плотность не менее 100 кг/м^3); Обеспечить жесткую фиксацию керамзита – после укладки пролить цементным молочком

Общая экспликация полов тома

Номер пом.	Тип пола	Схема пола	Данные элементов пола, мм	Площадь	Примечание
114, 115	1.13.3	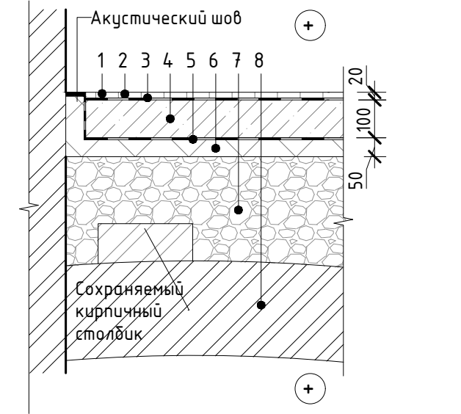	1. Керамогранитная плитка с раскладкой, имитирующей исторический рисунок паркета (Ктр=0,35; класс износостойкости 3) на клею см. раздел НД-2026-1-Р-1.1/1.3/1.4/2-РР.АИ) – 15+5 мм 2. Гидроизоляция обмазочная на цементной основе (завести на стену, обработать узлы прохода и крепления трубопроводов) – 2 слоя 3. Грунтовка 4. Стяжка на цементно-песчаном растворе М200, армированная сеткой d5, Вр1 100x100 – 100 мм 5. Армированная полиэтиленовая пленка – 300 мкм 6. Минераловатные плиты (ρ=110 кг/м^3) – 50 мм 7. Засыпка керамзитом М350 Ф10–20 – 190-390 мм 8. Существующее основание – кирпичный свод (см. раздел НД-2026-1-ТО1.3)	55.57	Плавающий пол технического помещения; По периметру помещения (Р=42,24 м) предусмотреть акустический шов толщиной 5 см с закладкой упругим утеплителем (плотность не менее 100 кг/м^3); Завести гидроизоляцию на стену на высоту 200 миллиметров от уровня покрытия, на узлы крепления и прохода трубопроводов (S=8,45 кв.м.); Обеспечить жесткую фиксацию керамзита – после укладки пролить цементным молочком
113, 116, 117, 118, 142	1.13р		1. Керамогранитная плитка с раскладкой, имитирующей исторический рисунок паркета (Ктр не менее 0,35; класс износостойкости не менее 3) на клею см. раздел НД-2026-1-Р-1.1/1.3/1.4/2-РР.АИ) – 15+5 мм 2-5. см. тип 1.13	53.74	Обеспечить жесткую фиксацию керамзита – после укладки пролить цементным молочком
119	1.14	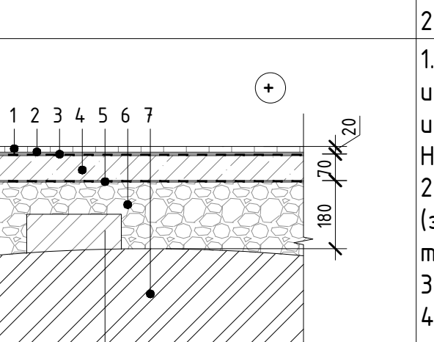	1. Керамогранитная плитка с раскладкой, имитирующей исторический рисунок паркета (Ктр=0,35; класс износостойкости 3) на клею см. раздел НД-2026-1-Р-1.1/1.3/1.4/2-РР.АИ) – 15+5 мм 2. Гидроизоляция обмазочная на цементной основе (завести на стену, обработать узлы прохода и крепления трубопроводов) – 2 слоя 3. Грунтовка 4. Стяжка на цементно-песчаном растворе М200, армированная сеткой d5, Вр1 100x100 – 70 мм 5. Армированная полиэтиленовая пленка – 300 мкм 6. Засыпка керамзитом М350 Ф10–20 – 180-380 мм 7. Существующее основание – кирпичный свод (см. раздел НД-2026-1-ТО1.3)	53.15	Обеспечить жесткую фиксацию керамзита – после укладки пролить цементным молочко; Завести гидроизоляцию на стену на высоту 200 миллиметров от уровня покрытия, на узлы крепления и прохода трубопроводов (S=62,45 кв.м.)
106, 107, 110, 120, 122	1.15	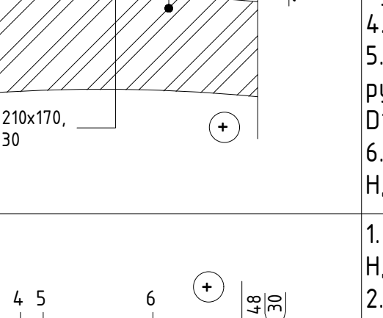	1. Чистовое покрытие – паркет дубовый на клею под лаком- см. том НД-2026-1-Р-2-АИ – 15+3 мм 2. Подложка под паркет – фанерные листы ФК водостойкие нешлифованные сорт 3/4, 2 слоя по 15 мм – 30 мм 3. Добор – разреженный дощатый настил 30x200 (шаг 250 мм) – 30 мм Существующая конструкция – см. раздел НД-2026-1-ТО1.3: 4. Лага 140x55 (шаг 700 мм) 5. Балка – бревно 210x170 (шаг 1430) по подкладке из рубероида, с проектной засыпкой пеностекольным щебнем D100 – 180-380 мм 6. Существующее основание – кирпичный свод (см. раздел НД-2026-1-ТО1.3)	11.89	Предусмотреть пропитку деревянных элементов конструкции пола огнебиозащитным составом (см. п VIII лист 1) (S=15,55м^2). После обработки деревянных элементов пола произвести дозасыпку пеностекольным щебнем до верха лаг
106, 107, 110, 120, 122	1.15р	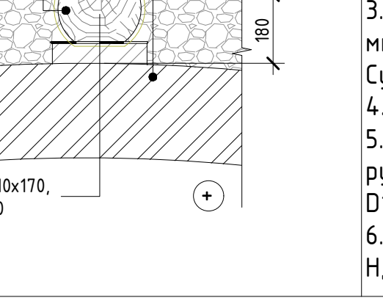	1. Восстанавливаемый паркет на клею под лаком - см. том НД-2026-1-Р-2-РР.АИ – 15+3 мм 2. Подложка под паркет – фанерные листы ФК водостойкие нешлифованные сорт 3/4, 2 слоя по 15 мм – 30 мм 3. Добор – разреженный дощатый настил 30x200 (шаг 250 мм) – 30 мм Существующая конструкция – см. раздел НД-2026-1-ТО1.3: 4. Лага 140x55 (шаг 700 мм) 5. Балка – бревно 210x170 (шаг 1430) по подкладке из рубероида, с проектной засыпкой пеностекольным щебнем D100 – 180-380 мм 6. Существующее основание – кирпичный свод (см. раздел НД-2026-1-ТО1.3)	12.00	Предусмотреть пропитку деревянных элементов конструкции пола огнебиозащитным составом (см. п VIII лист 1) (S=17,44м^2). После обработки деревянных элементов пола произвести дозасыпку пеностекольным щебнем до верха лаг
				351.79	
Этаж 2					
237, 255	2.12	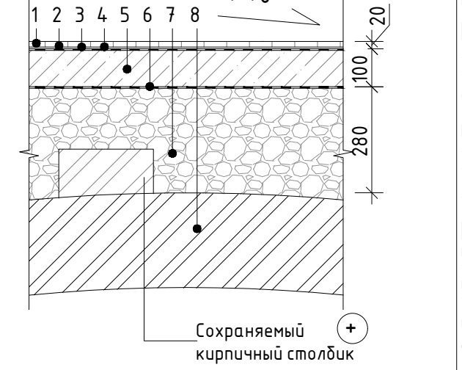	1. Плитка керамогранитная (Ктр=0,40; класс износостойкости 3) на клею см. раздел НД-2026-1-Р-1.1/1.3/1.4/2-АИ – 15+5 мм 2. Гидроизоляция обмазочная на цементной основе (завести на стену, обработать узлы прохода и крепления трубопроводов) – 2 слоя 3. Грунтовка 4. Стяжка уклонообразующая на цементно-песчаном растворе М200, армированная сеткой d5, Вр1 100x100 – 50-100 мм 5. Армированная полиэтиленовая пленка – 300 мкм 6. Засыпка керамзитом М350 Ф10–20 – 280-480 мм 7. Существующее основание – кирпичный свод (см. раздел НД-2026-1-ТО1.3)	12.70	Пол санитарного/санитарно-техническо го помещения; Завести гидроизоляцию на стену на высоту 200 миллиметров от уровня покрытия, на узлы прохода и крепления трубопроводов (S= 17,27м^2); Обеспечить жесткую фиксацию гранул керамзита – после укладки пролить цементным молочком
237	2.12.1	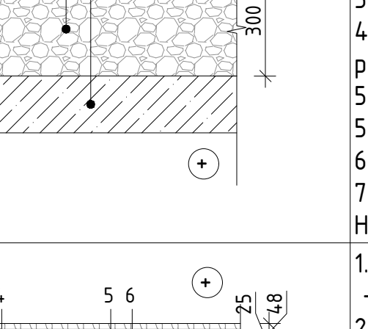	1. Плитка керамогранитная (Ктр=0,40; класс износостойкости 3) на клею см. раздел НД-2026-1-Р-1.1/1.3/1.4/2-АИ – 15+5 мм 2. Гидроизоляция обмазочная на цементной основе (завести на стену, обработать узлы прохода и крепления трубопроводов) – 2 слоя 3. Грунтовка 4. Стяжка уклонообразующая на цементно-песчаном растворе М200, армированная сеткой d5, Вр1 100x100 – 50-100 мм 5. Армированная полиэтиленовая пленка – 300 мкм 6. Засыпка керамзитом М350 Ф10–20 – 300 мм 7. Плита монолитная железобетонная (см. раздел НД-2026-1-Р-1.1-КР) – 150 мм	6.62	Пол санитарного/санитарно-техническо го помещения; Завести гидроизоляцию на стену на высоту 200 миллиметров от уровня покрытия, на узлы прохода и крепления трубопроводов (S= 10,36 м^2); Обеспечить жесткую фиксацию гранул керамзита – после укладки пролить цементным молочком
223, 225	2.13	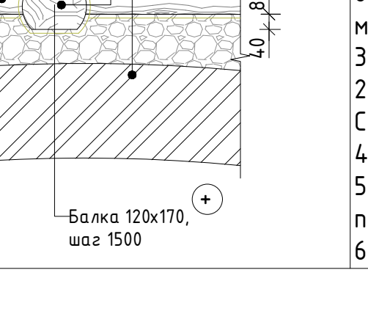	1. Чистовое покрытие – паркет дубовый на клею под лаком – 15+3 мм 2. Подложка под паркет – фанерные листы ФК водостойкие нешлифованные сорт 3/4, 2 слоя по 15 мм – 30 мм 3. Добор – разреженный деревянный настил 200x25 (шаг 250 мм) – 25 мм Существующая конструкция – см. раздел НД-2026-1-ТО1.3: 4. Лага 160x80 (шаг 700 мм) 5. Балка – бревно 120x170 (шаг 1500) с проектной засыпкой пеностекольным щебнем D100 – 130-390 мм 6. Существующее основание – кирпичный свод	12.59	Предусмотреть пропитку деревянных элементов конструкции пола огнебиозащитным составом (см. п VIII лист 1) (Общая S=72,01м^2, захв.1.1: S=5,05м^2, захв.2: S=66,96м^2). После обработки деревянных элементов пола произвести дозасыпку пеностекольным щебнем до верха лаг
				31.91	
Этаж 3					
326 1.1	3.5	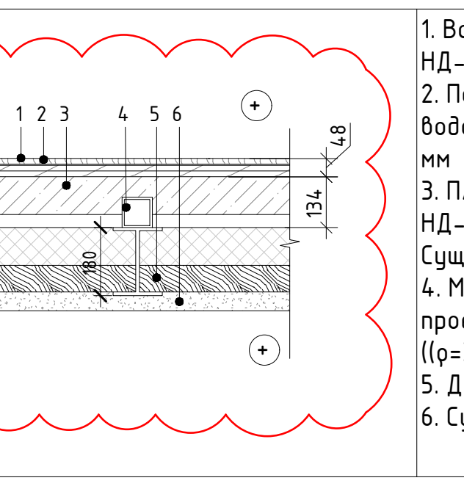	1. Восстанавливаемый паркет на клею под лаком - см. том НД-2026-1-Р-1.1-РР.АИ - 15+3 мм 2. Подложка под паркет – фанерные листы ФК водостойкие нешлифованные сорт 3/4, 2 слоя по 15 мм – 30 мм 3. Плита монолитная железобетонная (см. том НД-2026-1-Р-1.1-КР) – 100 мм Существующая конструкция – см. раздел НД-2026-1-ТО1.3: 4. Металлическая балка усиленная трубой и уголками с проектным заполнением пустот минеральной ватой ((ρ=35-45 кг/м^3) – 100 мм 5. Дощатый накат – 70 мм 6. Существующая штукатурка – 50 мм	67.11	Пустоты между металлическими балками заполнить минераловатным утеплителем (V= 6,7куб.м.)

Общая экспликация полов тома

Номер пом.	Тип пола	Схема пола	Данные элементов пола, мм	Площадь	Примечание
327	3.12.2	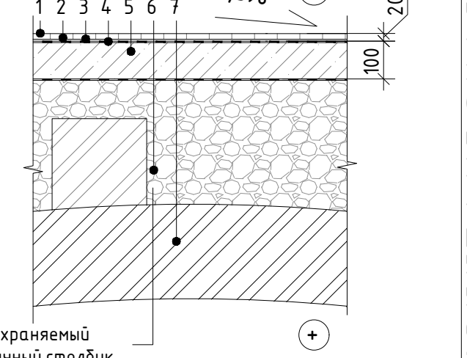	1. Плитка керамогранитная (Ктр=0,40; класс износостойкости 3) на клею см. раздел НД-2026-1-Р-1.1-АИ – 15+5 мм 2. Гидроизоляция обмазочная на цементной основе (завести на стену, обработать узлы прохода и крепления трубопроводов) – 2 слоя 3. Грунтовка 4. Стяжка уклонообразующая на цементно-песчаном растворе М200, армированная сеткой d5, Вр1 100x100 – 50-100 мм 5. Армированная полиэтиленовая пленка – 300 мкм 6. Засыпка керамзитом Ф10–20 М350 – 300-470 мм 7. Существующее основание – кирпичный свод (см. раздел НД-2026-1-ТО1.3)	10.65	Пол санитарного/санитарно-техническо го помещения; Завести гидроизоляцию на стену на высоту 200 миллиметров от уровня покрытия, на узлы прохода и крепления трубопроводов (S= 25,62 м^2); Обеспечить жесткую фиксацию гранул керамзита – после укладки пролить цементным молочком
327	3.12.3	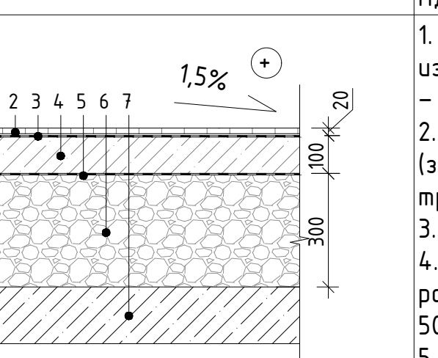	1. Плитка керамогранитная (Ктр=0,40; класс износостойкости 3) на клею см. раздел НД-2026-1-Р-1.1-АИ – 15+5 мм 2. Гидроизоляция обмазочная на цементной основе (завести на стену, обработать узлы прохода и крепления трубопроводов) – 2 слоя 3. Грунтовка 4. Стяжка уклонообразующая на цементно-песчаном растворе М200, армированная сеткой d5, Вр1 100x100 – 50-100 мм 5. Армированная полиэтиленовая пленка – 300 мкм 6. Засыпка керамзитом М350 Ф10–20 – 300 мм 7. Плита монолитная железобетонная (см. раздел НД-2026-1-Р-1.1-КР) – 150 мм	8.78	Пол санитарного/санитарно-техническо го помещения; Завести гидроизоляцию на стену на высоту 200 миллиметров от уровня покрытия, на узлы прохода и крепления трубопроводов (S= 25,62 м^2); Обеспечить жесткую фиксацию гранул керамзита – после укладки пролить цементным молочком
				86.54	
Этаж 5					
537, 540, 544, 546	5.11	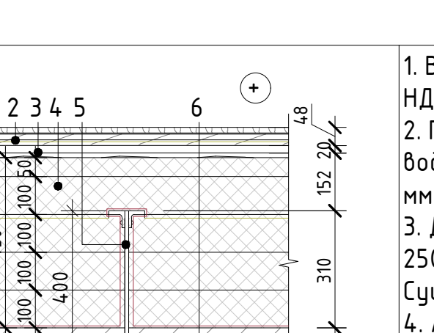	1. Восстанавливаемый паркет на клею под лаком - см. том НД-2026-1-Р-1.1/1.3-РР.АИ– 15+3 мм 2. Подложка под паркет – фанерные листы ФК водостойкие нешлифованные сорт 3/4, 2 слоя по 15 мм – 30 мм 3. Добор – разреженный деревянный настил 200x20 (шаг 250 мм) – 20 мм Существующая конструкция – см. раздел НД-2026-1-ТО1.3: 4. Лага 170x150 (шаг 570) 5. Клепанные металлические балки с проектным заполнением пустот минеральной ватой ((ρ=35-45 кг/м^3) – 3x100) – 400 мм 6. Штукатурка по сетке – 180 мм	215.22	Предусмотреть пропитку деревянных элементов конструкции пола огнебиозащитным составом (см. п VIII лист 1) деревянных конструкций полов (Общая S=16,45 ; захв. 1.1 - S= 13,71 м^2; захв. 1.3 - S=2,74 м^2); Пустоты между металлическими балками заполнить минераловатным утеплителем (V= 74,91 куб.м.)
538	5.12	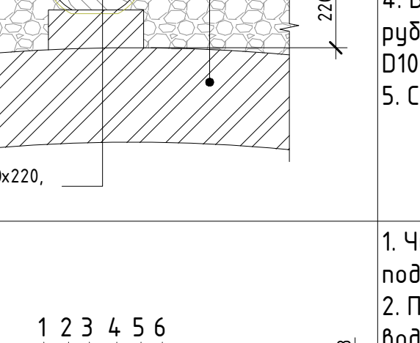	1. Восстанавливаемый паркет на клею под лаком - см. том НД-2026-1-Р-1.1-РР.АИ - 15+3 мм 2. Подложка под паркет – фанерные листы ФК водостойкие нешлифованные сорт 3/4, 3 слоя по 15 мм – 45 мм Существующая конструкция – см. раздел НД-2026-1-ТО1.3: 3. Лага 200x100 (шаг 1200) 4. Балка – бревно 220x250 (шаг 1320) по подкладке их рубероида,с проектной засыпкой пеностекольным щебнем D100 – 220-650 мм 5. Существующее основание – кирпичный свод	49.65	Предусмотреть пропитку деревянных элементов конструкции пола огнебиозащитным составом (см. п VIII лист 1) деревянных конструкций полов (Общая S=29,7 ; захв. 1.1- S= 29,7 м^2)
539	5.12.1	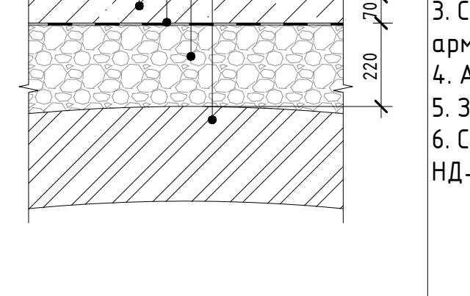	1. Чистовое покрытие – паркет штучный дубовый на клею под лаком – 15+3 мм 2. Подложка под паркет – фанерные листы ФК водостойкие нешлифованные сорт 3/4, 2 слоя по 15 мм – 30 мм 3. Стяжка на цементно-песчаном растворе М200, армированная сеткой d5, Вр1 100x100 – 100 мм 4. Армированная полиэтиленовая пленка – 300 мкм 5. Засыпка керамзитом Ф10–20 М350 – 220-590 мм 6. Существующее основание – кирпичный свод – см. раздел НД-2026-1-ТО1.3	10.20	Обеспечить жесткую фиксацию керамзита – после укладки пролить цементным молочком
524, 525, 526, 528, 530, 531, 533, 565	5.13	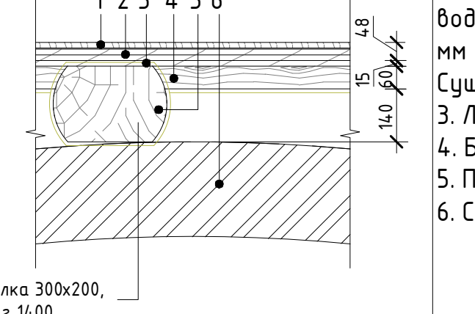	1. Чистовое покрытие – паркет дубовый на клею под лаком – 15+3 мм 2. Подложка под паркет – фанерные листы ФК водостойкие нешлифованные сорт 3/4, 3 слоя по 15 мм – 45 мм Существующая конструкция – см. раздел НД-2026-1-ТО1.3: 3. Лага 100x60 (шаг 600) – 60 мм 4. Балка перекрытия – бревно 300x200 (шаг 1400) – 200 мм 5. Прогон – бревно 360x210 – 210 мм 6. Существующее основание – кирпичный свод	112.05	Предусмотреть пропитку деревянных элементов конструкции пола огнебиозащитным составом (см. п VIII лист 1) деревянных конструкций полов (захв. 1.1- S= 88,82 м^2)
524, 525, 526, 528, 530, 531, 533, 565	5.13р	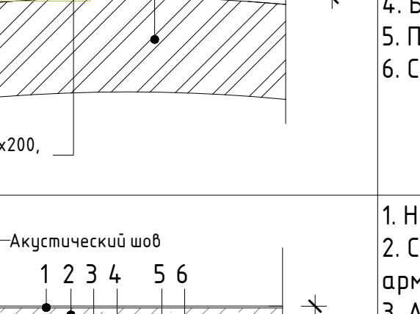	1. Восстанавливаемый паркет на клею под лаком - см. том НД-2026-1-Р-1.1/1.3-РР.АИ– 15+3 мм 2. Подложка под паркет – фанерные листы ФК водостойкие нешлифованные сорт 3/4, 3 слоя по 15 мм – 45 мм Существующая конструкция – см. раздел НД-2026-1-ТО1.3: 3. Лага 100x60 (шаг 600) – 60 мм 4. Балка перекрытия – бревно 300x200 (шаг 1400) – 200 мм 5. Прогон – бревно 360x210 – 210 мм 6. Существующее основание – кирпичный свод	39.75	Предусмотреть пропитку деревянных элементов конструкции пола огнебиозащитным составом (см. п VIII лист 1) деревянных конструкций полов (захв. 1.1- S= 29,39 м^2)
527	5.15	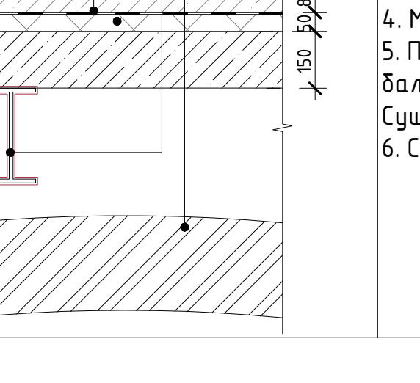	1. Наливной поулиретановый пол в два слоя – 5 мм 2. Стяжка на цементно-песчаном растворе М200, армированная сеткой d5, Вр1 100x100 – 100 мм 3. Армированная полиэтиленовая пленка – 300 мкм 4. Минераловатные плиты (ρ=110 кг/м^3) – 50 мм 5. Плита монолитная железобетонная по металлическим балкам (см. раздел НД-2026-1-Р-1.1-КР) – 150 мм Существующая конструкция – см. раздел НД-2026-1-ТО1.3: 6. Существующее основание – кирпичный свод	143.01	Плавающий пол технического помещения; По периметру помещения (Р=48,9 м) предусмотреть акустический шов толщиной 5 см с закладкой упругим утеплителем (плотность не менее 100 кг/м^3)

Общая экспликация полов тома

Номер пом.	Тип пола	Схема пола	Данные элементов пола, мм	Площадь	Примечание
541	5.20	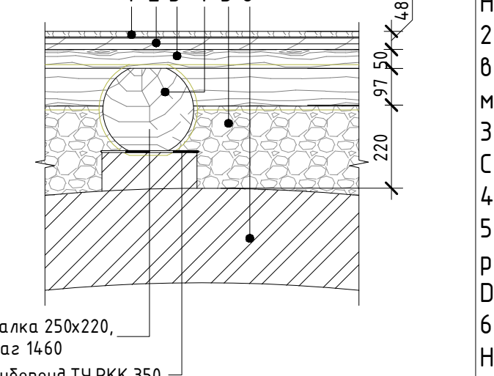	1. Восстанавливаемый паркет на клею под лаком - см. том НД-2026-1-Р-1.1-РР.АИ - 15+3 мм 2. Подложка под паркет – фанерные листы ФК водостойкие нешлифованные сорт 3/4, 2 слоя по 15 мм – 30 мм 3. Добор – доска разреженная 200x50 (шаг 500) – 50 мм Существующая конструкция – см. раздел НД-2026-1-ТО1.3: 4. Лага 200x100 (шаг 480) – 100 мм 5. Балка – бревно 220x240 (шаг 1460) по подкладке их рубероида, с проектной засыпкой пеностекольным щебнем D100 – 220-650 мм 6. Существующее основание – кирпичный свод (см. раздел НД-2026-1-ТО1.3)	70.75	Предусмотреть пропитку деревянных элементов конструкции пола огнебиозащитным составом (см. п VIII лист 1) деревянных конструкций полов (захв. 1.1- S= 39,49 м^2); После обработки деревянных элементов пола произвести дозасыпку пеностекольным щебнем до верха лаг
542	5.20.2	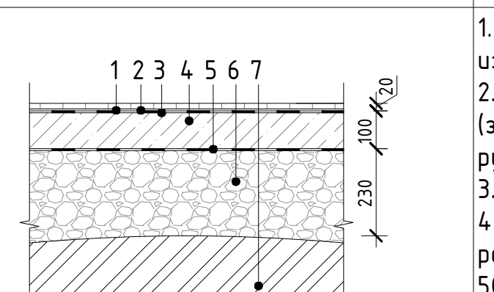	1. Керамогранитная плитка (Ктр=0,40; класс износостойкости 3) на клею – 15+5 мм 2. Гидроизоляция обмазочная на цементной основе (завести на стену, обработать узлы прохода и крепления рубопроводов) – 2 слоя 3. Грунтовка 4. Стяжка уклонообразующая на цементно-песчаном растворе М200, армированная сеткой d5, Вр1 100x100 – 50-100 мм 5. Армированная полиэтиленовая пленка – 300 мкм 6. Засыпка керамзитом М350 Ф10–20 – 230-300 мм 7. Существующее основание – кирпичный свод (см. раздел НД-2026-1-ТО1.3)	13.72	Пол санитарного/санитарно-техническо го помещения; Обеспечить жесткую фиксацию керамзита – после укладки пролить цементным молочком; Завести гидроизоляцию на стену на высоту 200 миллиметров от уровня покрытия, на узлы крепления и прохода трубопроводов (S=16,2 кв.м.)
542	5.20.3	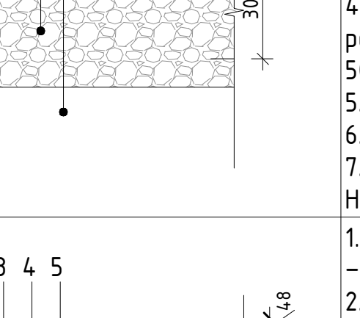	1. Керамогранитная плитка (Ктр=0,40; класс износостойкости 3) на клею – 15+5 мм 2. Гидроизоляция обмазочная на цементной основе (завести на стену, обработать узлы прохода и крепления трубопроводов) – 2 слоя 3. Грунтовка 4. Стяжка уклонообразующая на цементно-песчаном растворе М200, армированная сеткой d5, Вр1 100x100 – 50-100 мм 5. Армированная полиэтиленовая пленка – 300 мкм 6. Засыпка керамзитом М350 Ф10–20 – 300 мм 7. Плита монолитная железобетонная (см. раздел НД-2026-1-Р-1.1-КР) – 150 мм	8.42	Пол санитарного/санитарно-техническо го помещения; Обеспечить жесткую фиксацию керамзита – после укладки пролить цементным молочком; Завести гидроизоляцию на стену на высоту 200 миллиметров от уровня покрытия, на узлы крепления и прохода трубопроводов (S=10,57 кв.м.)
533	5.28.2	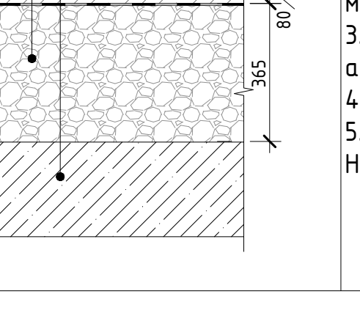	1. Чистовое покрытие – паркет дубовый на клею под лаком – 15+3 мм 2. Подложка под паркет – фанерные листы ФК водостойкие нешлифованные сорт 3/4, 2 слоя по 15 мм – 30 мм 3. Стяжка на цементно-песчаном растворе М200, армированная сеткой d5, Вр1 100x100 – 80 мм 4. Засыпка керамзитом Ф10–20 – 400 мм 5. Плита монолитная железобетонная (см. раздел НД-2026-1-Р-1.1-КР) – 250 мм	5.88	Обеспечить жесткую фиксацию керамзита – после укладки пролить цементным молочком
				668.63 1377.73	

Эскиз паркета 'корзинка"
Плашки 250x83,33 мм

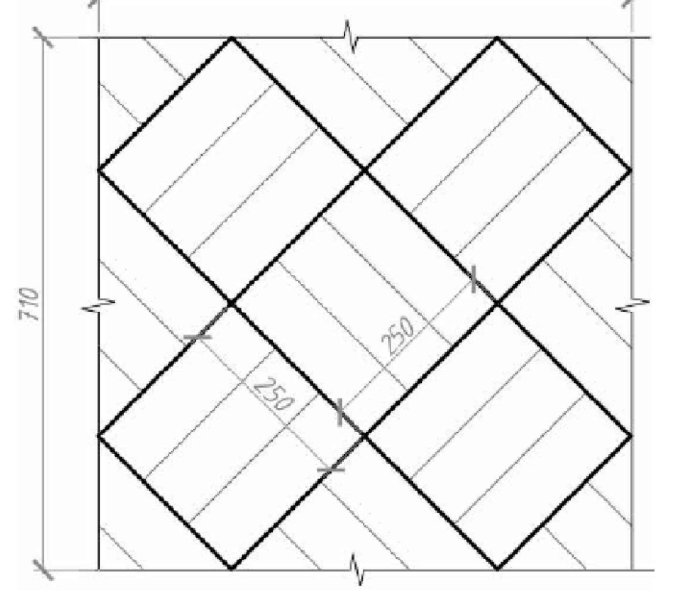

1	4	изм	01-09/26		24.09.26
Изм.	Кол.уч.	Лист	№док.	Подпись	Дата
Разработал		Лысюк			03.26
Рук. проекта		Суша			03.26
ГИП		Чапова			03.26
ГАП		Ермолаева			03.26
Н. контр.		Шапченко			03.26

НД-2026-1-Р-1.1-АР2

г. Санкт-Петербург, пл. Труда, д. 4, литера В

«Ремонт, реставрация и приспособление для современного использования (капитальный ремонт, оснащение технологическим оборудованием, в том числе проектирование) объектов культурного наследия федерального значения «Дворец», «Манеж», «Корпус служебный», «Конюшни главные дворцовые», расположенных по адресу: г. Санкт-Петербург, пл. Труда, д. 4, литера В, входящих в состав объекта культурного наследия федерального значения «Дворец Великого князя Николая Николаевича (Ксенинский институт)»

Стадия	Лист	Листов
Р	23	28

«Дворец». Общая экспликация полов тома по этажам -1-5

ОБЩЕСТВО С ОГРАНИЧЕННОЙ ОТВЕТСТВЕННОСТЬЮ
НИиПИ СПЕЦРЕСТАВРАЦИЯ

Согласовано
Взам. инв. №
Подп. и дата
Инв. № подл.

A2x3 (594x1261)