Маркировочный план фрагмента 5 этажа в осях 12-18/Д-Р

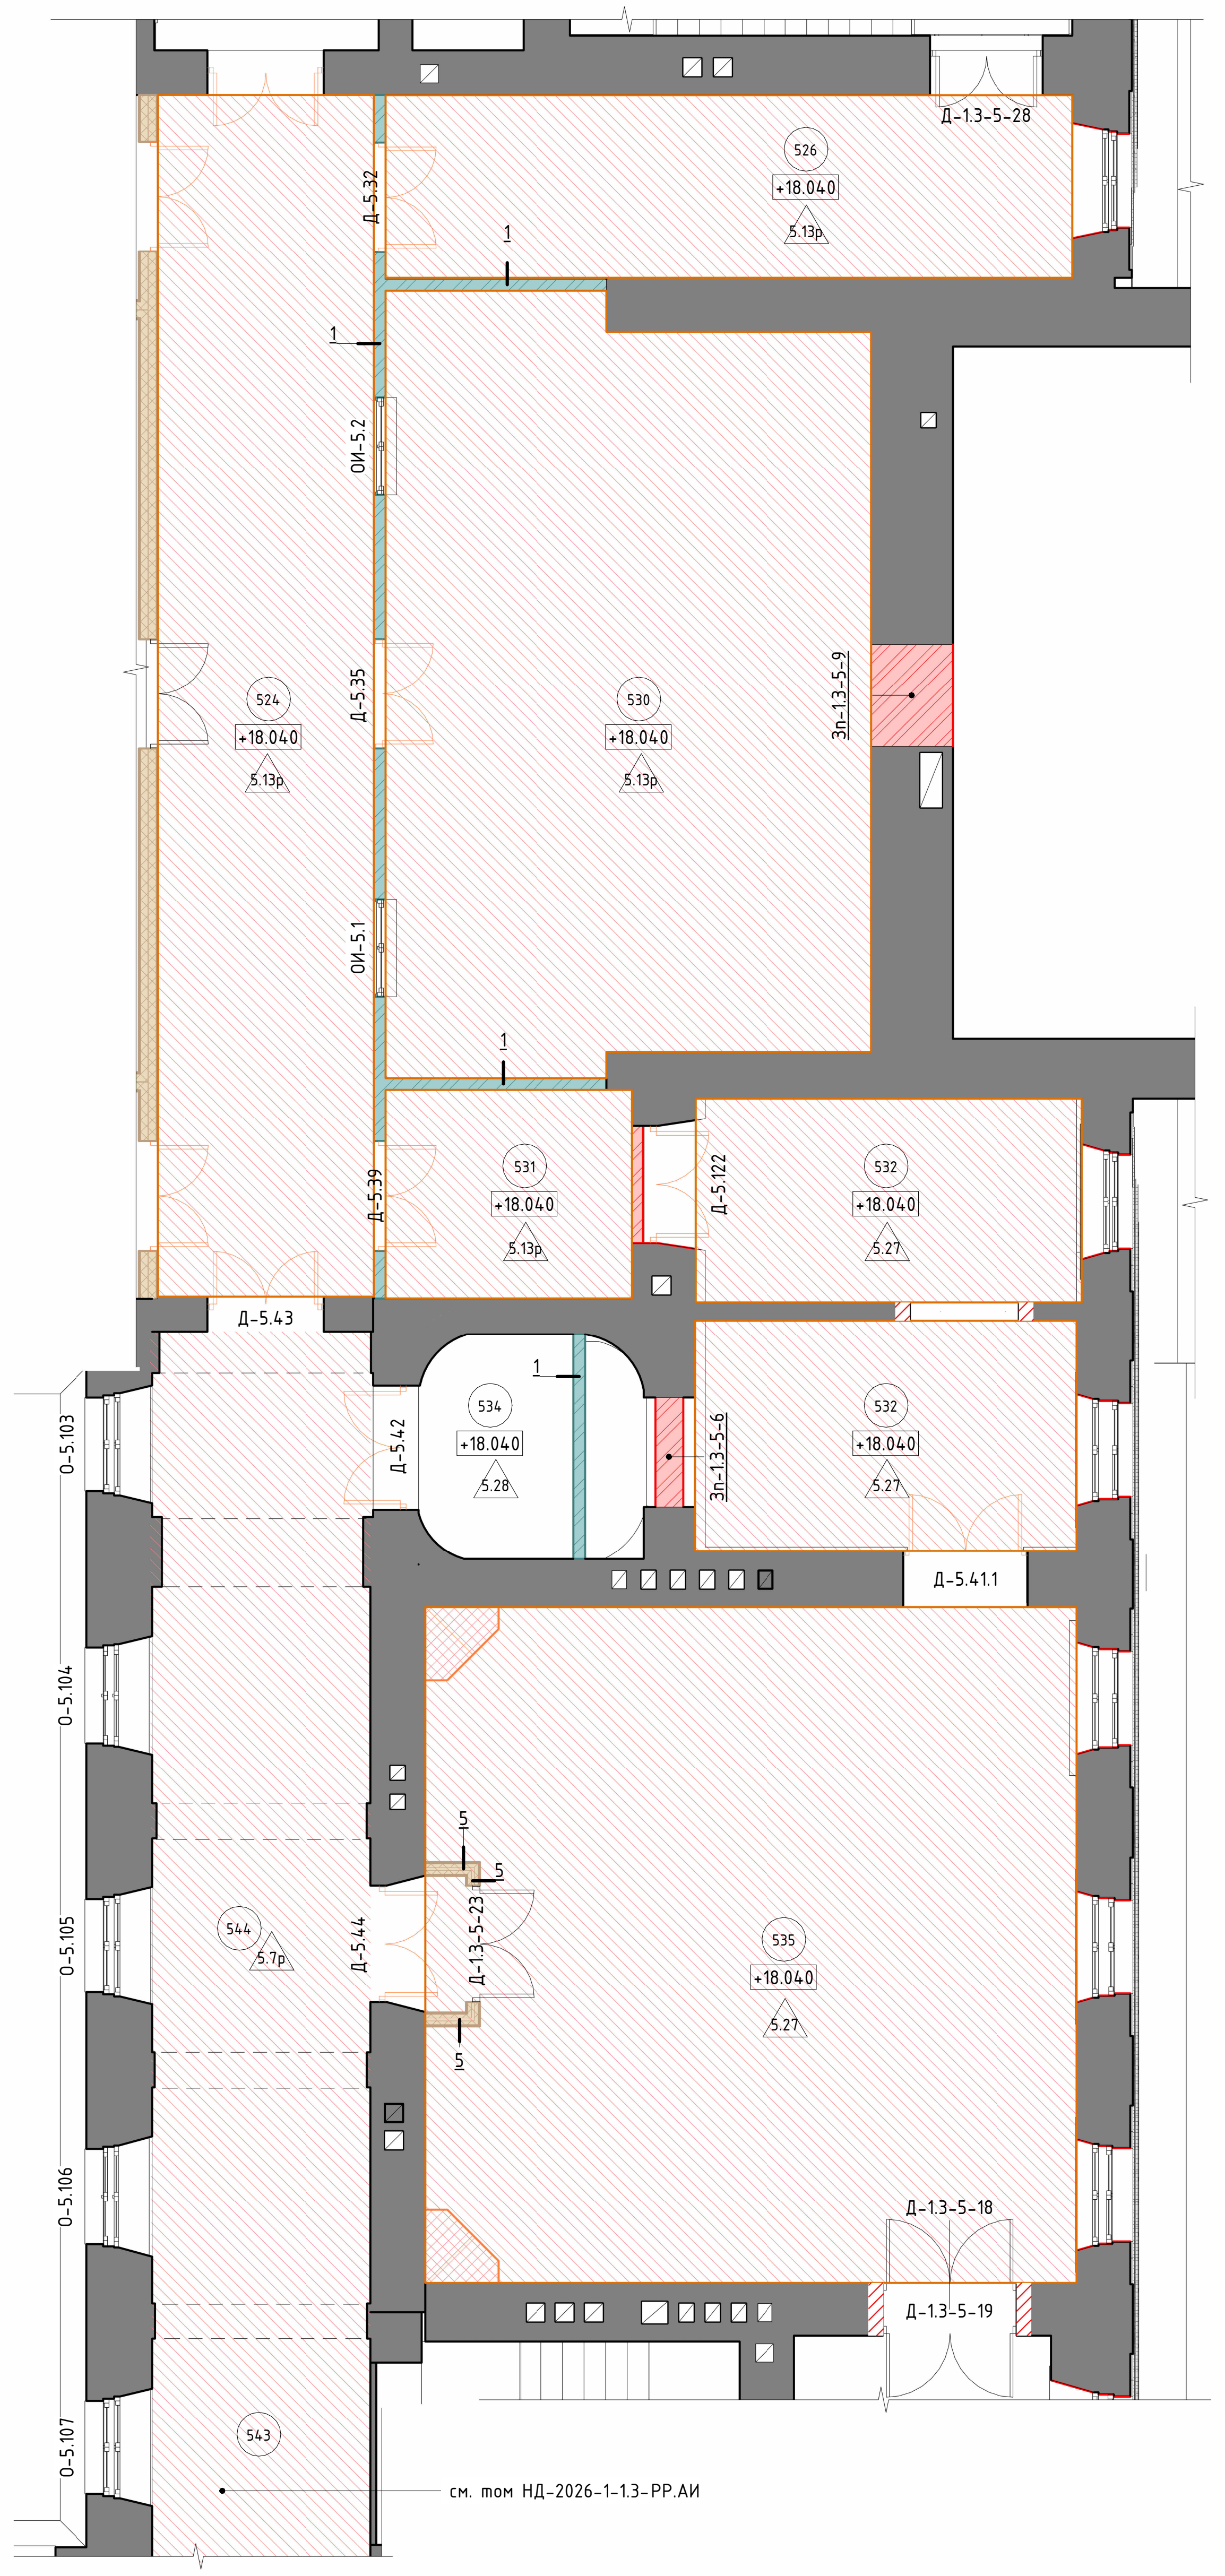

Маркировочный план фрагмента 5 этажа в осях 1-13/А-Г (1 : 75)

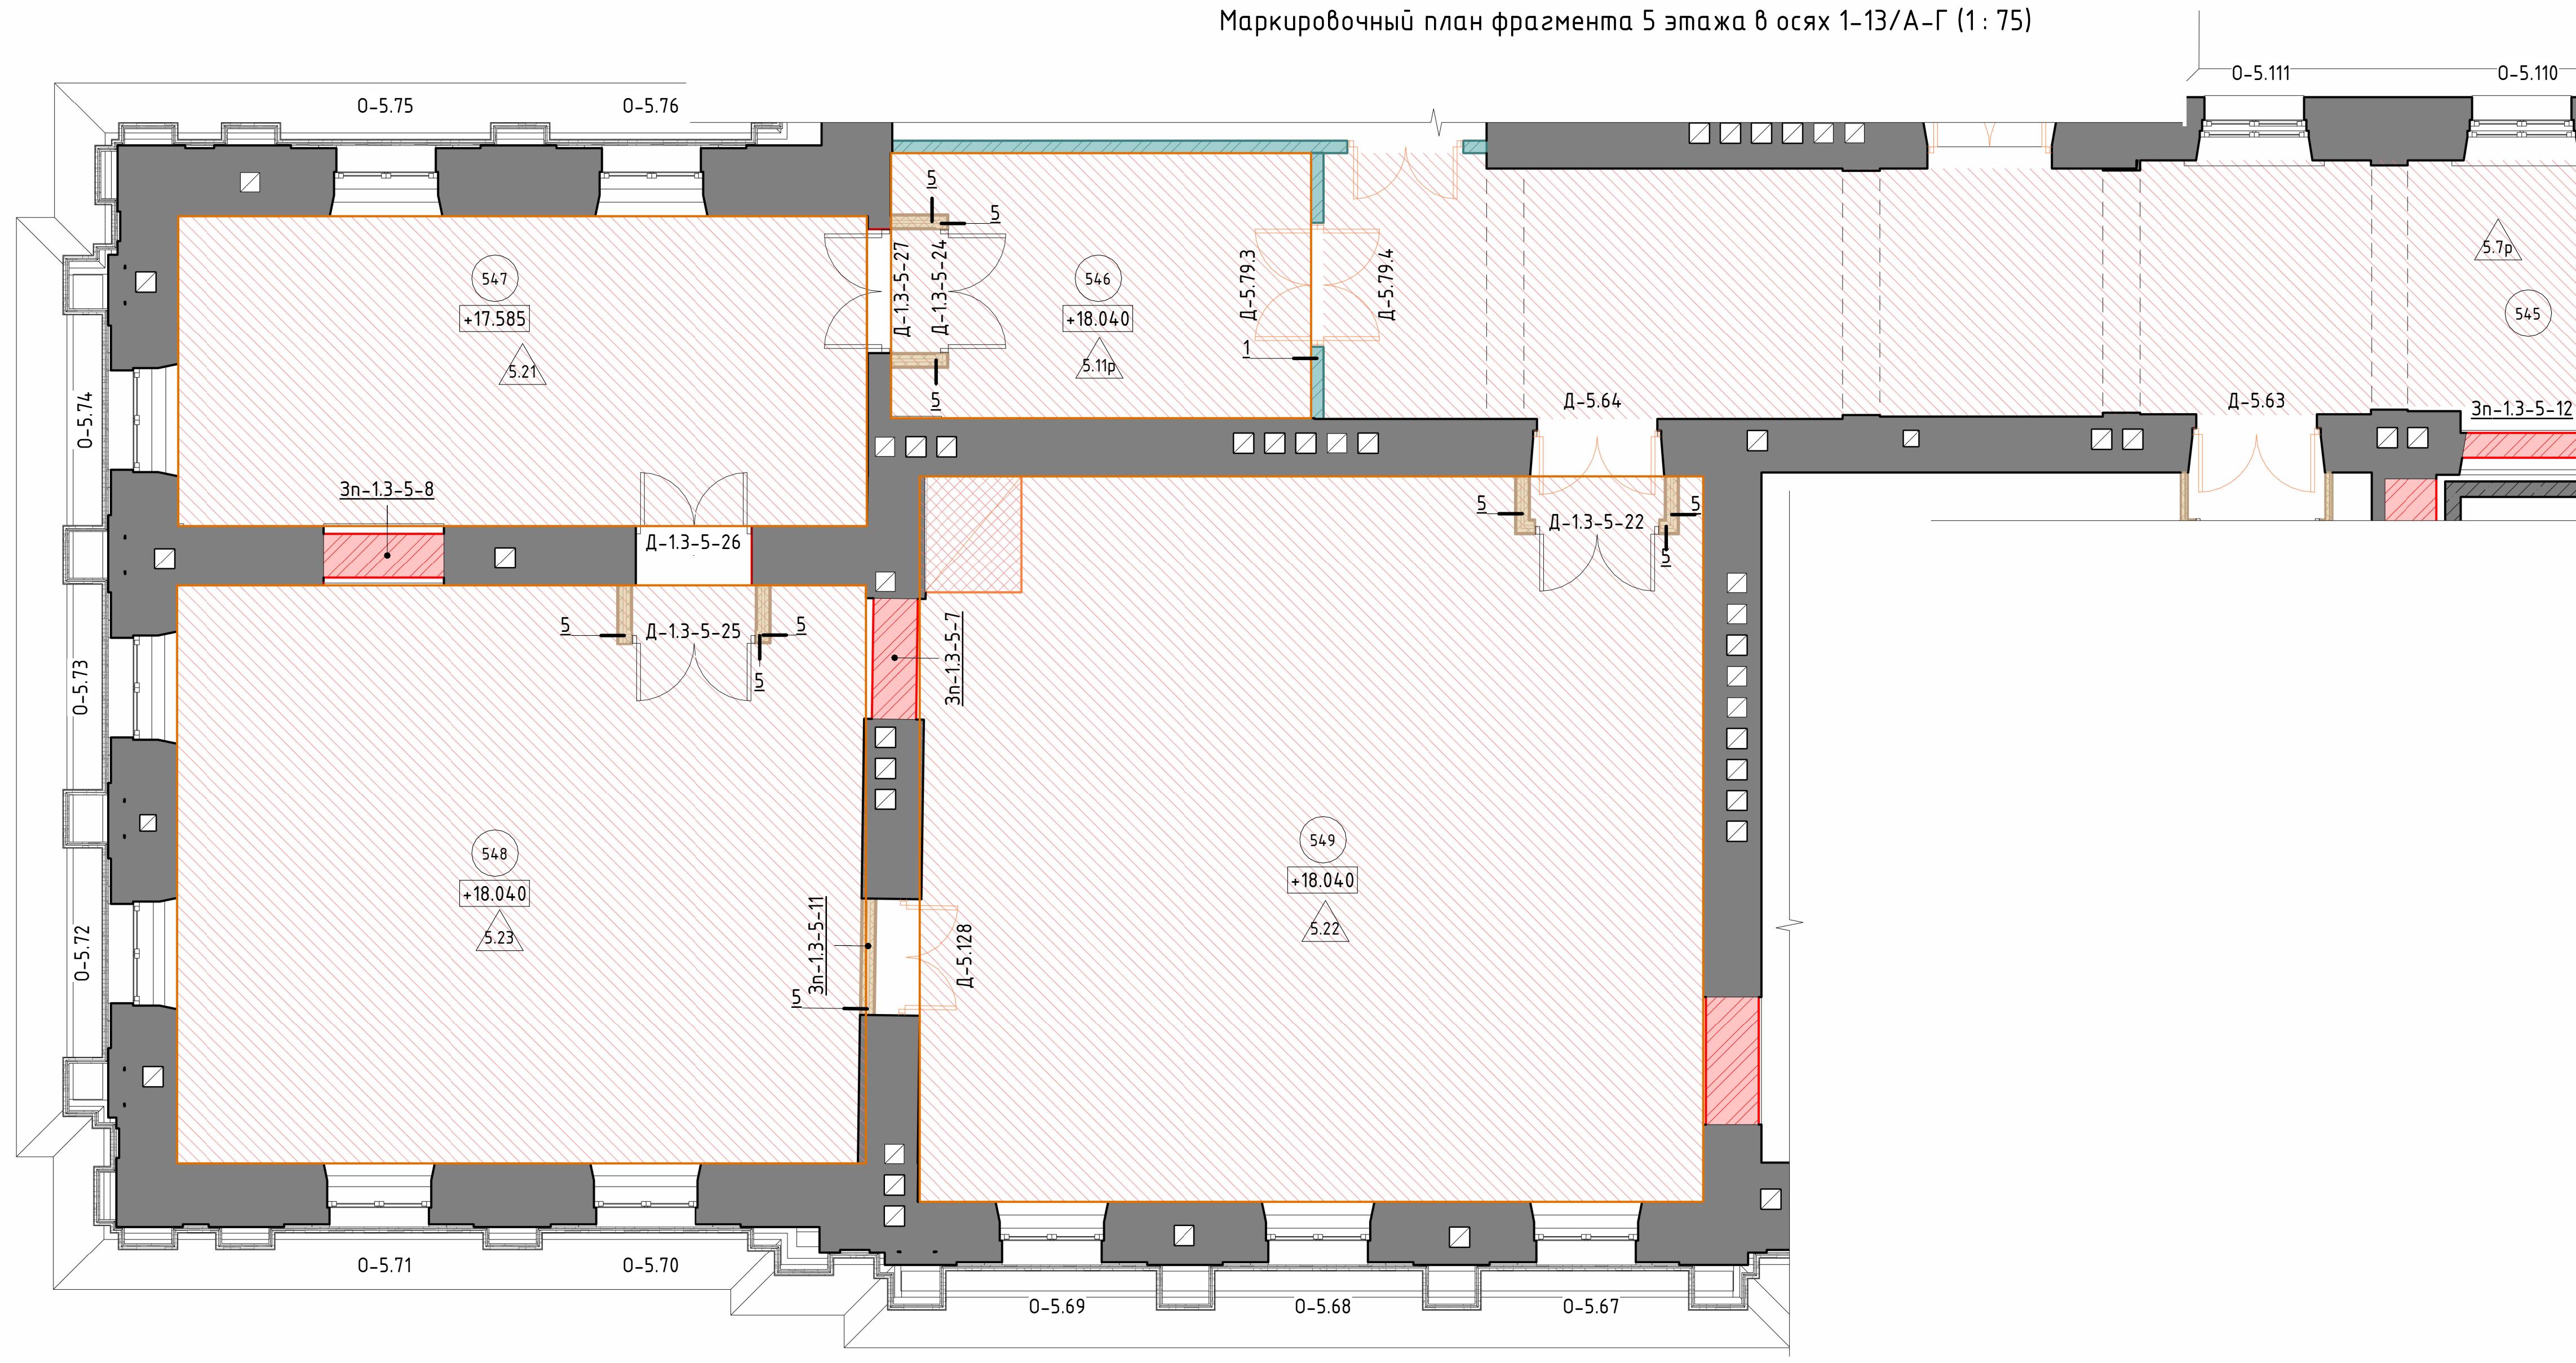

Экспликация помещений фрагмента 5 этажа в осях 1-18/А-Р

Номер	Имя	Площадь, кв. м.	Кат. пом.
524	Коридор	48.75	
526	Коридор	23.60	
530	Кладовая музыкальных инструментов	68.38	В3
531	ПУИ	9.55	В4
532	Кладовая музыкальных инструментов	31.31	В3
534	Коридор	6.26	
535	Репетиторий	82.48	
543	Коридор	55.77	
544	Коридор	29.78	
545	Коридор	54.96	
546	Коридор	18.51	
547	Репетиторий	35.55	
548	Репетиторий	65.90	
549	Репетиторий	94.33	
		625.12	

Ведомость закладываемых проемов фрагмента 5 этажа в осях 1-18/А-Р

Марка	Наименование	Объем, куб. м.	Примечание
Зп-1.3-5-5	Кирпичная кладка	0.72	
Зп-1.3-5-6	Кирпичная кладка	1.71	
Зп-1.3-5-7	Кирпичная кладка	2.56	
Зп-1.3-5-8	Кирпичная кладка	2.61	
Зп-1.3-5-9	Кирпичная кладка	3.53	
Зп-1.3-5-10	Кирпичная кладка	3.37	
Зп-1.3-5-11	КНАУФ перегородка типа С366	0.86	
Зп-1.3-5-12	Кирпичная кладка	1.37	
		16.72	

Ведомость возводимых перегородок и стен фрагмента 5 этажа в осях 1-18/А-Р

Марка	Наименование	Площадь, кв м	Примечание
1	Перегородка из бетонного камня	104.94	
5	КНАУФ перегородка типа С366	28.28	
		133.22	

Общая экспликация полов фрагмента 5 этажа в осях 1-18/А-Р

Тип пола	Схема пола	Данные элементов пола, мм	Площадь	Примечание
Этаж 5				
5.7р	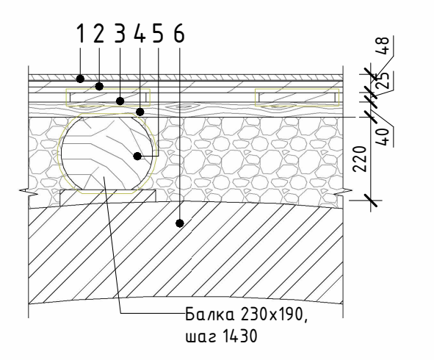 1 2 3 4 5 6 Балка 230х190, шаг 1430	1. Восстанавливаемый паркет на клею под лаком - см. том НД-2026-1-Р-1.3/2-РР.АИ - 15+3 мм. 2. Подложка под паркет – фанерные листы ФК водостойкие нешлифованные сорт 3/4, 2 слоя по 15 мм – 30 мм 3. Добор – разреженный деревянный настил 45х120 с организацией врубок (шаг 380 мм) – 25 мм Существующее основание – см. раздел НД-2026-1-ТО1.3: 4. Лага 140х40 (шаг 300) 5. Балка – бревно 230х190 (шаг 1430) на кирпичных столбиках по подкладке из рубероида, с проектной засыпкой пеностекольным щебнем D100 – 220-340 мм 6. Существующее основание – кирпичный свод	139.44	Предусмотреть пропитку деревянных элементов конструкции пола огнебиозащитным составом (см. п VIII лист 1) (захв.1.3: S=79,08м²). После обработки деревянных элементов пола произвести дозасыпку пеностекольным щебнем до верха лаг
5.11р	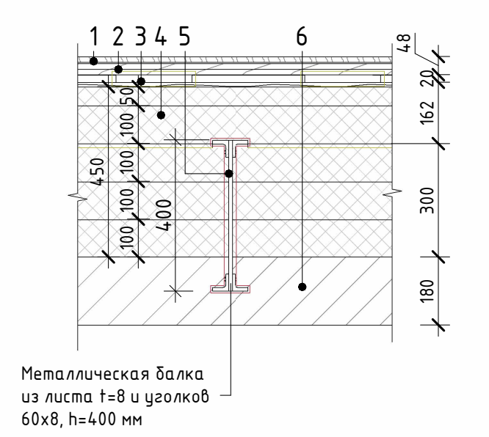 1 2 3 4 5 6 Металлическая балка из листа t=8 и уголков 60х8, h=400 мм	1. Восстанавливаемый паркет на клею под лаком - см. том НД-2026-1-Р-1.1/1.3-РР.АИ– 15+3 мм 2. Подложка под паркет – фанерные листы ФК водостойкие нешлифованные сорт 3/4, 2 слоя по 15 мм – 30 мм 3. Добор – разреженный деревянный настил 20х120 (шаг 380 мм) – 20 мм Существующая конструкция – см. раздел НД-2026-1-ТО1.3: 4. Лага 170х150 (шаг 570) 5. Клепанные металлические балки с проектным заполнением пустот минеральной ватой ((ρ=35-45 кг/м³) – 3х100) – 400 мм 6. Штукатурка по сетке – 180 мм	26.45	Предусмотреть пропитку деревянных элементов конструкции пола огнебиозащитным составом (см. п VIII лист 1) (Общая S=16,45 ; захв. 1.1: S=13,71 м²; захв. 1.3 - S=2,74 м²); Пустоты между металлическими балками заполнить минераловатным утеплителем (V= 74,91 куб.м.)
5.13р	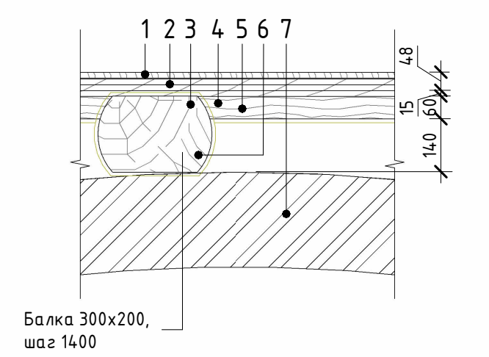 1 2 3 4 5 6 7 Балка 300х200, шаг 1400	1. Восстанавливаемый паркет на клею под лаком - см. том НД-2026-1-Р-1.1/1.3-РР.АИ – 15+3 мм 2. Подложка под паркет – фанерные листы ФК водостойкие нешлифованные сорт 3/4, 3 слоя по 15 мм – 45 мм 3. Дополнительные лаги между исторических лаг 45х120 с организацией врубок (шаг 380 мм) – 45 мм Существующая конструкция – см. раздел НД-2026-1-ТО1.3: 4. Лага 100х60 (шаг 600) – 60 мм 5. Балка перекрытия – бревно 300х200 с проектной засыпкой пеностекольным щебнем D100 – 220-340 мм (шаг 1400) – 200 мм 6. Прогон – бревно 360х210 – 210 мм 7. Существующее основание – кирпичный свод	153.28	Предусмотреть пропитку деревянных элементов конструкции пола огнебиозащитным составом (см. п VIII лист 1) (захв. 1.1: S=29,39 м²). После обработки деревянных элементов пола произвести дозасыпку пеностекольным щебнем до верха лаг
5.21	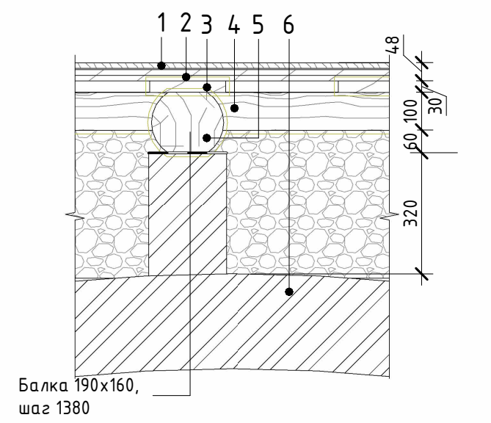 1 2 3 4 5 6 Балка 190х160, шаг 1380	1. Восстанавливаемый паркет на клею под лаком - см. том НД-2026-1-Р-1.3-РР.АИ – 15+3 мм 2. Подложка под паркет – фанерные листы ФК водостойкие нешлифованные сорт 3/4, 2 слоя по 15 мм – 30 мм 3. Добор – разреженный деревянный настил 45х120 с организацией врубок (шаг 380 мм) – 30 мм Существующая конструкция – см. раздел НД-2026-1-ТО1.3: 4. Лага 200х100 (шаг 1000) на кирпичных столбиках 5. Балка – бревно 190х160 (шаг 1380) на кирпичных столбиках по подкладке из рубероида, с проектной засыпкой пеностекольным щебнем D100 – 320-350 мм 6. Существующее основание – кирпичный свод	35.56	Предусмотреть пропитку деревянных элементов конструкции пола огнебиозащитным составом (см. п VIII лист 1) (захв. 1.3: S=18,62 м²). После обработки деревянных элементов пола произвести дозасыпку пеностекольным щебнем до верха лаг
5.22	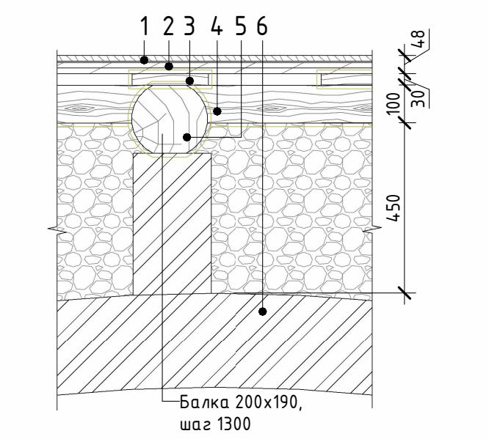 1 2 3 4 5 6 Балка 200х190, шаг 1300	1. Восстанавливаемый паркет на клею под лаком - см. том НД-2026-1-Р-1.3-РР.АИ – 15+3 мм 2. Подложка под паркет – фанерные листы ФК водостойкие нешлифованные сорт 3/4, 2 слоя по 15 мм – 30 мм 3. Добор – разреженный деревянный настил 45х120 с организацией врубок (шаг 380 мм) – 30 мм Существующая конструкция – см. раздел НД-2026-1-ТО1.3: 4. Лага 100х215 (шаг 560) - 100 мм 5. Балка – бревно 220х180 (шаг 1380) на кирпичных столбиках по подкладке из рубероида, с проектной засыпкой пеностекольным щебнем D100 – 220-650 мм 6. Существующее основание – кирпичный свод	97.40	Предусмотреть пропитку деревянных элементов конструкции пола огнебиозащитным составом (см. п VIII лист 1) (захв. 1.3: S=75,01 м²). После обработки деревянных элементов пола произвести дозасыпку пеностекольным щебнем до верха лаг
5.23	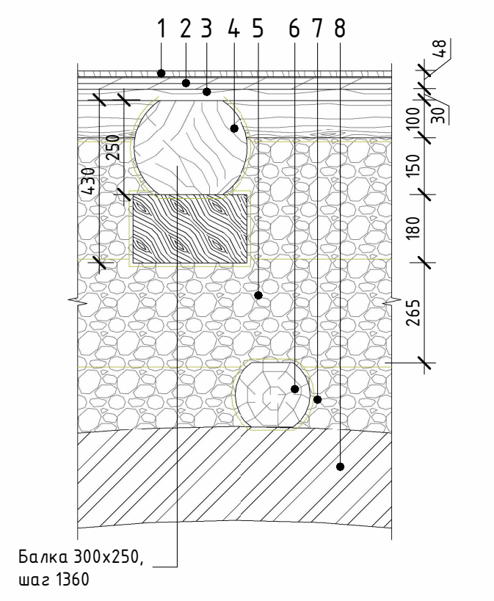 1 2 3 4 5 6 7 8 Балка 300х250, шаг 1360	1 Восстанавливаемый паркет на клею под лаком - см. том НД-2026-1-Р-1.3-РР.АИ – 15+3 мм 2. Подложка под паркет – фанерные листы ФК водостойкие нешлифованные сорт 3/4, 2 слоя по 15 мм – 30 мм 3. Добор – разреженный деревянный настил 45х120 с организацией врубок (шаг 380 мм) – 30 мм Существующая конструкция – см. раздел НД-2026-1-ТО1.3: 4. Лага 200х100 (шаг 520) 5. Балка – бревно 300х250 (шаг 1360) на подкладках из бревна 250х180, с проектной засыпкой пеностекольным щебнем D100 – 430 мм 6. Прогон пристенный – бревно 210х265 (шаг 1360) на подкладках из бревна 200х170 7. Существующее основание – кирпичный свод	69.64	Предусмотреть пропитку деревянных элементов конструкции пола огнебиозащитным составом (см. п VIII лист 1) (захв. 1.3: S=53,49 м²). После обработки деревянных элементов пола произвести дозасыпку пеностекольным щебнем до верха лаг
5.27	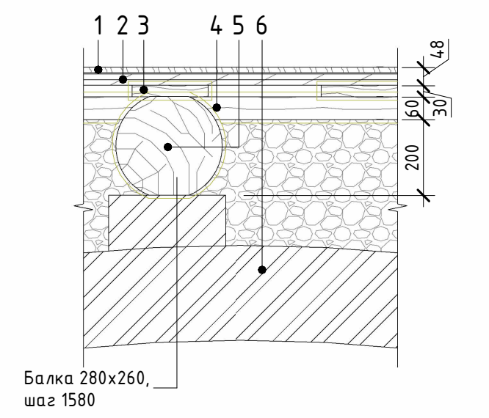 1 2 3 4 5 6 Балка 280х260, шаг 1580	1 .Восстанавливаемый паркет на клею под лаком - см. том НД-2026-1-Р-1.3-РР.АИ – 15+3 мм 2. Подложка под паркет – фанерные листы ФК водостойкие нешлифованные сорт 3/4, 2 слоя по 15 мм – 30 мм 3. Добор – разреженный деревянный настил 45х120 с организацией врубок (шаг 380 мм) – 30 мм Существующая конструкция – см. раздел НД-2026-1-ТО1.3: 4. Лага 180х60 (шаг 900) 5. Балка – бревно 260х280 (шаг 1580) по подкладке из рубероида,с проектной засыпкой пеностекольным щебнем D100 – 220-650 мм 6. Существующее основание – кирпичный свод – см. ТО	120.27	Предусмотреть пропитку деревянных элементов конструкции пола огнебиозащитным составом (см. п VIII лист 1) (захв. 1.3: S=77,98м²). После обработки деревянных элементов пола произвести дозасыпку пеностекольным щебнем до верха лаг
5.28	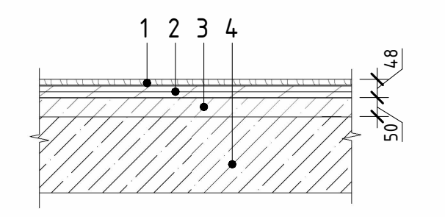 1 2 3 4	1. Чистовое покрытие – паркет штучный дубовый на клею под лаком (рисунок паркета "корзинка косая") – 15+3 мм 2. Подложка под паркет – фанерные листы ФК водостойкие нешлифованные сорт 3/4, 2 слоя по 15 мм – 30 мм 3. Стяжка на цементно-песчаном растворе М200, армированная сеткой d5, Вр1 100х100 – 80 мм 4. Плита монолитная железобетонная (см. раздел НД-2026-1-Р-1.1/1.2/1.3/1.4/2-КР) – 200 мм	6.26	
			648.28	

Условные обозначения:

1	– Ось координации
+0,000	– Отметка уровня
▨	– Реставрируемые помещения
▬	– Сохраняемые конструкции
▨	– Пробиваемый проем
🟥	– Закладываемый проем
🟩	– Рядовая перегородка с обшивкой ГКЛ-листами
🟦	– Влагостойкая перегородка с обшивкой КНАУФ-листами АКВАПАНЕЛЬ
🟥	– Огнестойкая перегородка обшивкой КНАУФ-листами ФАЙЕРБОРД
▨	– Перегородка из бетонного камня
🟪	– Смешанная перегородка
▨	– Сборная конструкция из фанеры
🟨	– Акустическая перегородка
Д-1.3-1-1П	– Марка дверного заполнения
О-1.1	– Марка оконного заполнения
1.1	– Марка пола
Зп-1.3-1-1	– Марка закладываемого проема
1.1	– Марка стены
– – – –	– Обмазочная гидроизоляция "мокрых" помещений

1. Данный лист смотреть совместно листами 5, 12, 15-22 данного тома;
2. Общая спецификация возводимых стен и перегородок дана на листе 19 данного тома;
3. Общая спецификация экспликация устраиваемых полов дана на листе 18 данного тома;
4. Общая спецификация элементов дверных и оконных заполнений дана на листе 20-21 данного тома;
5. Принципиальные решения по ремонту дверных проемов даны на листе 22 данного тома;
6. Маркировка проемов и ниш сквозная по этажу фрагмента, дана в стенах и перегородках;
7. Узлы устройства перегородок см. технологические карты, альбомы технических решений и комплектных систем производителей (см. лист 1 данного тома);
8. Реставрационные чертежи, в том числе чертежи печей и каминов, см. тома НД-2026-1-1.3-РР.АИ;
9. Реставрационные чертежи столярных дверных и оконных заполнений см. тома НД-2026-1-1.3-РР.ДВ, НД-2026-1-1.3-РР.ОК
10. Рисунок штучного паркета см. л 18 данного тома

1	-	Зам.	01-10/26		10.26
Изм.	Кол.уч.	Лист	№док.	Подпись	Дата
Разработал		Лысюк			03.26
Рук. проекта		Суша			03.26
ГИП		Чапова			03.26
ГАП		Ермолаева			03.26
Н. контр.		Шапченко			03.26

НД-2026-1-Р-1.3-АР2

г. Санкт-Петербург, пл. Труда, д. 4, литера В

«Ремонт, реставрация и приспособление для современного использования (капитальный ремонт, оснащение технологическим оборудованием, в том числе проектирование) объектов культурного наследия федерального значения «Дворец», «Манеж», «Корпус служебный», «Конюшни главные дворцовые», расположенных по адресу: г. Санкт-Петербург, пл. Труда, д. 4, литера В, входящих в состав объекта культурного наследия федерального значения «Дворец Великого князя Николая Николаевича (Ксенинский институт)»

Стадия	Лист	Листов
Р	11	22

«Дворец». Маркировочный план фрагмента 5 этажа в осях 1-18/А-Р

ОБЩЕСТВО С ОГРАНИЧЕННОЙ ОТВЕТСТВЕННОСТЬЮ
НИиПИ СПЕЦРЕСТАВРАЦИЯ

A2x3 (594x1261)

Согласовано

Взам. инв. №

Подп. и дата

Инв. № подл.